



*Индивидуальный жилой дом по адресу:
«Российская федерация, Московская область,
г. о. Домодедово, п. Государственного племенного завода
"Константиново", тер. КП "Юсупово Вилладж"
участок с кад. номером 50:28:0050421:2962»
КР-2. Конструкции выше отметки 0,000*

ГАП _____ Филатов А. Г.

город Москва, 2026 г.

Ведомость чертежей

Лист	Наименование	Примечание	Лист	Наименование	Примечание
1	Обложка		28	План кровли	
2	Ведомость чертежей		29	Спецификация к плану кровли	
3	Пояснительная записка		30	Узлы кровли	
4	Схема планировочной организации земельного участка		31	Узлы кровли (продолжение)	
5	План этажа на отм. + 0. 000		32	Разрез по вентканалам	
6	Схема расположения отсечной гидроизоляции				
7	3D вид 1				
8	3D вид 2				
9	3D вид 3				
10	3D вид 4				
11	Разрез 1-1				
12	Разрез 2-2				
13	Кладочный план на отм. + 0. 000				
14	Узлы армирования кладки				
15	Спецификация по газобетонным блокам				
16	План перемычек 1-го этажа				
17	Схема фасада 1				
18	Схема фасада 2				
19	Схема фасада 3				
20	Схема фасада 4				
21	План плиты перекрытия на отм. + 3. 480				
22	Спецификация к плите перекрытия на отм. +3,480				
23	Верхнее дополнительное армирование плиты на отм. + 3. 300				
24	Нижнее дополнительное армирование плиты на отм. + 3. 300				
25	План плиты перекрытия на отм. + 4. 680				
26	Нижнее дополнительное армирование плиты на отм. +4,680				
27	Верхнее дополнительное армирование плиты на отм. +4,680				

Согласовано			
Взам. инв. №			
Подпись и дата			
Инв. № подл.			

						Проект жилого дома			
Изм.	Кол.уч.	Лист	№ док.	Подпись	Дата				
ГАП		Филатов А.Г.			10.06.2026	Индивидуальный жилой дом по адресу: «Российская федерация, Московская область, г.о. Домодедово, п. Государственного племенного завода "Константиново", тер. КП "Юсупово Вилладж" участок с када. номером 50:28:0050421:2962»	Стадия	Лист	Листов
Разработал							Р	2	
							 Brick House строительство домов под ключ		
						Ведомость чертежей			

ОБЩИЕ ДАННЫЕ:

1. Проектная документация марки КР разработана в соответствии с:
– Техническим заданием, согласованным с Заказчиком;
– Действующих норм и стандартов.
2. Проектом разработаны архитектурные решения для индивидуального жилого дома по адресу:
«Российская федерация, Московская область,
г. о. Домодедово, п. Государственного племенного завода “Константиново”, тер. КП “Юсупово Вилдж”
участок с кад. номером 50:28:0050421:2962

3. Техничко-экономические показатели:

31. Этажность – 1 этаж
32. Площадь этажа (общая) – 235,06 м²
34. Площадь террас – 35 м²
35. Площадь помещений – 189,76 м²
36. Высота первого этажа – 3,5–4,68 м
37. Площадь застройки – 270 м²

4. Конструкции здания:

- 4.1 Конструкция фундамента:
– Ж/б плита толщиной 300 мм согласно КР-1.

4.2 Конструкции наружных стен:

- Газобетонный блок:
D400 625х400х250h
D500 625х250х250h
D500 625х150х250h.
- Армирование кладки из газобетонных блоков производится в штробе 25х25 мм
предварительно заполненной клеем, двумя стержнями арм-ры ф10A500C каждые 3 ряда блока по
высоте начиная с 1 ряда с отступом от края блока 85 мм.

4.3 Перекрытие 1-го этажа на отм. +3. 300:

- Ж/б плита толщиной 180 мм;

4.5. Конструкция кровли:

- плоская, с утеплением , согласно КР-2.

5. За условную отм. 0.000 принята отметка чистого пола.

6. На планах и ведомостях проемов указаны размеры проемов, ширина полотна двери будет на 100 мм меньше.

При заказе заполнения оконных и дверных проемов следует уточнить габаритные размеры проемов по окончании строительства.

7. Перед началом работ выполнить проекты ИС (инженерные сети водопровода и канализации, отопления и вентиляции и пр.) После разработки проектов ИС при необходимости согласовать с автором проекта места устройства сетей, отверстий, штроб и прочего.

8. Привязки дверных проемов во внутренних стенах, тип и направление открывания уточнить в Дизайн проекте.

Условные обозначения

№ п/п	наименование	сечение	поверхность	примечание
1	ЭППС			
2	Железобетон			
3	Газобетон			

АРМИРОВАНИЕ КОНСТРУКЦИЙ:

1. Армирование монолитных конструкций из отдельных стержней исходя из максимальной длины стержня.
Марка арматурной стали:
– А240 – ст3кп по ГОСТ 5781–82*
– А500С– 3ПС – ГОСТ 380–2005.
При необходимости стыковку стержней производить нахлесткой. Длина нахлестки стержней не менее 50d.

2. Арматура не должна иметь механических повреждений или пластических деформаций ухудшающих сцепление с бетоном, загрязнения и коррозионные поражения.


3. Все изготавливаемые арматурные изделия должны отвечать требованиям ГОСТ 10922–2012 и ГОСТ 14098–91.

4. Все сопряжения арматуры выполнять вязальной проволокой 1,2 – 0 – 4 по ГОСТ 3282–74 с шагом через 2 стержня в шахматном порядке.

Согласовано			
Взам. инв. №			
Подпись и дата			
Инв. № подл.			

						Проект жилого дома					
Изм.	Кол. уч.	Лист	№ док.	Подпись	Дата	Индивидуальный жилой дом по адресу: «Российская федерация, Московская область, г. о. Домодедово, п. Государственного племенного завода "Константиново", тер. КП "Юсупово Вилдж" участок с кад. номером 50:28:0050421:2962»			Стадия	Лист	Листов
ГАП		Филатов А.Г.			11.06.2026				Р	3	
Разработал									 Brick House строительство домов под ключ		
						Пояснительная записка					


Схема планировочной организации земельного участка

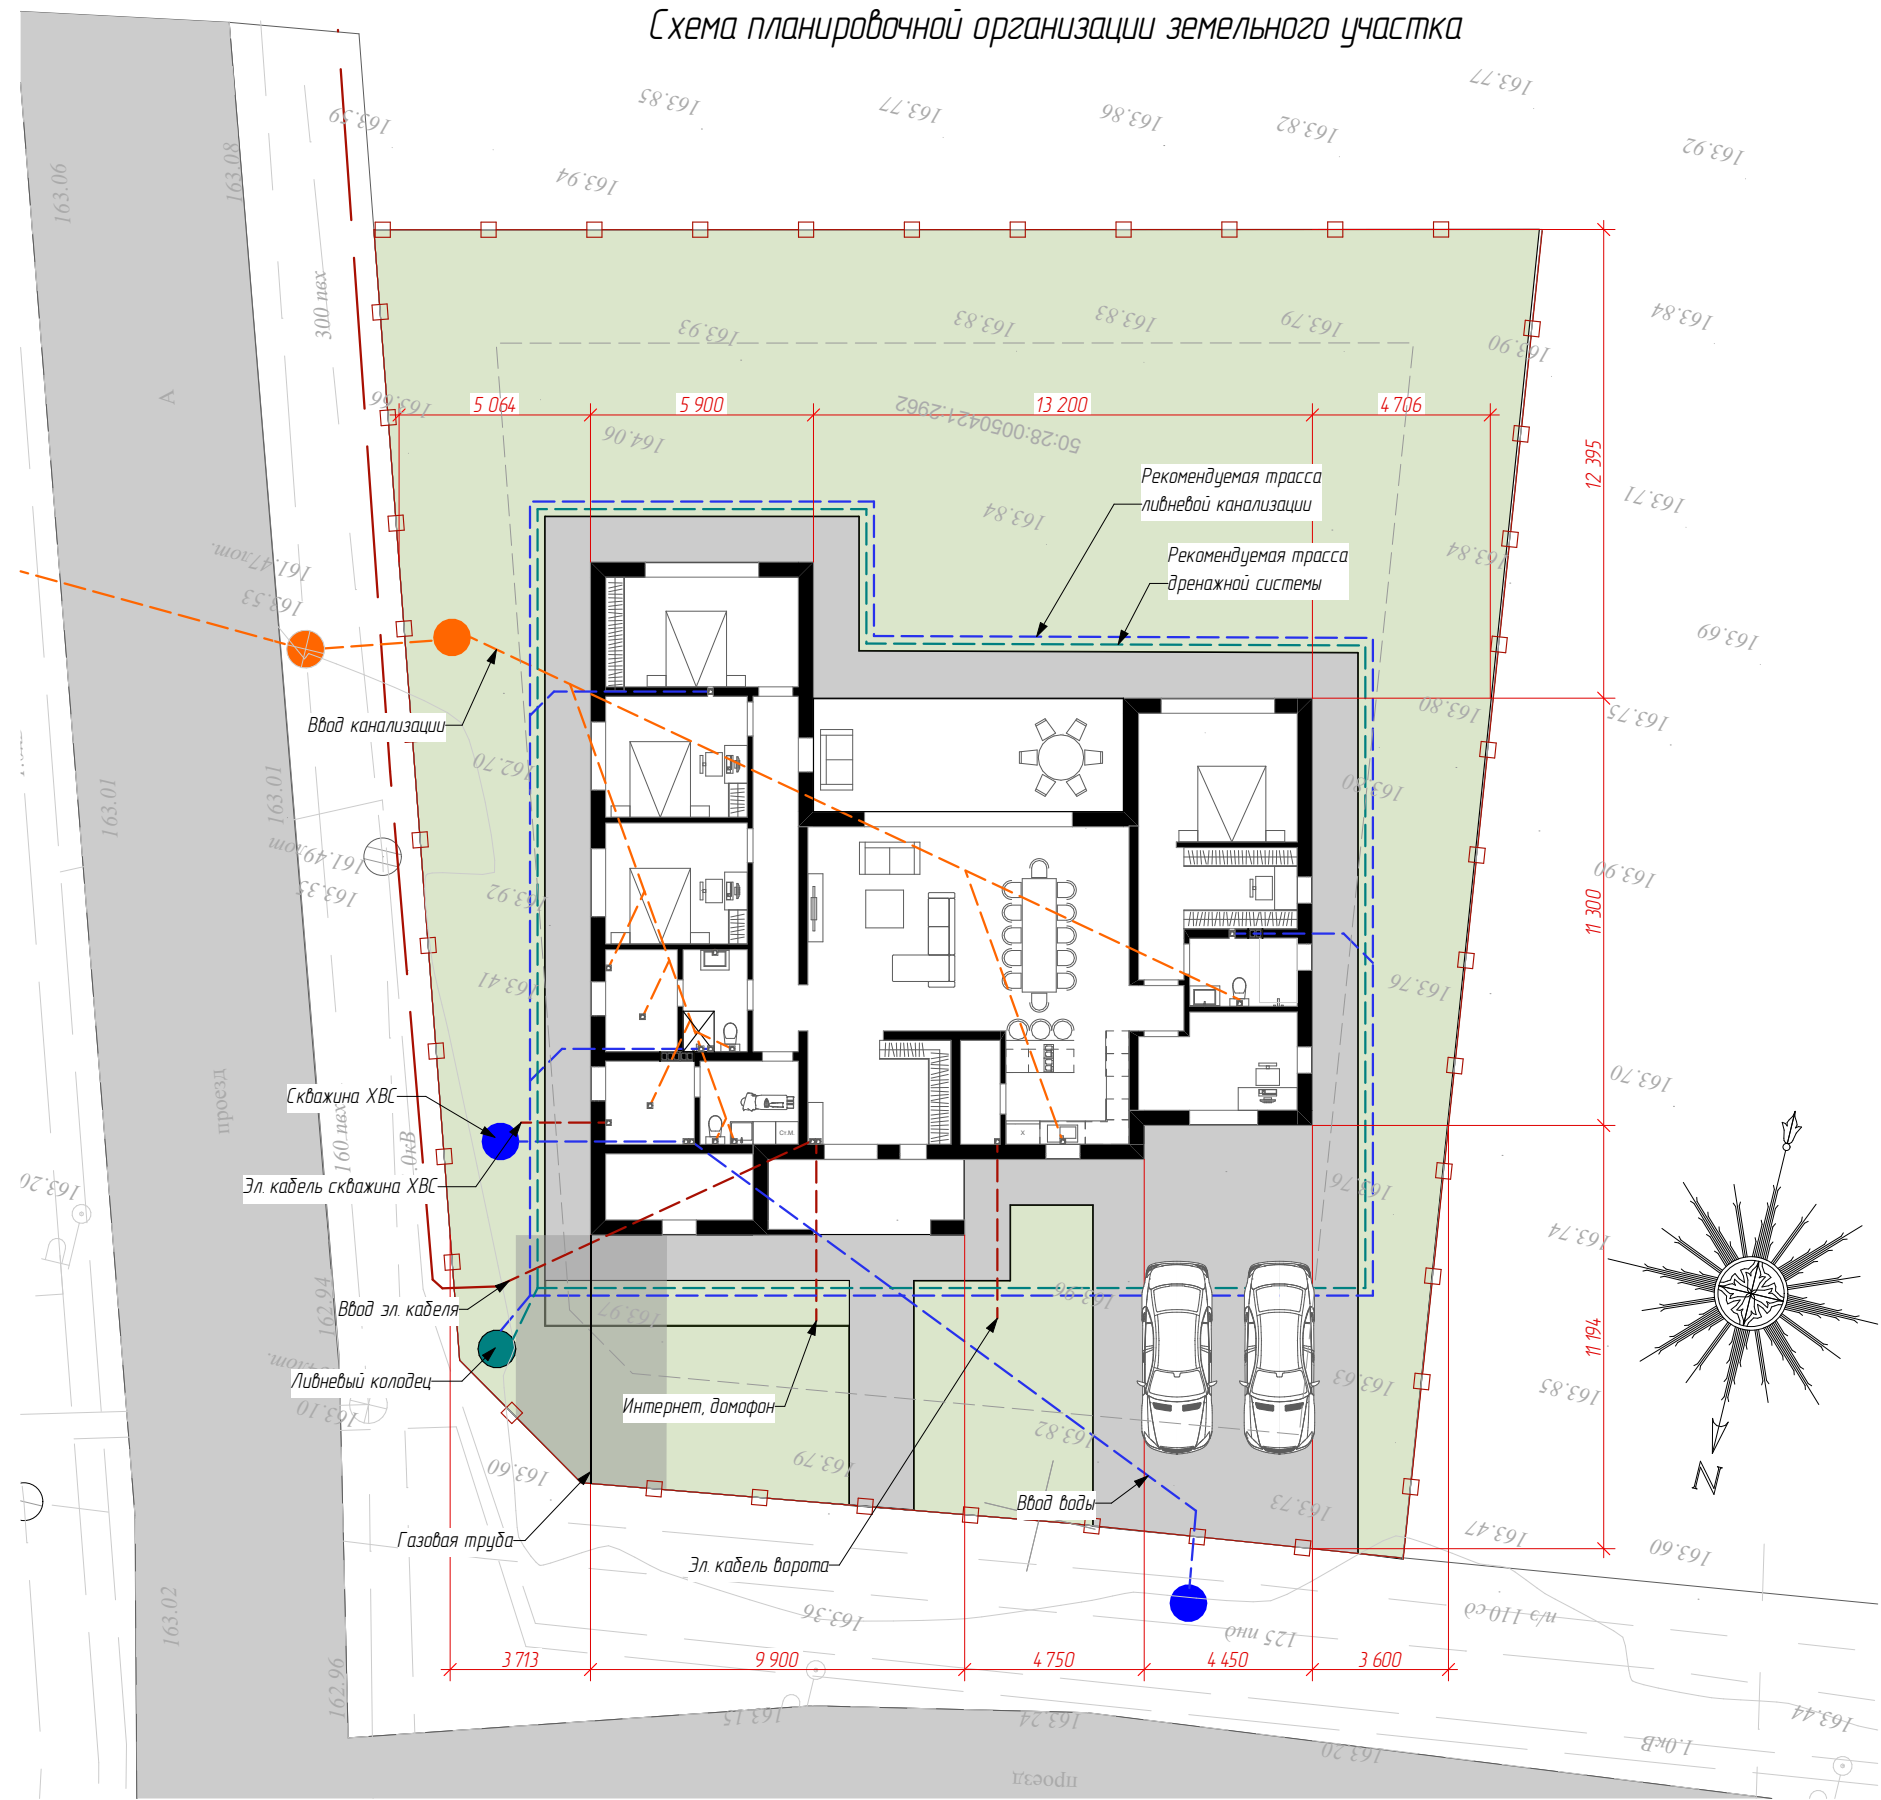

Согласовано					
Взам. инв. №					
Подпись и дата					
Инв. № подл.					

						Проект жилого дома			
Изм.	Кол.уч.	Лист	№ док.	Подпись	Дата	Индивидуальный жилой дом по адресу: «Российская федерация, Московская область, г. о. Домодедово, п. Государственного племенного завода "Константиново", тер. КП "Юсупово Вилладж" участок с кад. номером 50:28:0050421:2962»	Стадия	Лист	Листов
ГАП		Филатов А.Г.			10.06.2026		Р	4	
Разработал									
						Схема планировочной организации земельного участка	 Brick House строительство домов под ключ		

План этажа на отм. + 0.000

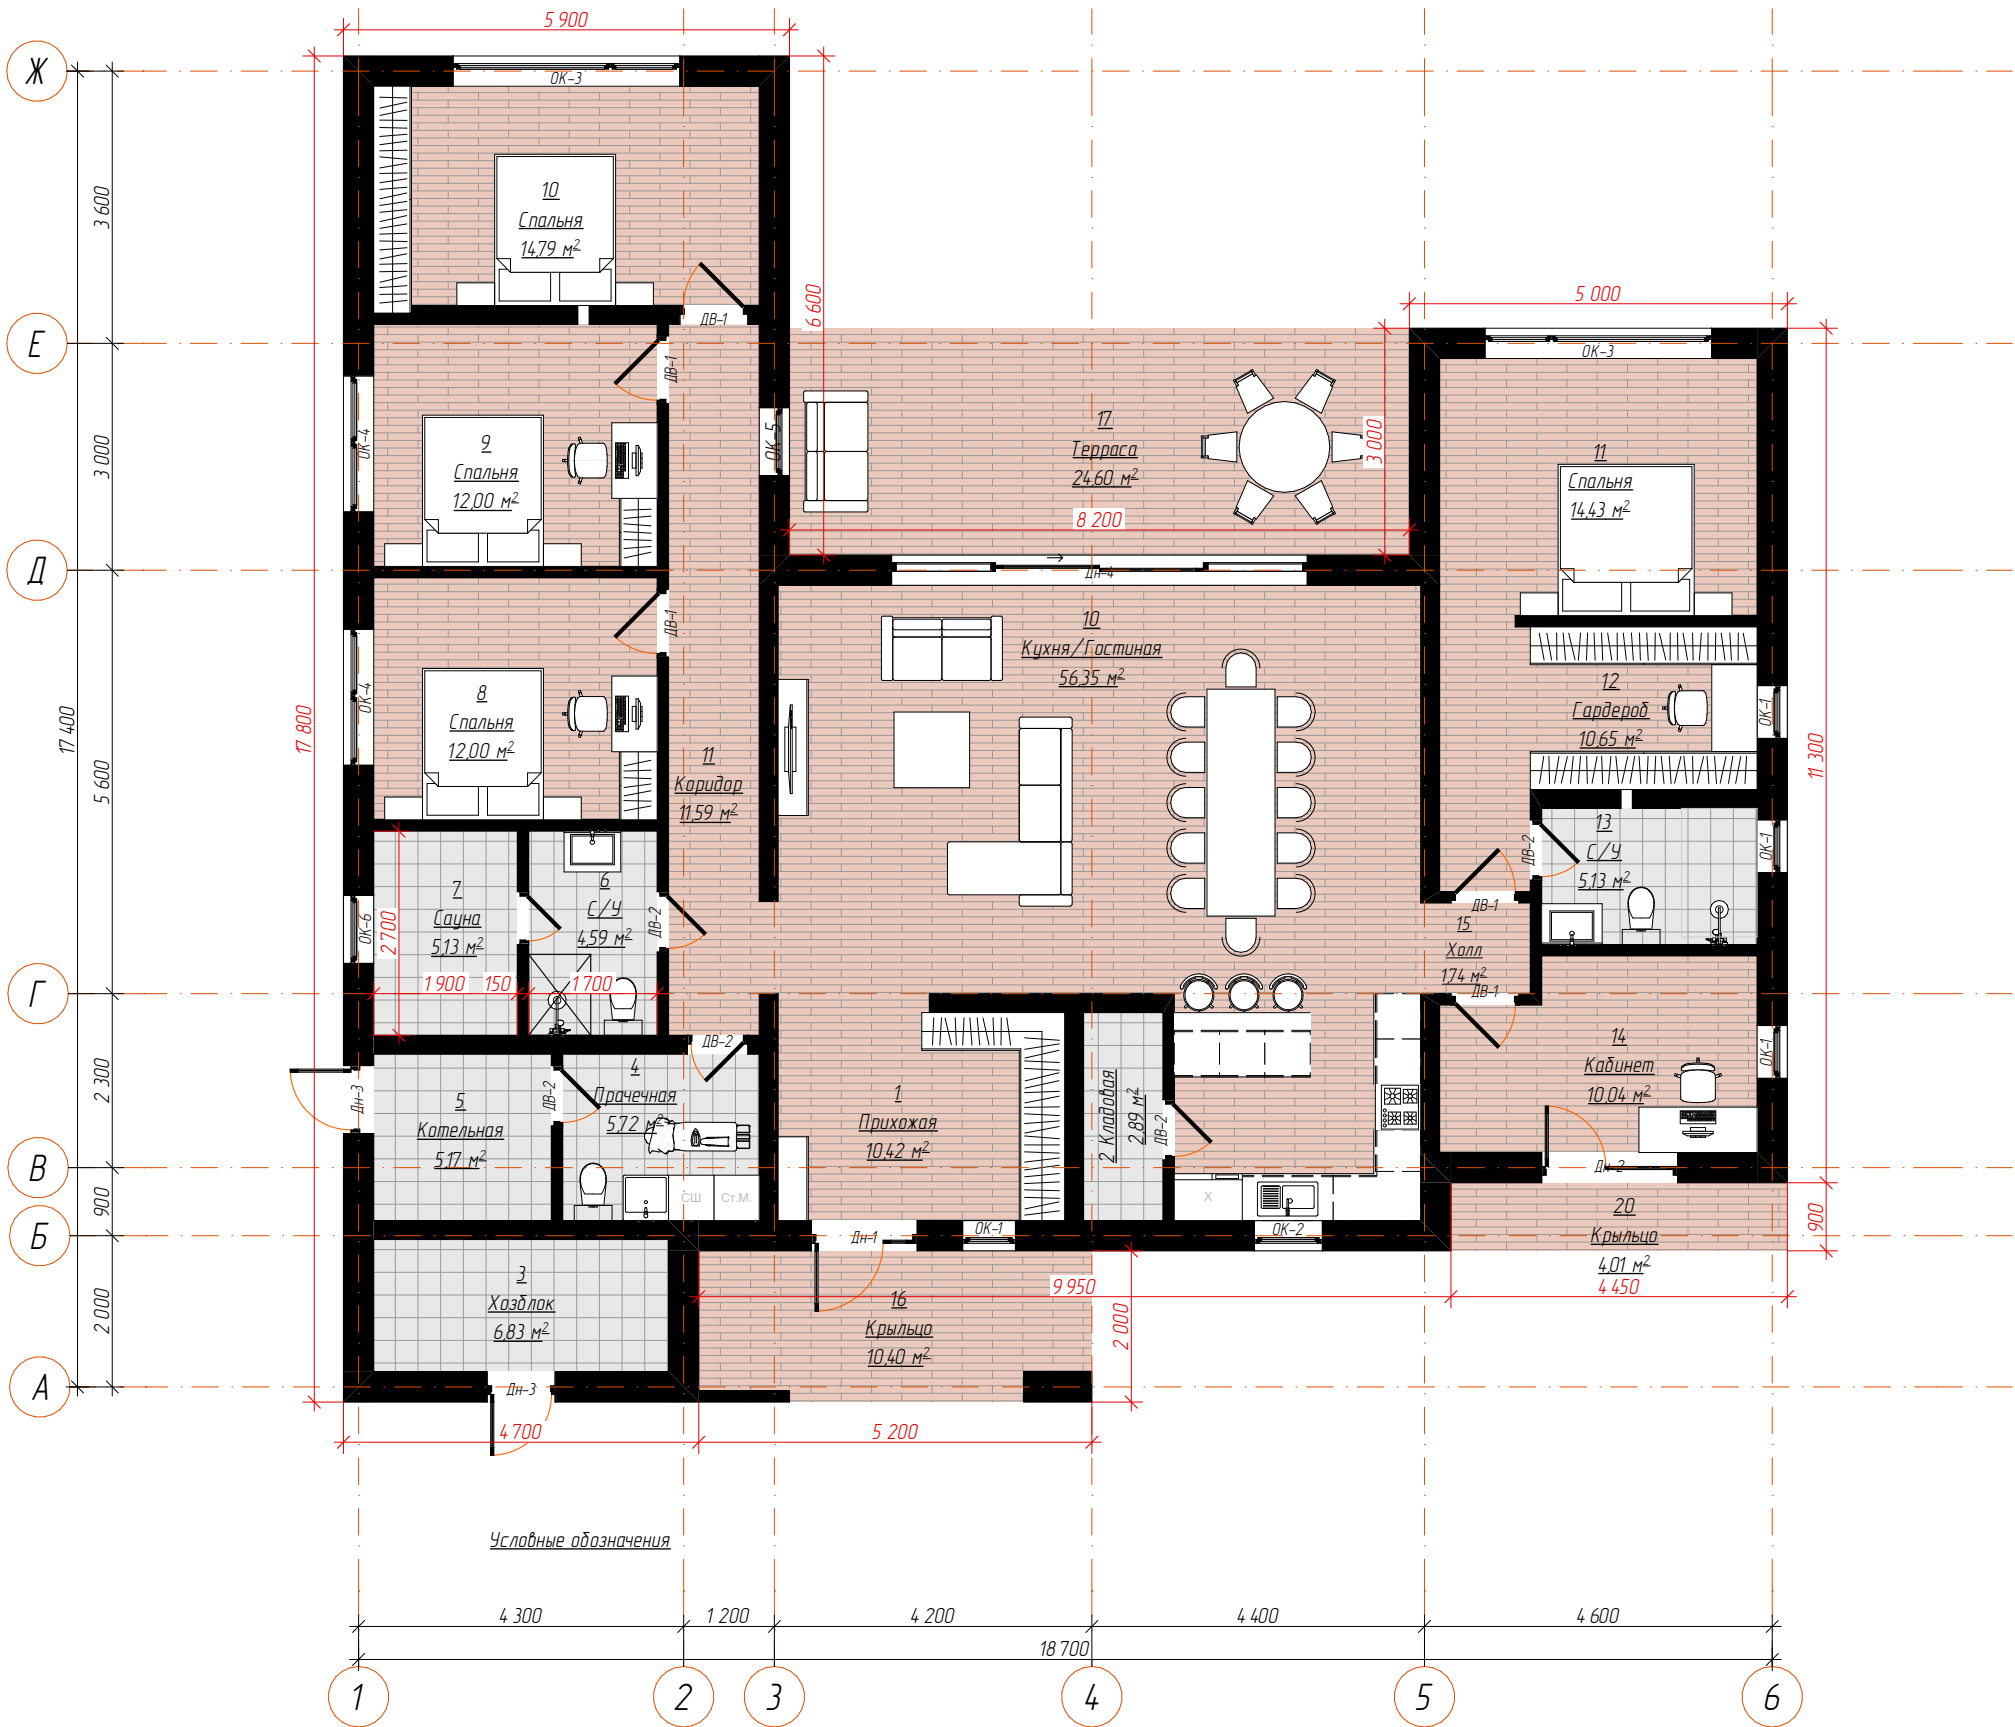

Экспликация помещений 1-й этаж		
№	Наименование	Площадь
1	Прихожая	10,42
2	2 Кладовая	2,89
3	Хозблок	6,83
4	Прачечная	5,72
5	Котельная	5,17
6	С/У	4,59
7	Сауна	5,13
8	Спальня	12,00
9	Спальня	12,00
10	Кухня/Гостиная	56,35
10	Спальня	14,79
11	Коридор	11,59
11	Спальня	14,43
12	Гардероб	10,65
13	С/У	5,13
14	Кабинет	10,04
15	Холл	1,74
		189,47 м²

Согласовано

Взам. инв. №

Подпись и дата

Инв. № подл.

Проект жилого дома

Изм.	Кол. уч.	Лист	№ док.	Подпись	Дата
ГАП		Филатов А.Г.			10.06.2026
Разработал					

Индивидуальный жилой дом по адресу:
«Российская федерация, Московская область,
г. о. Домодедово, п. Государственного племенного завода
"Константиново", тер. КП "Осупово Вилладж"
участок с кадастровым номером 50:28:0050421:2962»

Стадия

Р

Лист

5


Листов



План этажа на отм. + 0.000

Формат А3

Схема расположения отсечной гидроизоляции

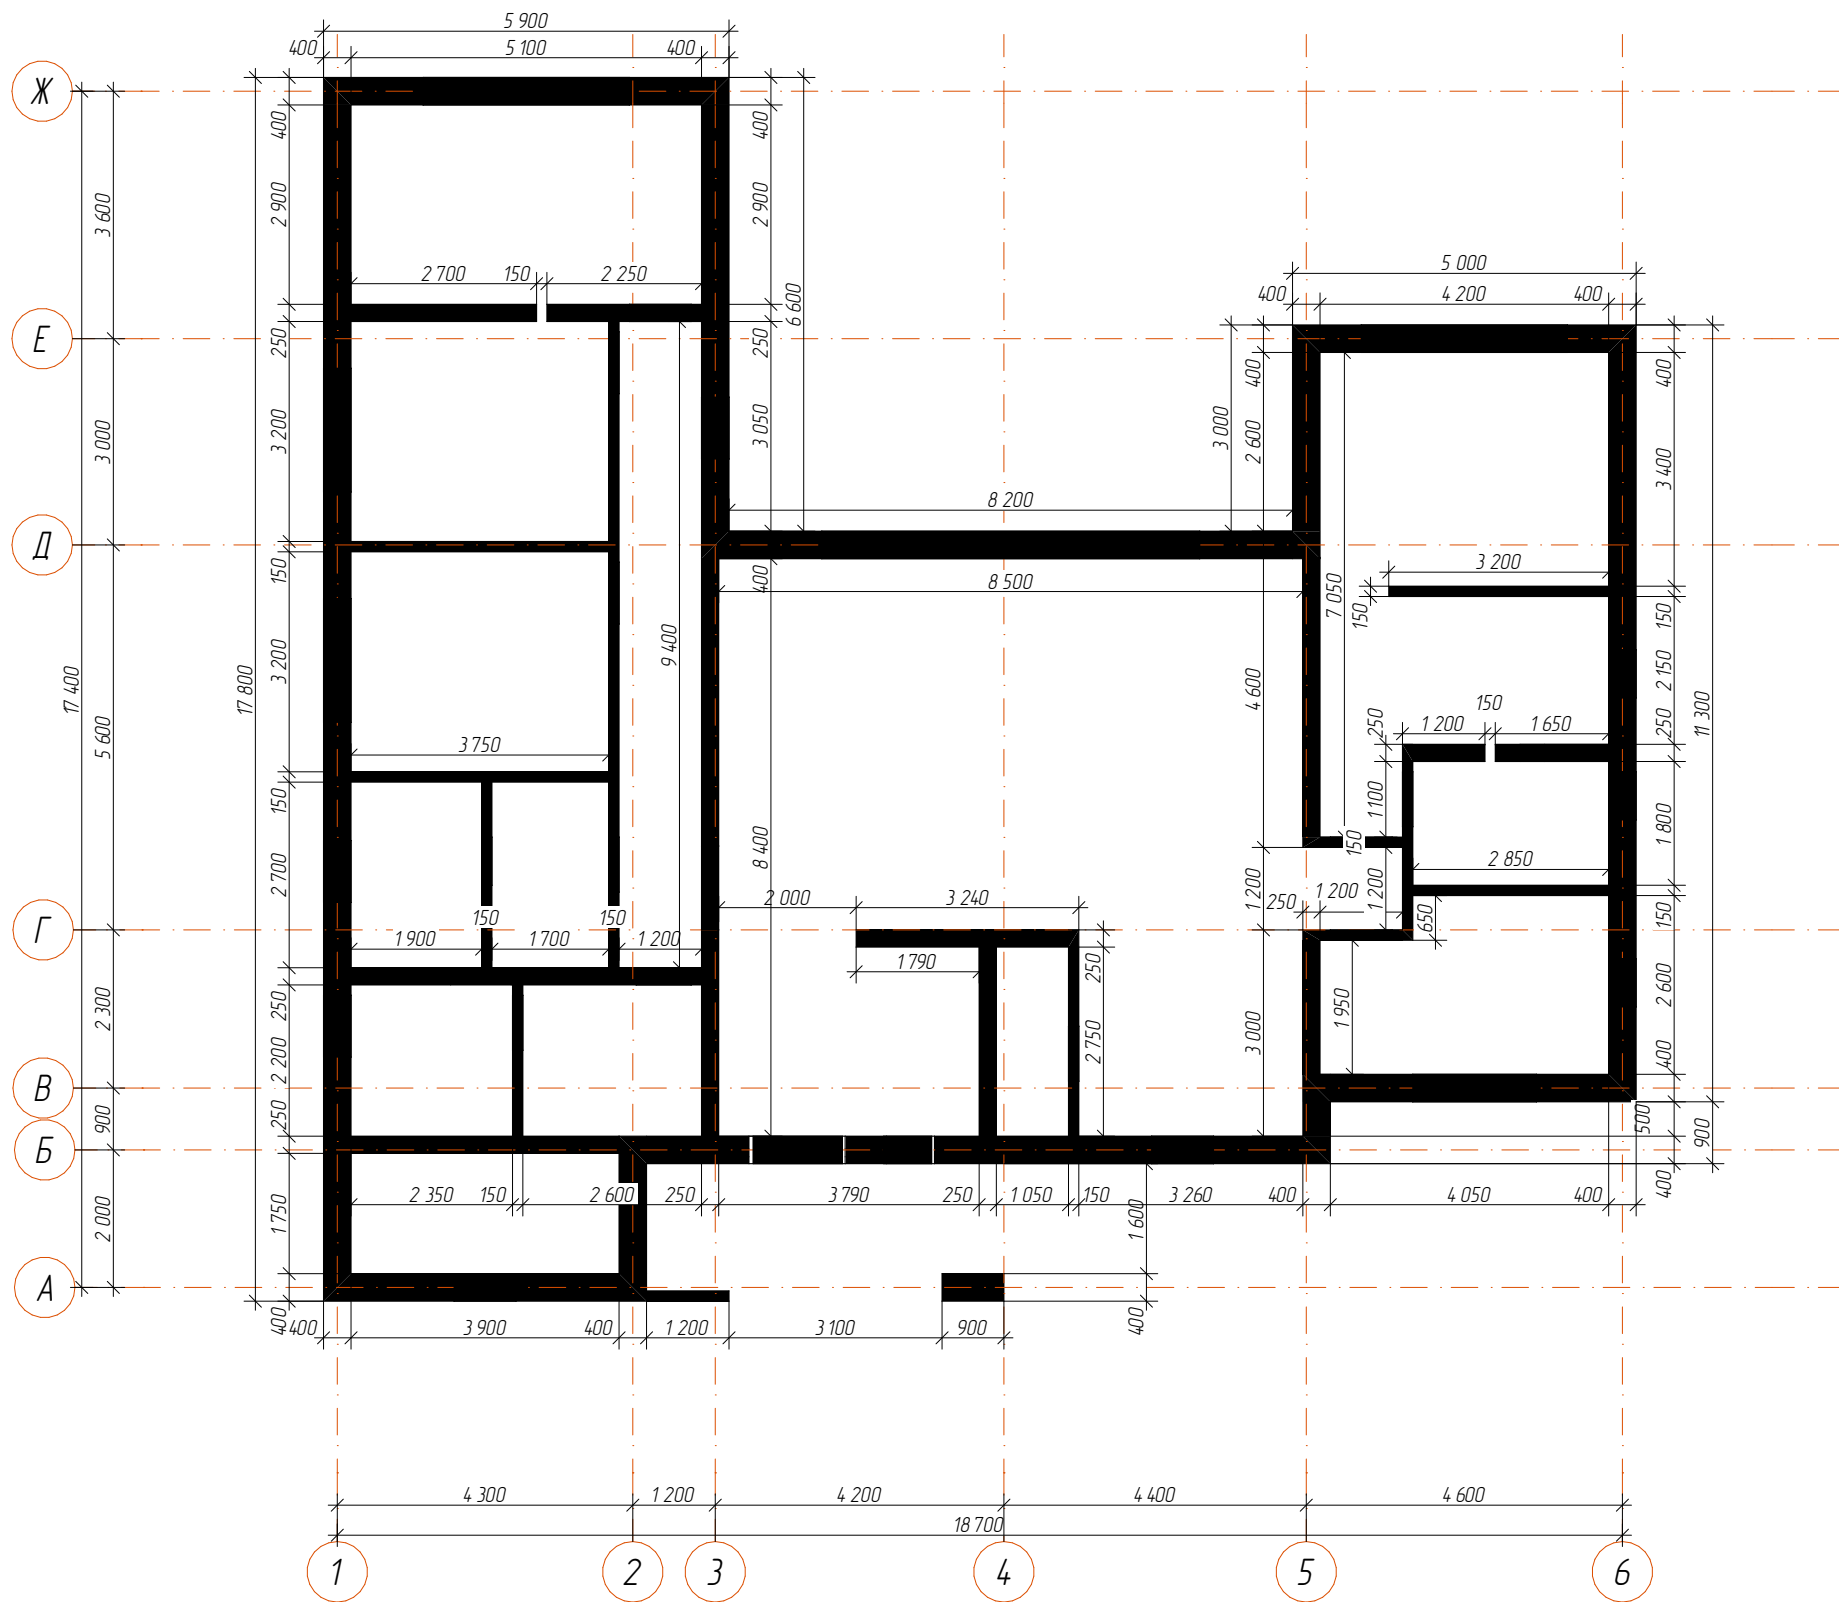

Спецификация гидроизоляционных материалов

Поз.	Обозначение	Наименование	Кол-во	Масса ед. шт.	Примечание
	СТО 72746455-3123-2017	Гидроизоляция отсечная, битумсодержащая типа ТЕХНОНИКОЛЬ master (несущие стены)	39,555		м²
	СТО 72746455-3123-2017	Гидроизоляция отсечная, битумсодержащая типа ТЕХНОНИКОЛЬ master (перегородки)	5,04		м²

						Проект жилого дома			
Изм.	Кол.уч.	Лист	№ док.	Подпись	Дата	Индивидуальный жилой дом по адресу: «Российская федерация, Московская область, г. о. Домодедово, п. Государственного племенного завода "Константиново", тер. КП "Юсупово Вилладж" участок с кад. номером 50:28:0050421:2962»	Стадия	Лист	Листов
ГАП		Филатов А.Г.			10.06.2026		Р	6	
Разработал							 Brick House строительство домов под ключ		
						Схема расположения отсечной гидроизоляции			



Согласовано			
Взам. инв. №			
Подпись и дата			
Инв. № подл.			

						Проект жилого дома			
Изм.	Кол.уч.	Лист	№ док.	Подпись	Дата	Индивидуальный жилой дом по адресу: «Российская федерация, Московская область, г. о. Домодедово, п. Государственного племенного завода "Константиново", тер. КП "Юсупово Вилладж" участок с кад. номером 50:28:0050421:2962»	Стадия	Лист	Листов
ГАП		Филатов А.Г.			11.06.2026		Р	7	
Разработал									
3D вид 1						 Brick House строительство домов под ключ			



Согласовано				
Взам. инв. №				
Подпись и дата				
Инв. № подл.				

						Проект жилого дома			
Изм.	Кол. уч.	Лист	№ док.	Подпись	Дата	Индивидуальный жилой дом по адресу: «Российская федерация, Московская область, г. о. Домодедово, п. Государственного племенного завода "Константиново", тер. КП "Осупово Вилладж" участок с кад. номером 50:28:0050421:2962»	Стадия	Лист	Листов
ГАП		Филатов А.Г.			10.06.2026		Р	8	
Разработал									
						3D вид 2	 Brick House строительство домов под ключ		



Согласовано	

Взам. инв. №	
Подпись и дата	
Инв. № подл.	

						Проект жилого дома				
Изм.	Кол.уч.	Лист	№ док.	Подпись	Дата					
ГАП		Филатов А.Г.			11.06.2026	Индивидуальный жилой дом по адресу: «Российская федерация, Московская область, г. о. Домодедово, п. Государственного племенного завода "Константиново", тер. КП "Юсупово Вилладж" участок с кад. номером 50:28:0050421:2962»		Стадия	Лист	Листов
Разработал								Р	9	
								 Brick House строительство домов под ключ		
						3D вид 3				



Согласовано			
Взам. инв. №			
Подпись и дата			
Инв. № подл.			

						Проект жилого дома				
Изм.	Кол.уч.	Лист	№ док.	Подпись	Дата					
ГАП		Филатов А.Г.			11.06.2026	Индивидуальный жилой дом по адресу: «Российская федерация, Московская область, г. о. Домодедово, п. Государственного племенного завода "Константиново", тер. КП "Осупово Вилладж" участок с када. номером 50:28:0050421:2962»		Стадия	Лист	Листов
Разработал					Р			10		
3D вид 4						 Brick House строительство домов под ключ				


Разрез 1-1



Примечание : Материалы по кровле допускается заменять аналогами со схожими характеристиками

						Проект жилого дома				
Изм.	Кол.уч.	Лист	№ док.	Подпись	Дата					
ГАП		Филатов А.Г.			11.06.2026	Индивидуальный жилой дом по адресу: «Российская федерация, Московская область, г. о. Домодедово, п. Государственного племенного завода "Константиново", тер. КП "Осупово Вилладж" участок с кад. номером 50:28:0050421:2962»		Стадия	Лист	Листов
Разработал								Р	11	
								 Brick House строительство домов под ключ		
						Разрез 1-1				

Разрез 2-2

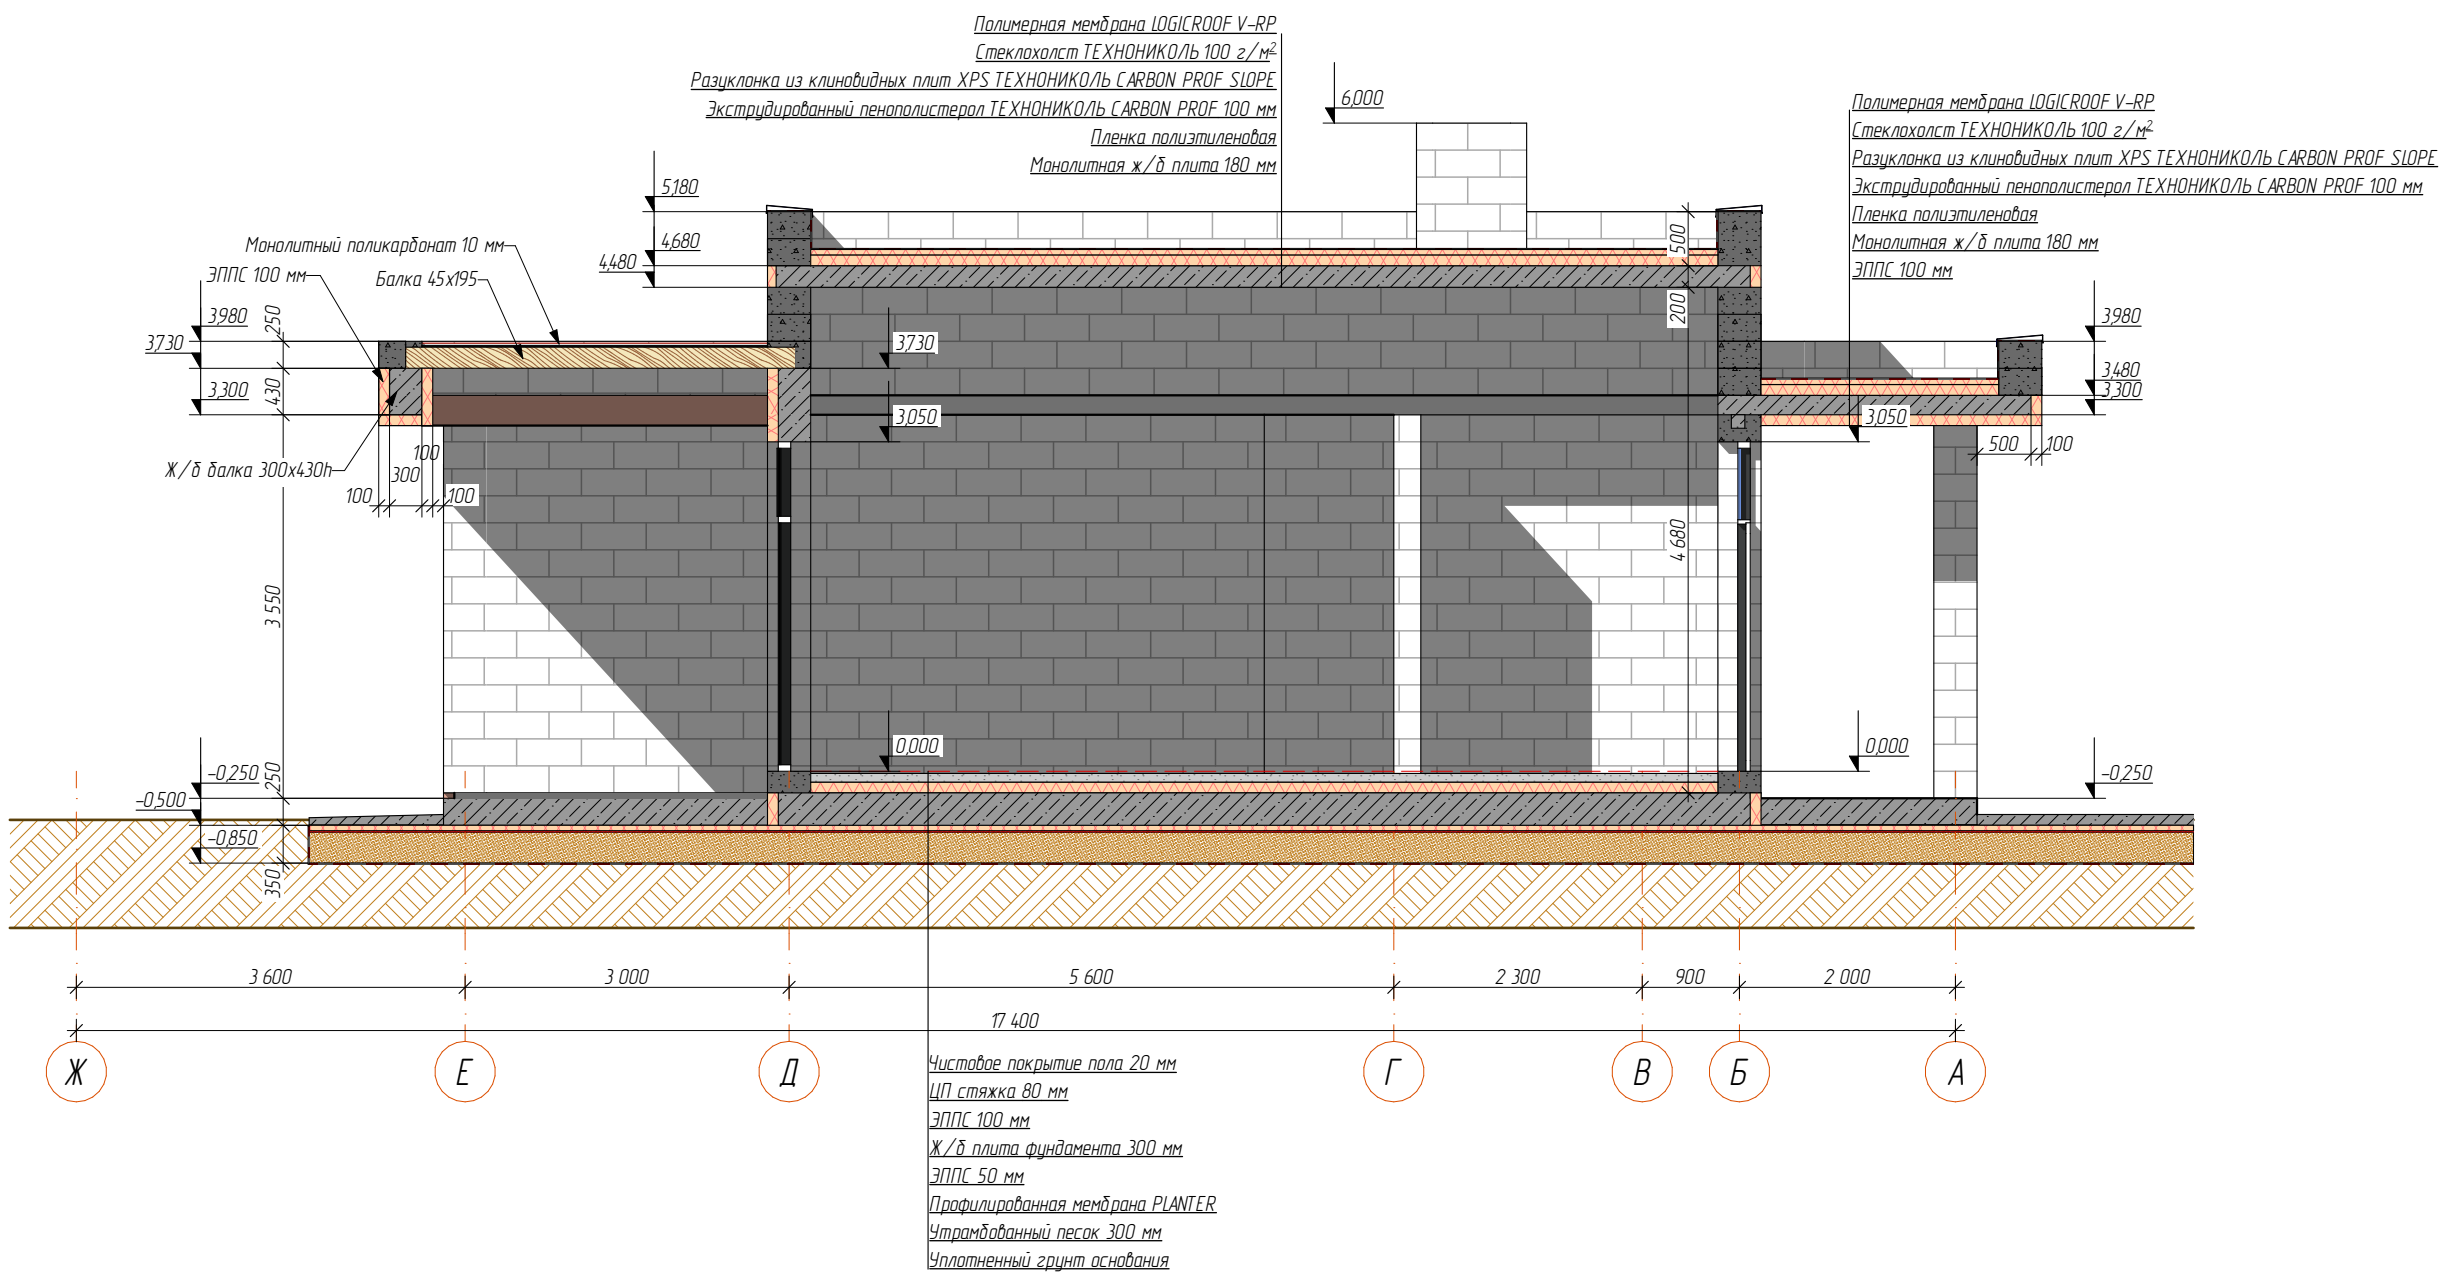

Примечание : Материалы по кровле допускается заменять аналогами со схожими характеристиками

						Проект жилого дома				
Изм.	Кол.уч.	Лист	№ док.	Подпись	Дата					
ГАП		Филатов А.Г.			10.06.2026	Индивидуальный жилой дом по адресу: «Российская федерация, Московская область, г.о. Домодедово, п. Государственного племенного завода "Константиново", тер. КП "Юсупово Вилладж" участок с кад. номером 50:28:0050421:2962»		Стадия	Лист	Листов
Разработал								Р	12	
								 Brick House строительство домов под ключ		
						Разрез 2-2				


Согласовано				
Взам. инв. №				
Подпись и дата				
Инв. № подл.				




						Проект жилого дома				
Изм.	Кол.уч.	Лист	№ док.	Подпись	Дата					
ГАП		Филатов А.Г.			10.06.2026	Индивидуальный жилой дом по адресу: «Российская федерация, Московская область, г. о. Домодедово, п. Государственного племенного завода "Константиново", тер. КП "Юсупово Вилладж" участок с кад. номером 50:28:0050421:2962»		Стадия	Лист	Листов
Разработал								Р	13	
								 Brick House строительство домов под ключ		
						Кладочный план на отм. + 0. 000				

Узлы армирования кладки


Узел 1. Армирование угла
кладки

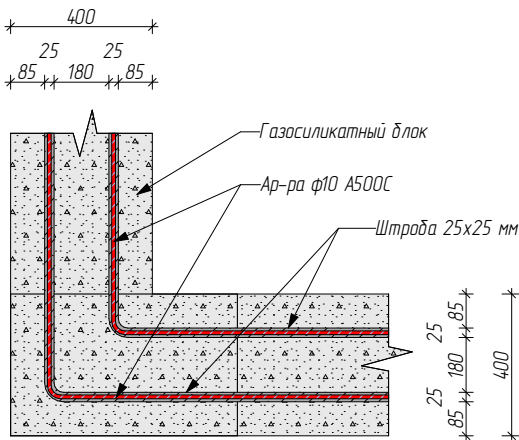


Узел 2. Армирование кладки
блоков 250 мм

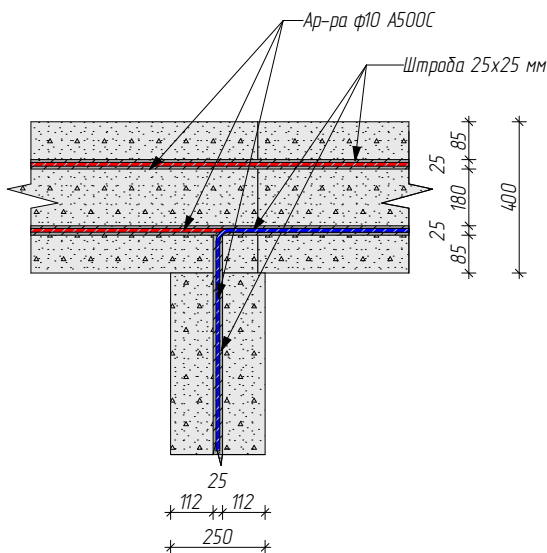

Узел порога панорамных окон

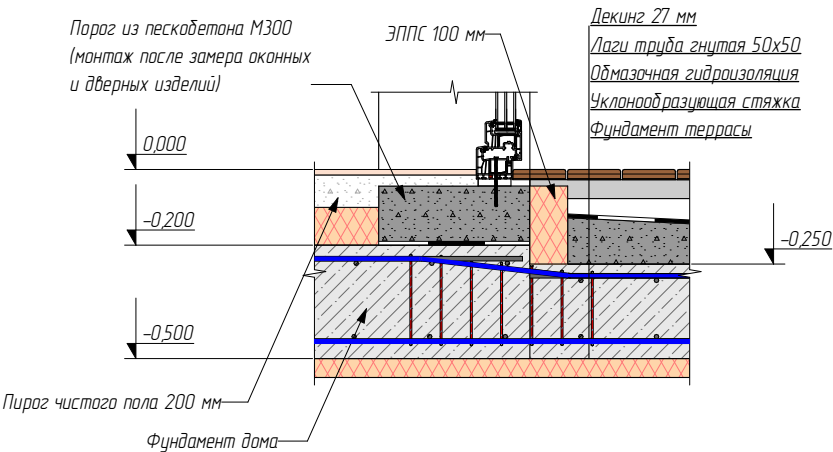

Узел 3. Примыкание перегородки

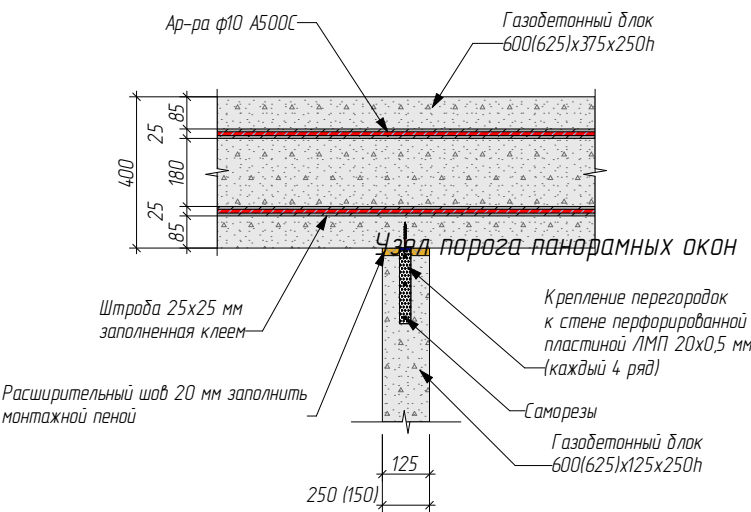

Согласовано

Взам. инв. №

Подпись и дата

Инв. № подл.

						Проект жилого дома			
Изм.	Кол. уч.	Лист	№ док.	Подпись	Дата				
ГАП		Филатов А.Г.			10.06.2026	Стадия		Лист	Листов
Разработал						Р		14	
						 Brick House строительство домов под ключ			
						Узлы армирования кладки			

Спецификация по газобетонным блокам

Поз.	Обозначение	Наименование	Кол-во	Масса ед. шт.	Примечание
		Газобетонный блок 600х400х250	7895		м³
		Газобетонный блок 600х250х250	30,4		м³
	ГОСТ 34028-2016	φ10 A500С (армирование кладки)	1235	0,617	м/п

Спецификация перегородок 1-го этажа

Поз.	Обозначение	Наименование	Кол-во	Масса ед. шт.	Примечание
		Газобетонный блок 600х150х250	16,81		м³
	ГОСТ 34028-2016	φ10 A500С (армирование кладки)	189	0,617	м/п

Спецификация несущих стен 2-го этажа

Поз.	Обозначение	Наименование	Кол-во	Масса ед. шт.	Примечание
		Газобетонный блок 600х400х250	1344		м³
	ГОСТ 34028-2016	φ10 A500С (армирование кладки)	152	0,617	м/п

Спецификация парапетов кровли

Поз.	Обозначение	Наименование	Кол-во	Масса ед. шт.	Примечание
		Газобетонный блок 600х400х250	2274		м³
	ГОСТ 34028-2016	φ10 A500С (армирование кладки)	258	0,617	м/п

Согласовано

Взам. инв. №

Подпись и дата

Инв. № подл.

Изм.

Кол. уч.

Лист

№ док.

Подпись

Дата

ГАП

Филатов А.Г.

11.06.2026

Разработал

Проект жилого дома

Индивидуальный жилой дом по адресу:
«Российская федерация, Московская область,
г. о. Домодедово, п. Государственного племенного завода
"Константиново", тер. КП "Осупово Вилладж"
участок с када. номером 50:28:0050421:2962»

Стадия

Р

Лист

15

Листов





Спецификация по газобетонным блокам

Brick House



строительство домов под ключ

Формат А3

План перемычек 1-го этажа

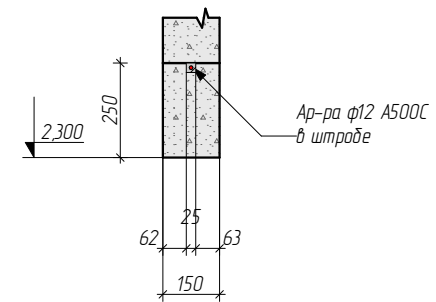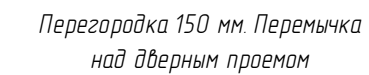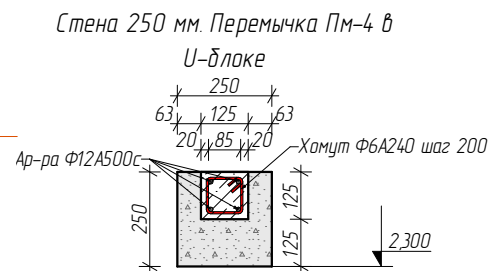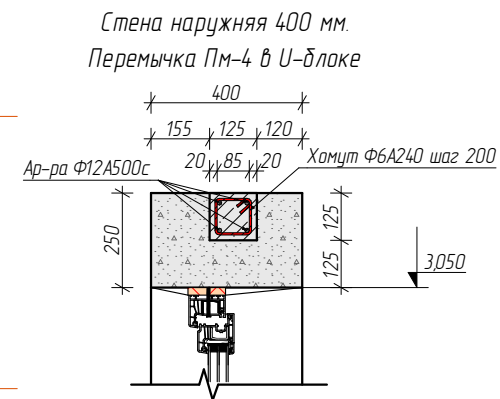


Спецификация перемычек 1-20 этажа

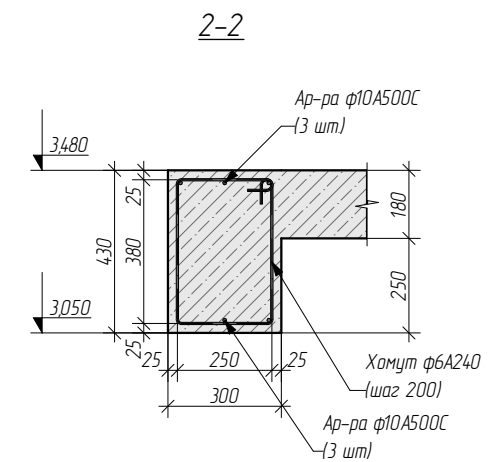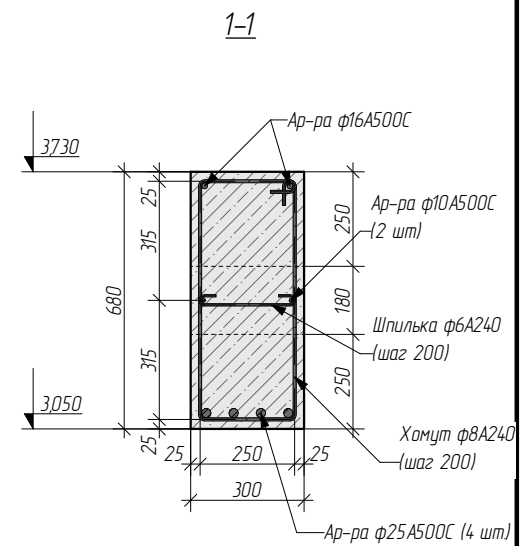

Поз.	Обозначение	Наименование	Кол-во	Масса ед. шт.	Примечание
	ГОСТ 26633-2015	Бетон В-22,5	0,24		м³
	ГОСТ 34028-2016	φ12 А500С	103		кг
	ГОСТ 34028-2016	φ6 А240 (хомуты)	204		кг
		Длина перемычек в U-блоках	215		м/п

						Проект жилого дома		
Изм.	Кол. ун.	Лист	№ док.	Подпись	Дата			
ГАП		Филатов А. Г.		10.06.2026		Индивидуальный жилой дом по адресу: «Российская федерация, Московская область, г. о. Домодедово, п. Государственного племенного завода "Константиново", тер. КП "Юсупово Виллаж" участок с када. номером 50:28:0050421:2962»		
Разработал								
План перемычек 1-го этажа						Стация	Лист	Листов
						Р	16	
						 Brick House строительство домов под ключ		


Схема фасада 1

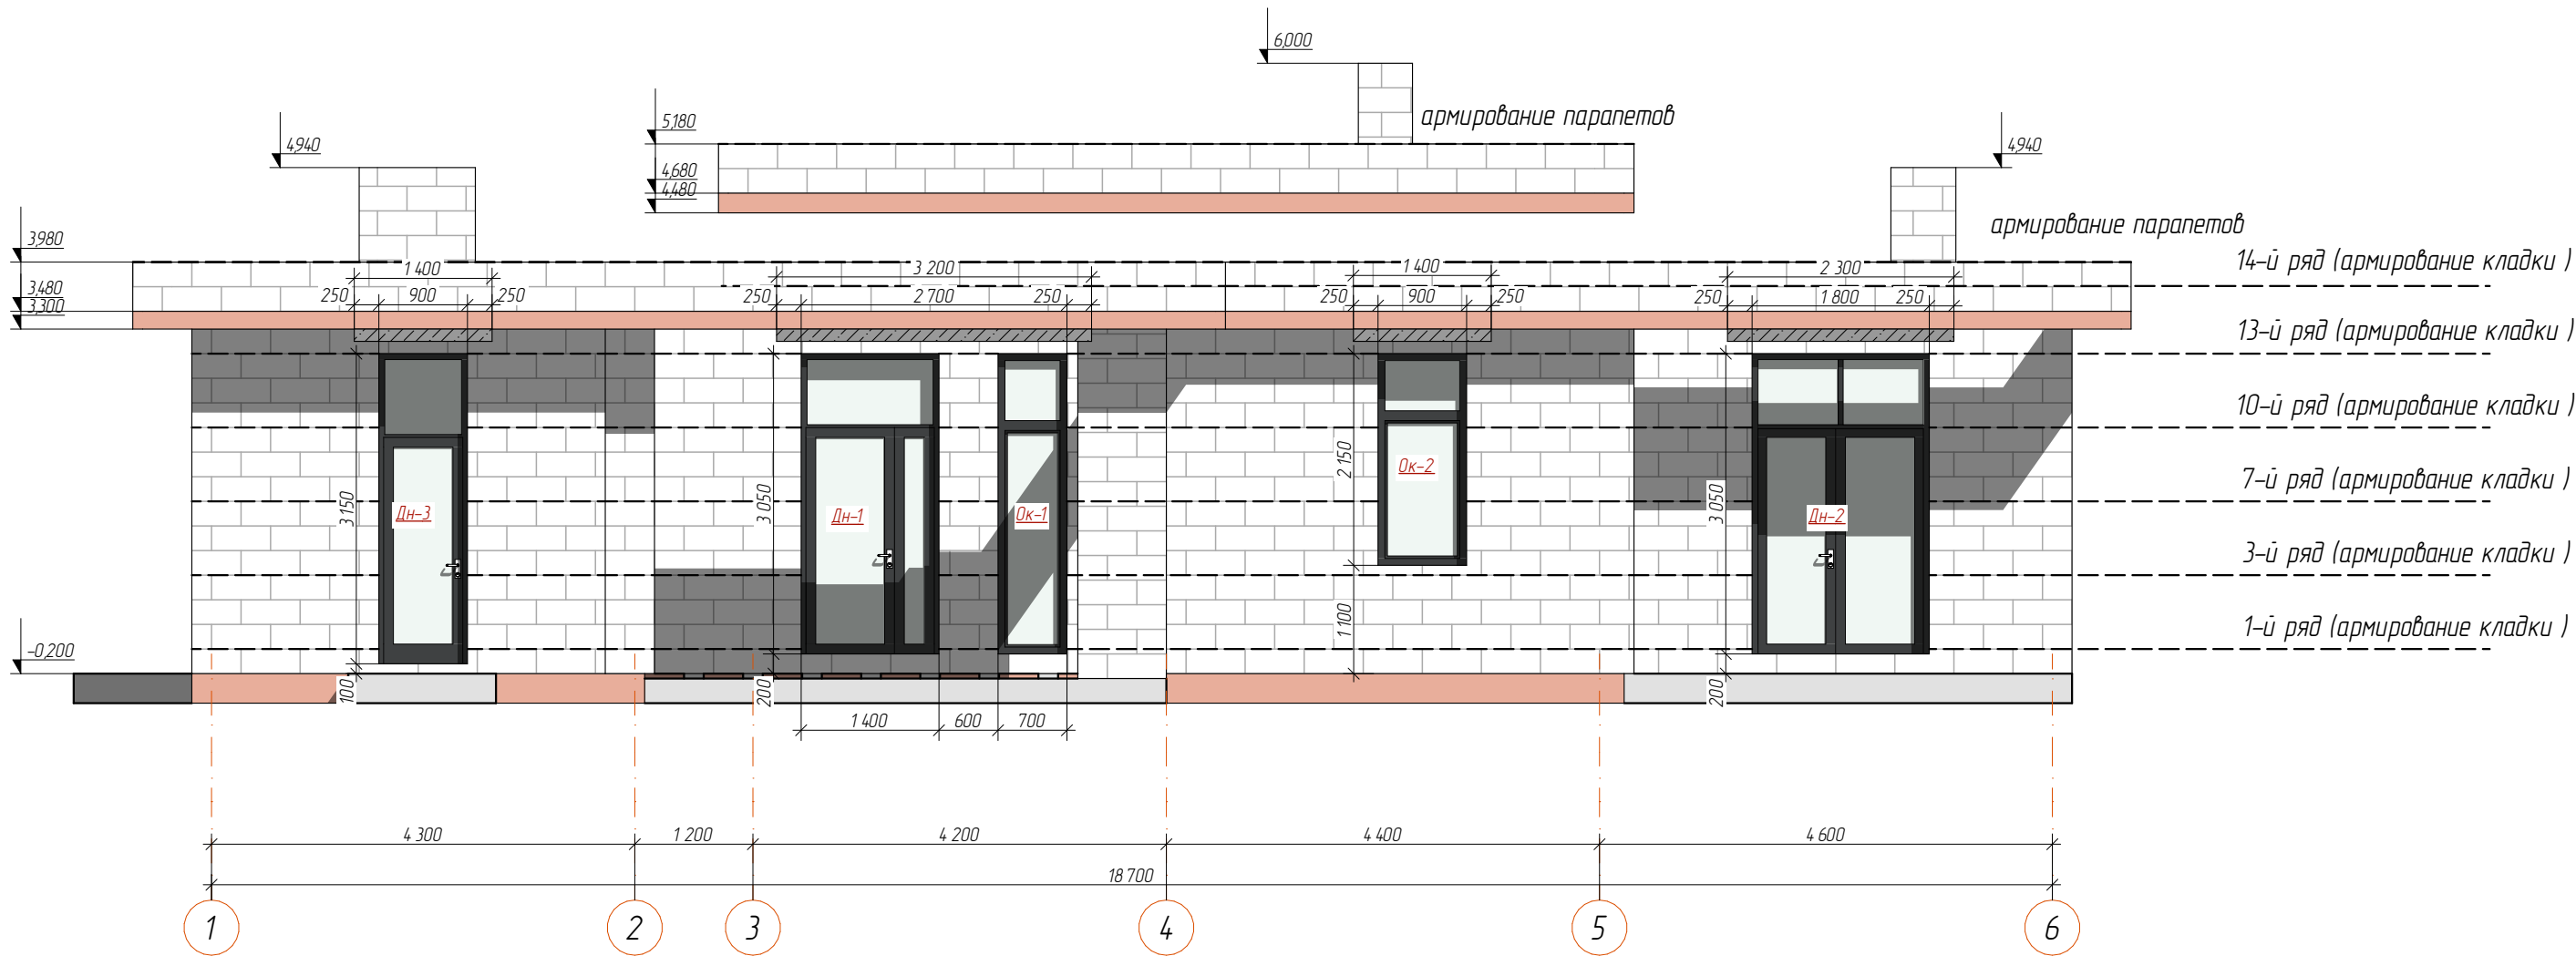

Согласовано				
Взам. инв. №				
Подпись и дата				
Инв. № подл.				

						Проект жилого дома				
Изм.	Кол.уч.	Лист	№ док.	Подпись	Дата					
ГАП		Филатов А.Г.			10.06.2026	Индивидуальный жилой дом по адресу: «Российская федерация, Московская область, г. о. Домодедово, п. Государственного племенного завода "Константиново", тер. КП "Осупово Вилладж" участок с када. номером 50:28:0050421:2962»		Стадия	Лист	Листов
Разработал								Р	17	
						Схема фасада 1		 Brick House строительство домов под ключ		


Схема фасада 2

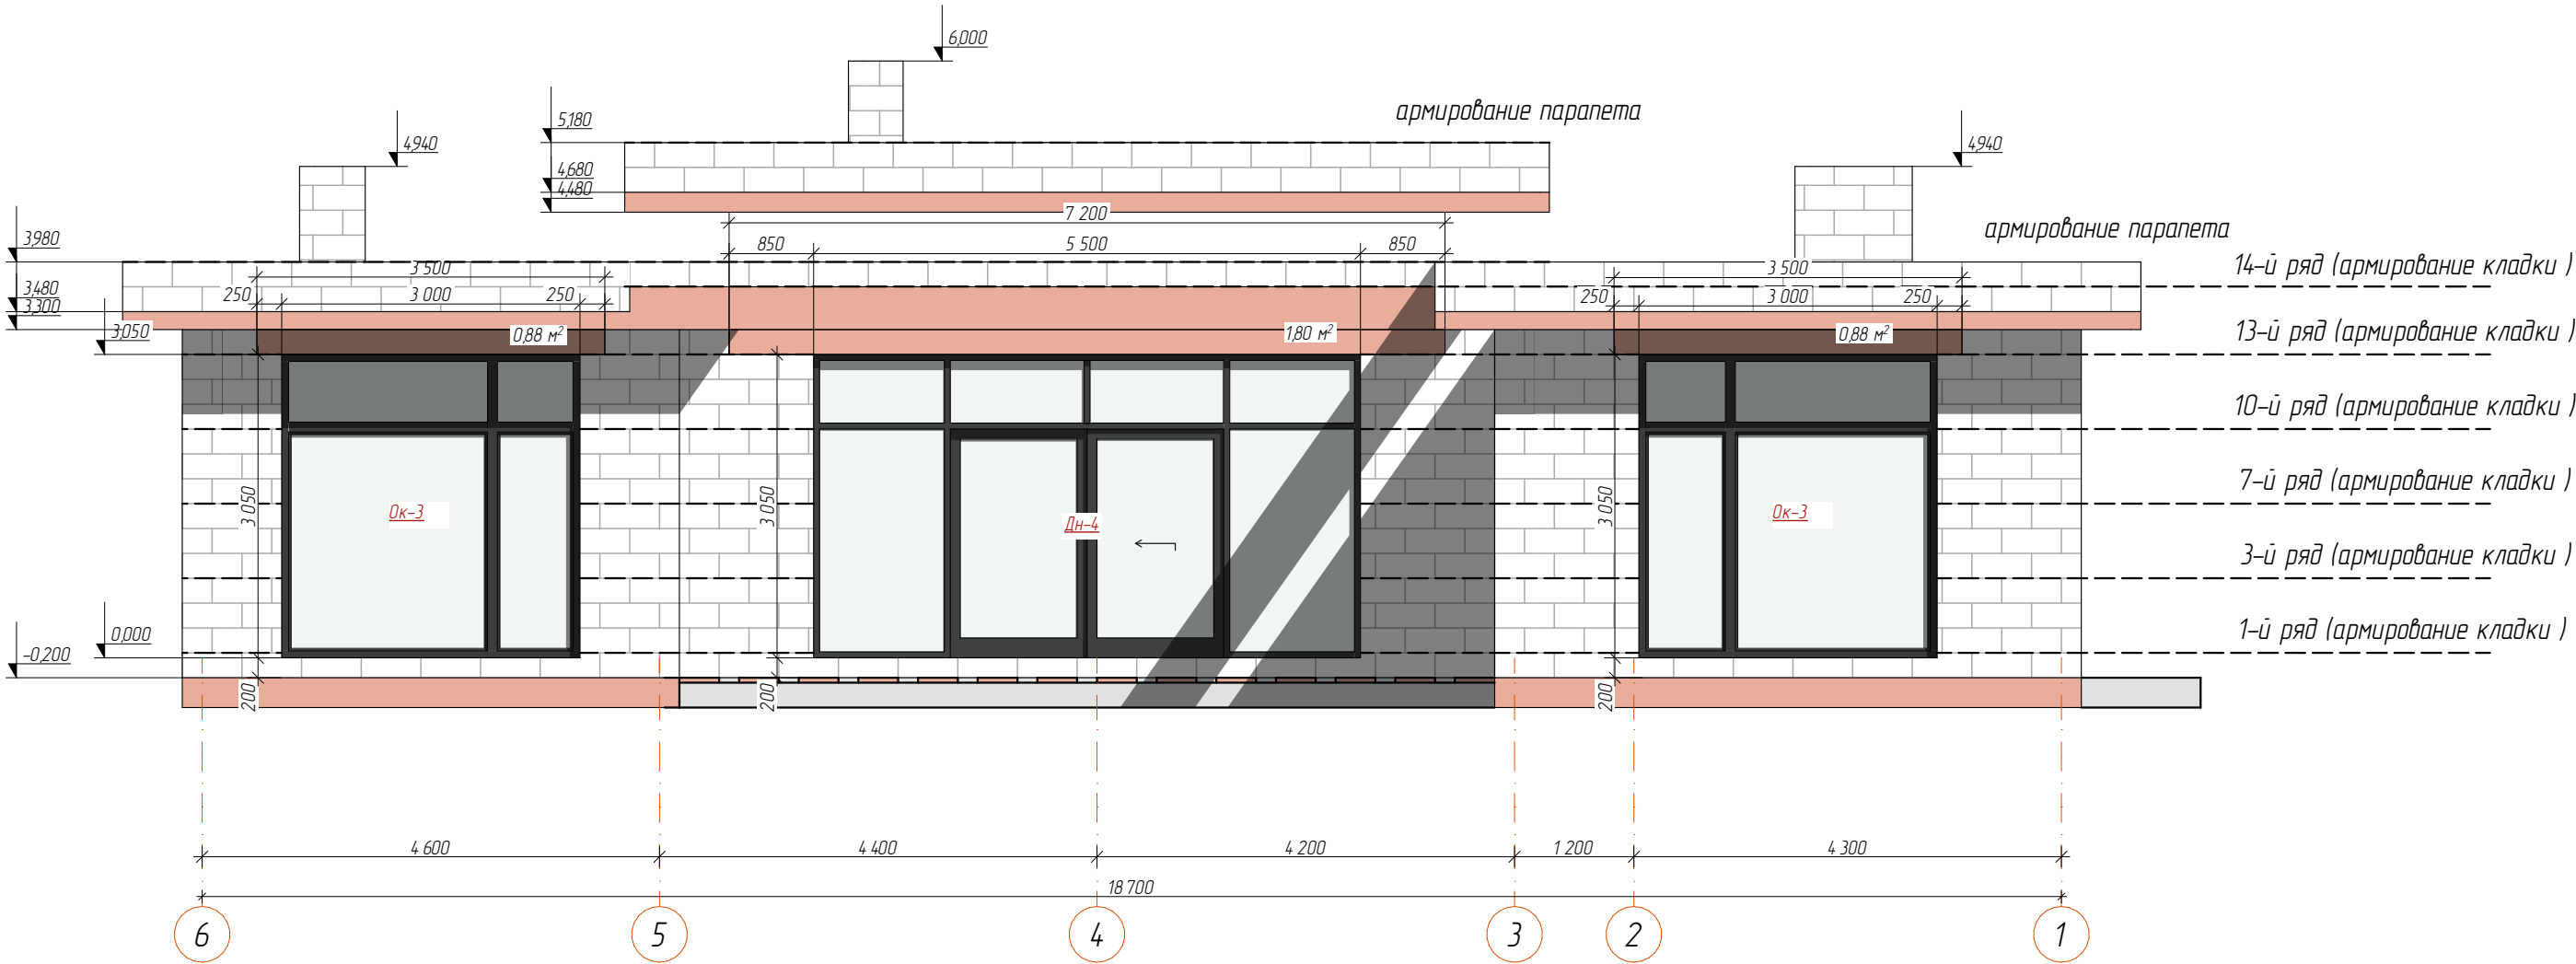

Согласовано				
Взам. инв. №				
Подпись и дата				
Инв. № подл.				

						Проект жилого дома				
Изм.	Кол.уч.	Лист	№ док.	Подпись	Дата					
ГАП		Филатов А.Г.			10.06.2026	Индивидуальный жилой дом по адресу: «Российская федерация, Московская область, г. о. Домодедово, п. Государственного племенного завода "Константиново", тер. КП "Юсупово Вилладж" участок с кад. номером 50:28:0050421:2962»		Стадия	Лист	Листов
Разработал					Р			18		
						Схема фасада 2		 Brick House строительство домов под ключ		


Схема фасада 3

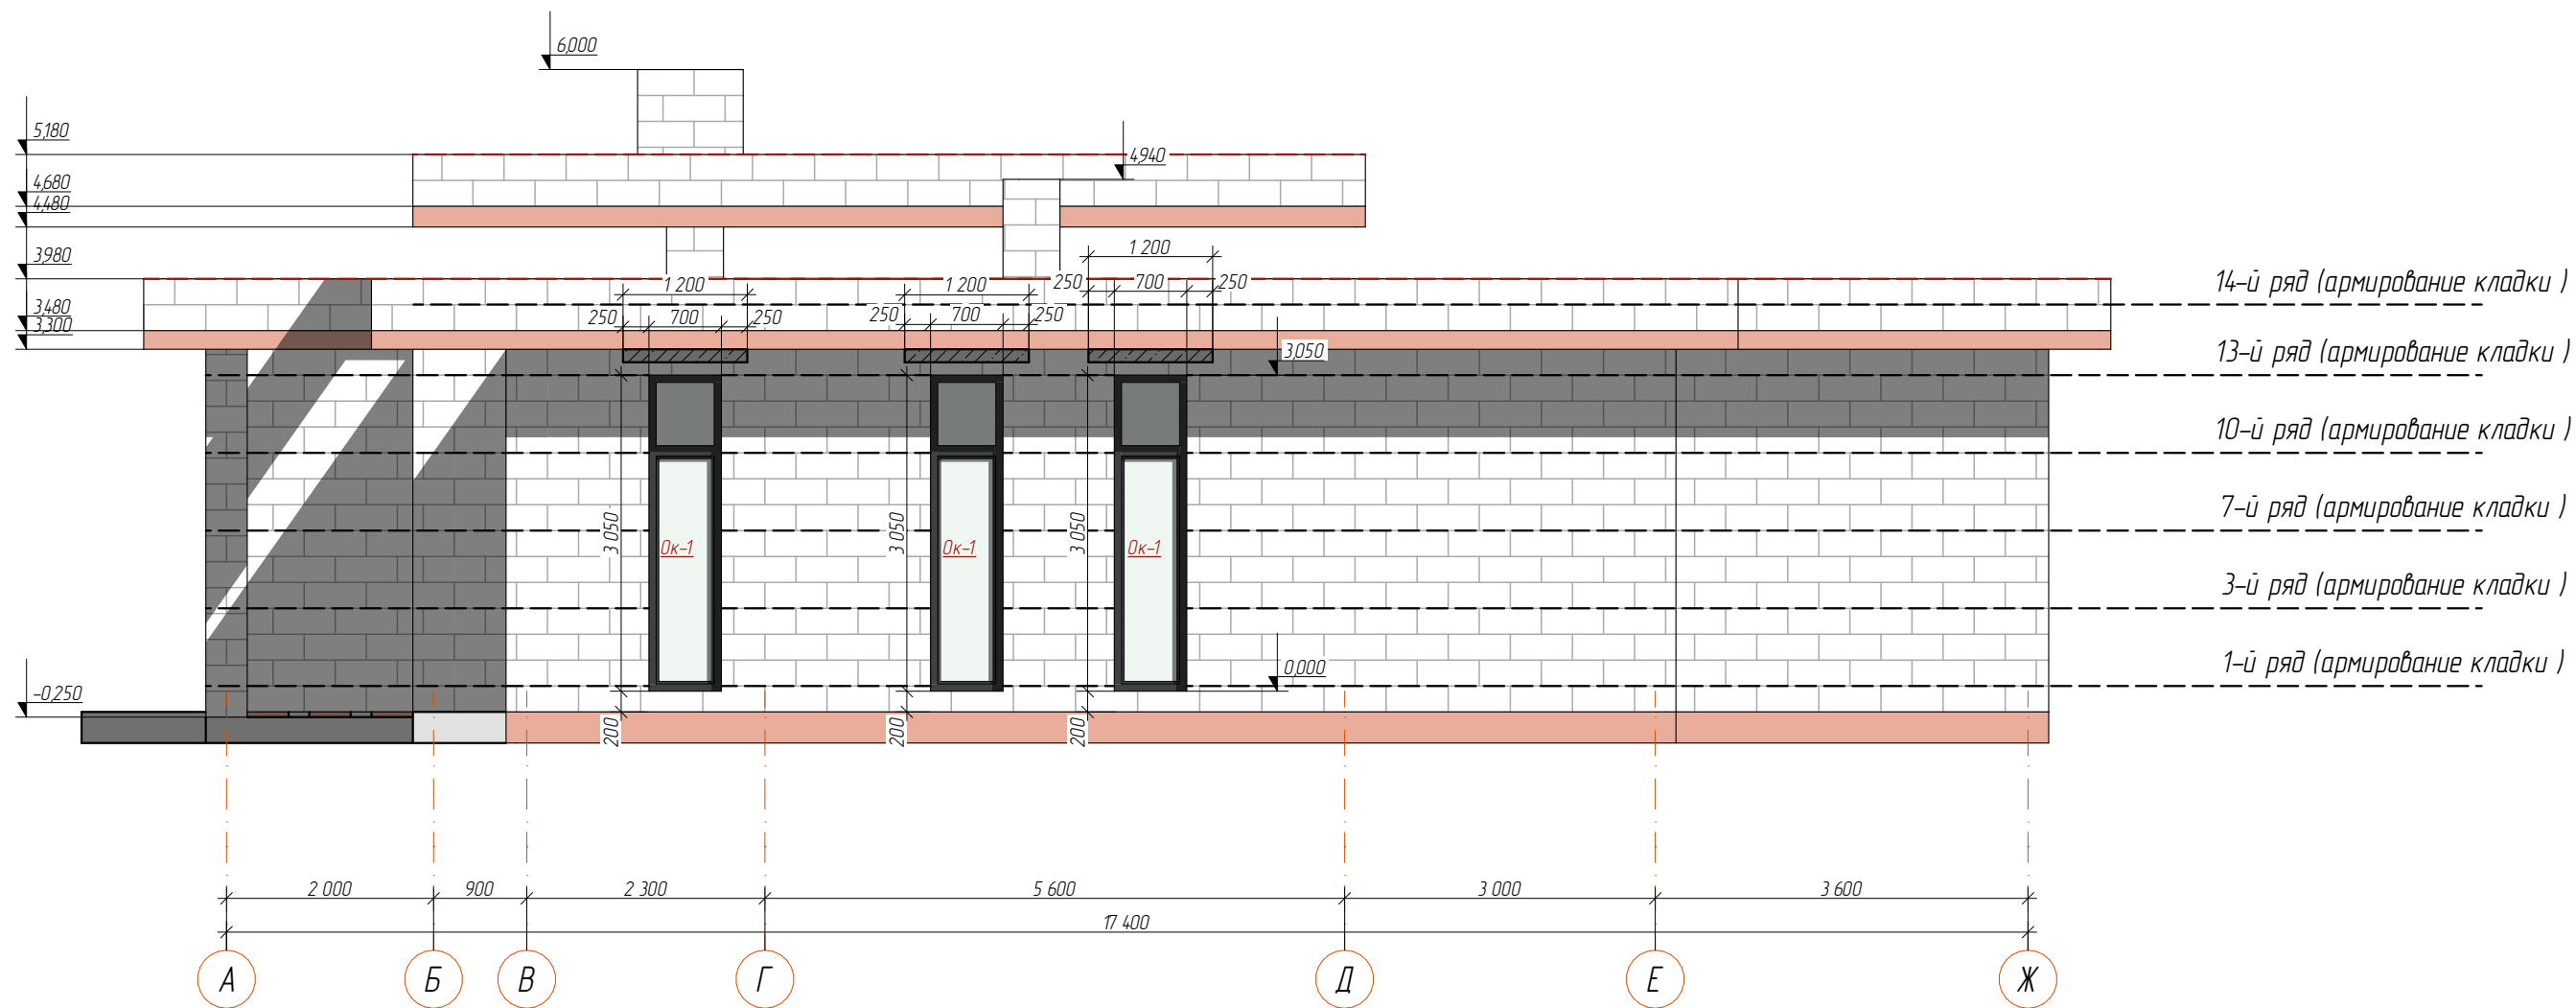

Согласовано				
Взам. инв. №				
Подпись и дата				
Инв. № подл.				

						Проект жилого дома				
Изм.	Кол.уч.	Лист	№ док.	Подпись	Дата					
ГАП		Филатов А.Г.			11.06.2026	Индивидуальный жилой дом по адресу: «Российская федерация, Московская область, г. о. Домодедово, п. Государственного племенного завода "Константиново", тер. КП "Осупово Вилладж" участок с кад. номером 50:28:0050421:2962»		Стадия	Лист	Листов
Разработал								Р	19	
						Схема фасада 3		 Brick House строительство домов под ключ		

Схема фасада 4

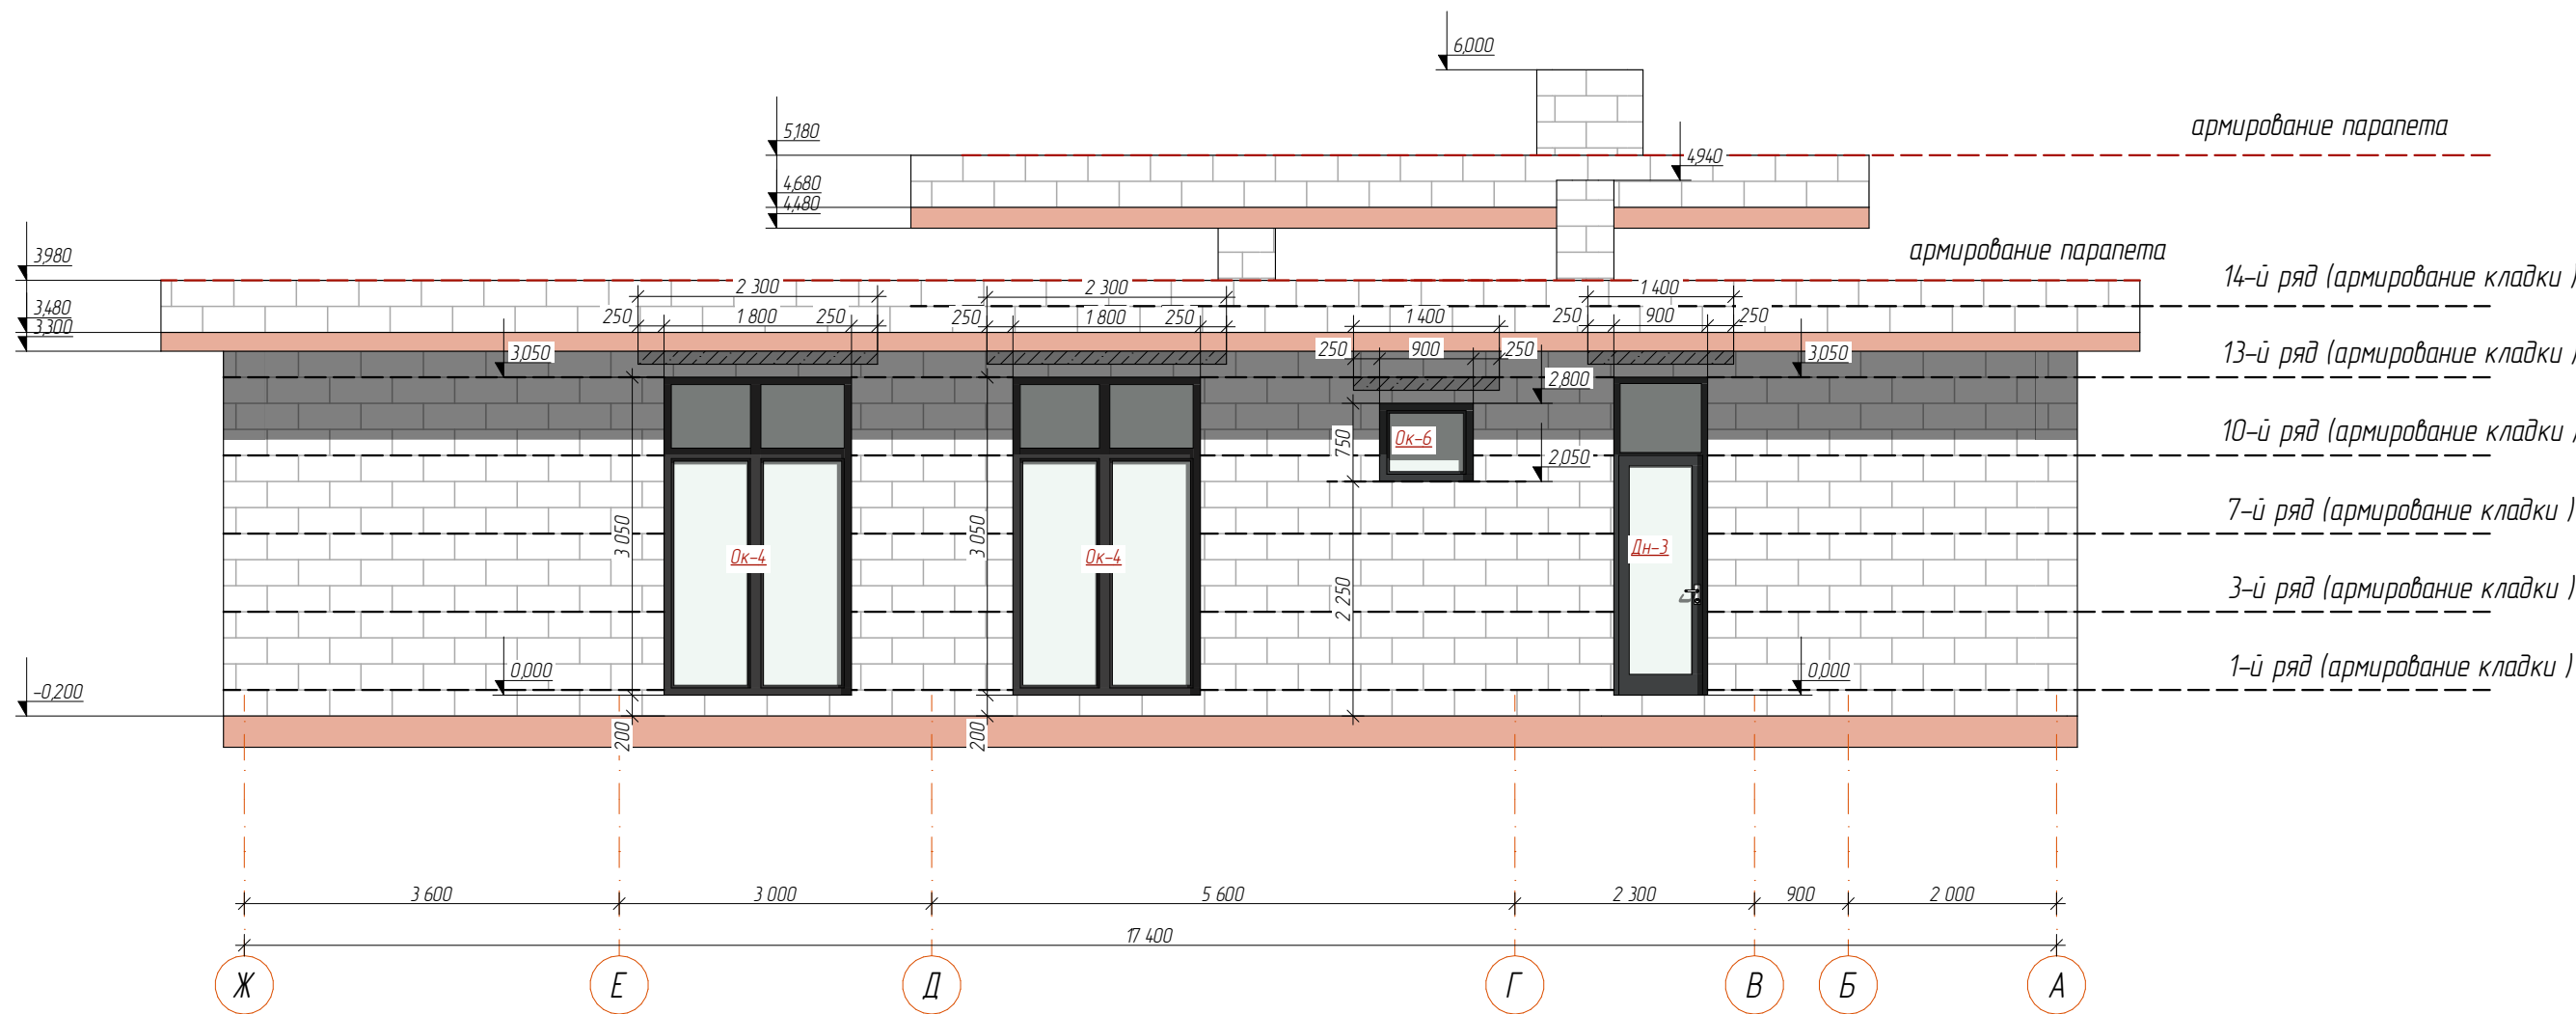

Согласовано			
Взам. инв. №			
Подпись и дата			
Инв. № подл.			

						Проект жилого дома				
Изм.	Кол.уч.	Лист	№ док.	Подпись	Дата					
ГАП		Филатов А.Г.			10.06.2026	Индивидуальный жилой дом по адресу: «Российская федерация, Московская область, г. о. Домодедово, п. Государственного племенного завода "Константиново", тер. КП "Осупово Вилладж" участок с када. номером 50:28:0050421:2962»		Стадия	Лист	Листов
Разработал								Р	20	
						Схема фасада 4		 Brick House строительство домов под ключ		


Согласовано

Взам. инв. №


Подпись и дата

Инв. № подл.


План плиты перекрытия на отм. + 3.480

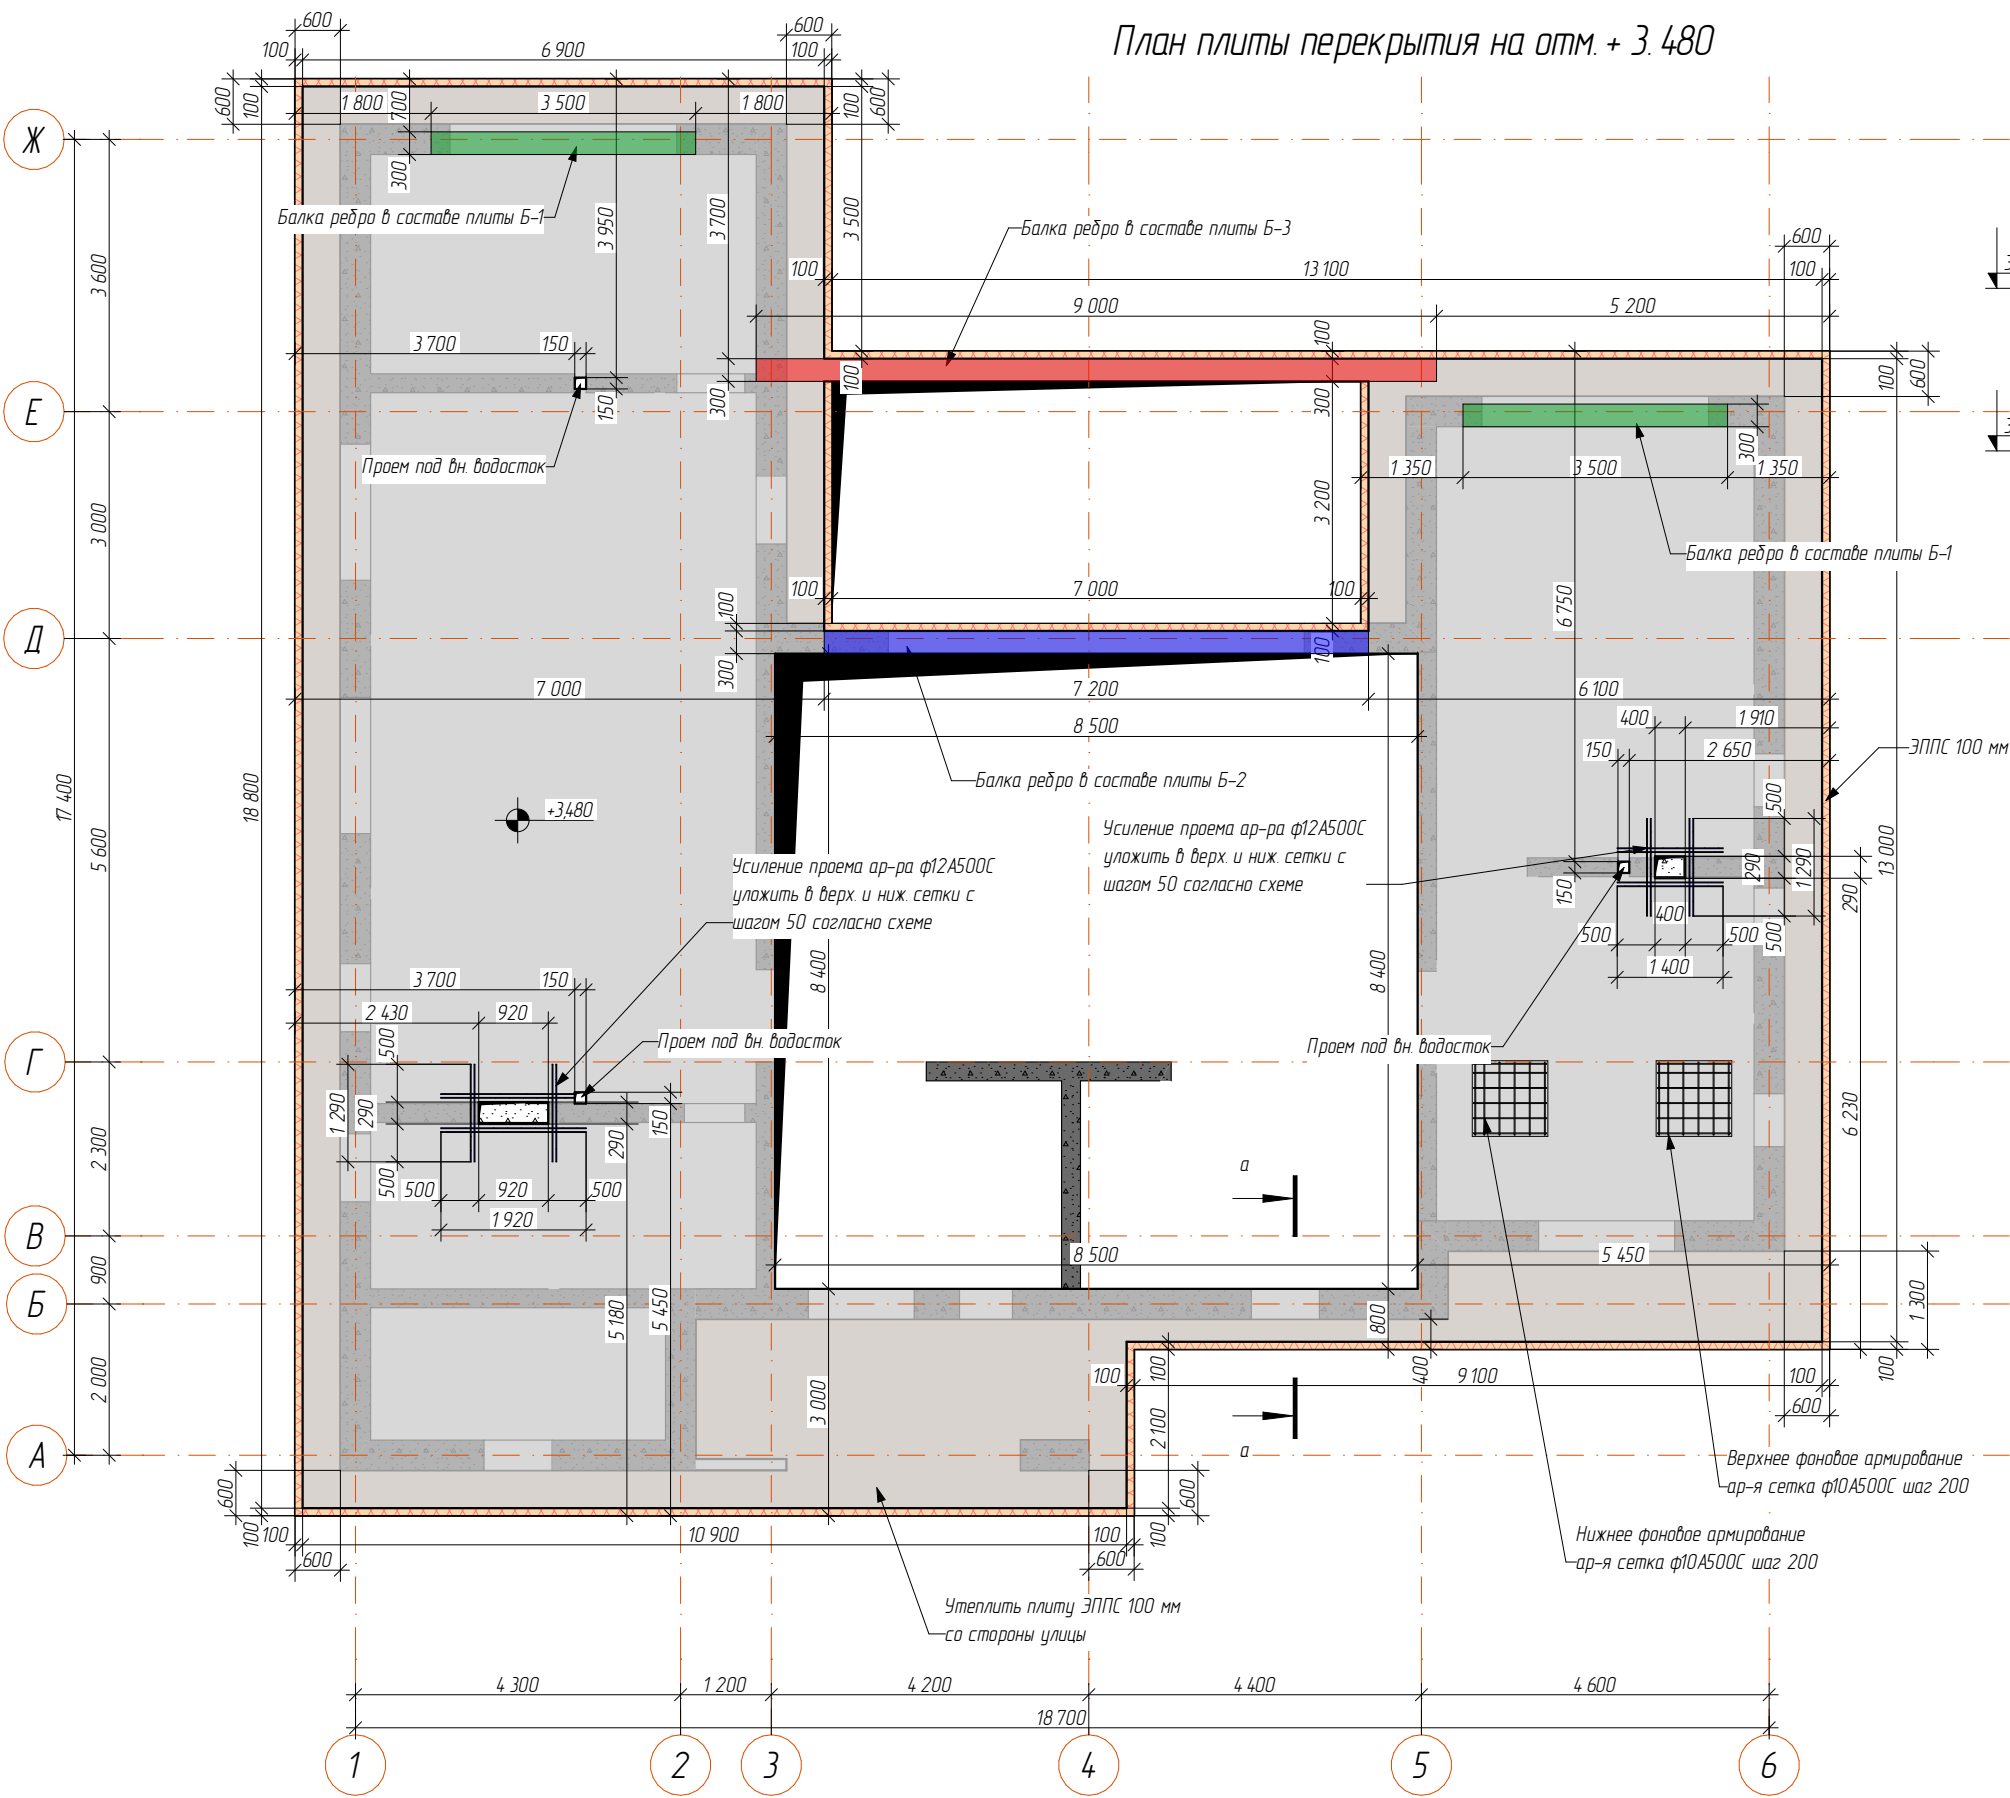


Б-1

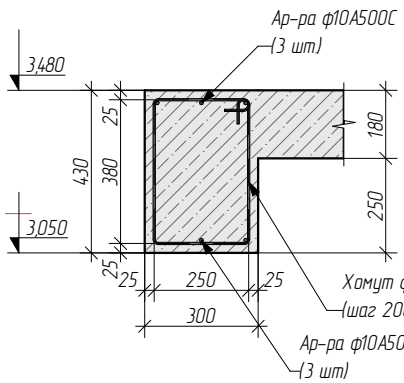


Б-2

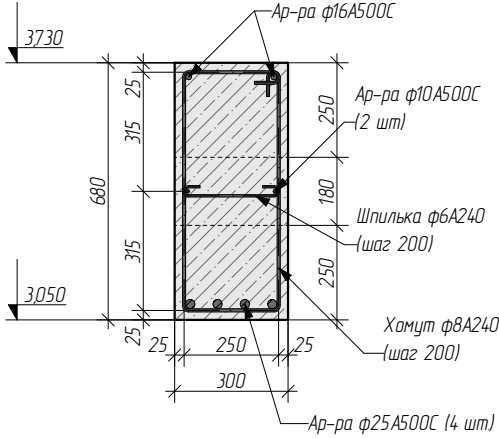

Б-3

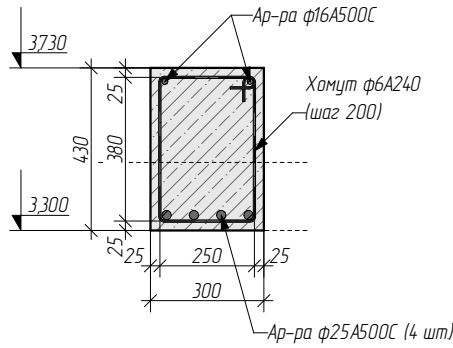

Сечение по плите перекрытия

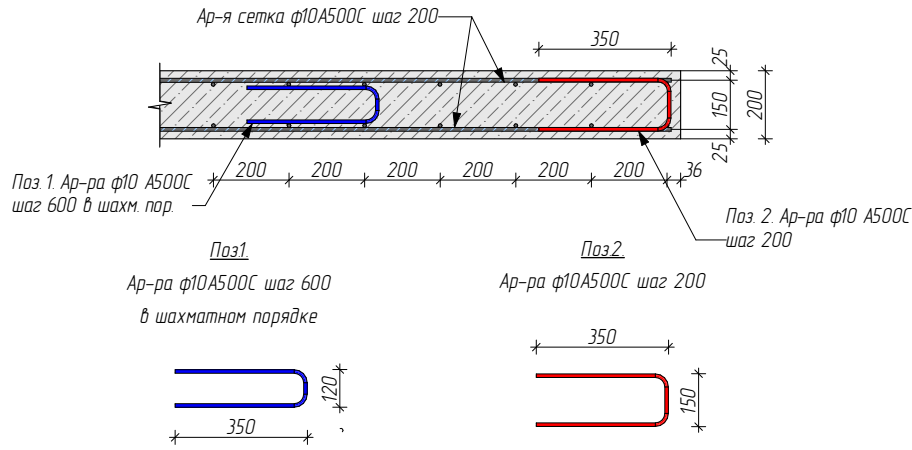

						Проект жилого дома			
Изм.	Кол. уч.	Лист	№ док.	Подпись	Дата	Индивидуальный жилой дом по адресу: «Российская федерация, Московская область, г. о. Домодедово, п. Государственного племенного завода "Константиново", тер. КП "Осупово Вилладж" участок с кад. номером 50:28:0050421:2962»	Стадия	Лист	Листов
ГАП		Филатов А.Г.			10.06.2026		Р	21	
Разработал									
						План плиты перекрытия на отм. + 3. 480	 Brick House строительство домов под ключ		

Спецификация к плите перекрытия на отм. +3,480

Спецификация к плите перекрытия на отм. +3,480

Поз.	Обозначение	Наименование	Кол-во	Масса ед. шт.	Примечание
	ГОСТ 26633-2015	Бетон В 22,5 W6 F150 П4 (плита)	38,22		м³
	ГОСТ 26633-2015	Бетон В 22,5 W6 F150 П4 (балки)	2,63		м³
	ГОСТ 32310-2012	ЭППС 100 мм (низ плиты)	50,4		м³
	ГОСТ 32310-2012	ЭППС 100 мм (торец плиты)	26,6		м²
	ГОСТ 34028-2016	φ10 А500С (ар-я сетка, П-ки, фиксаторы, балки)	6320	0,617	м/п
	ГОСТ 34028-2016	φ12 А500С (усиление проемов)	47,3	0,888	м/п
	ГОСТ 34028-2016	φ25 А500С (балки)	4,2	3,85	м/п
	ГОСТ 34028-2016	φ16 А500С (балки)	32,52	1,6	м/п
	ГОСТ 34028-2016	φ6 А240 (балки)	67,56	0,222	м/п
	ГОСТ 34028-2016	φ8 А240 (балки)	17	0,395	м/п

Спецификация Ж\Б балок

Поз.	Длина	Ширина	Высота	Бетон	Опалубка
Б-1	7	0,3	0,25	0,525	3,8
Б-2	7,2	0,3	0,68	1,46	10,1
Б-3	9	0,3	0,43	1,16	8,14
Итого	23,2			3,16	22,04

Согласовано				
Взам. инв. №				
Подпись и дата				
Инв. № подл.				


						Проект жилого дома			
Изм.	Кол. уч.	Лист	№ док.	Подпись	Дата	Индивидуальный жилой дом по адресу: «Российская федерация, Московская область, г.о. Домодедово, п. Государственного племенного завода "Константиново", тер. КП "Юсупово Вилладж" участок с када. номером 50:28:0050421:2962»	Стадия	Лист	Листов
ГАП		Филатов А.Г.			10.06.2026		Р	22	
Разработал							Спецификация к плите перекрытия на отм. +3,480		

Согласовано



Формат А3


Нижнее дополнительное армирование плиты на отм. + 3.300

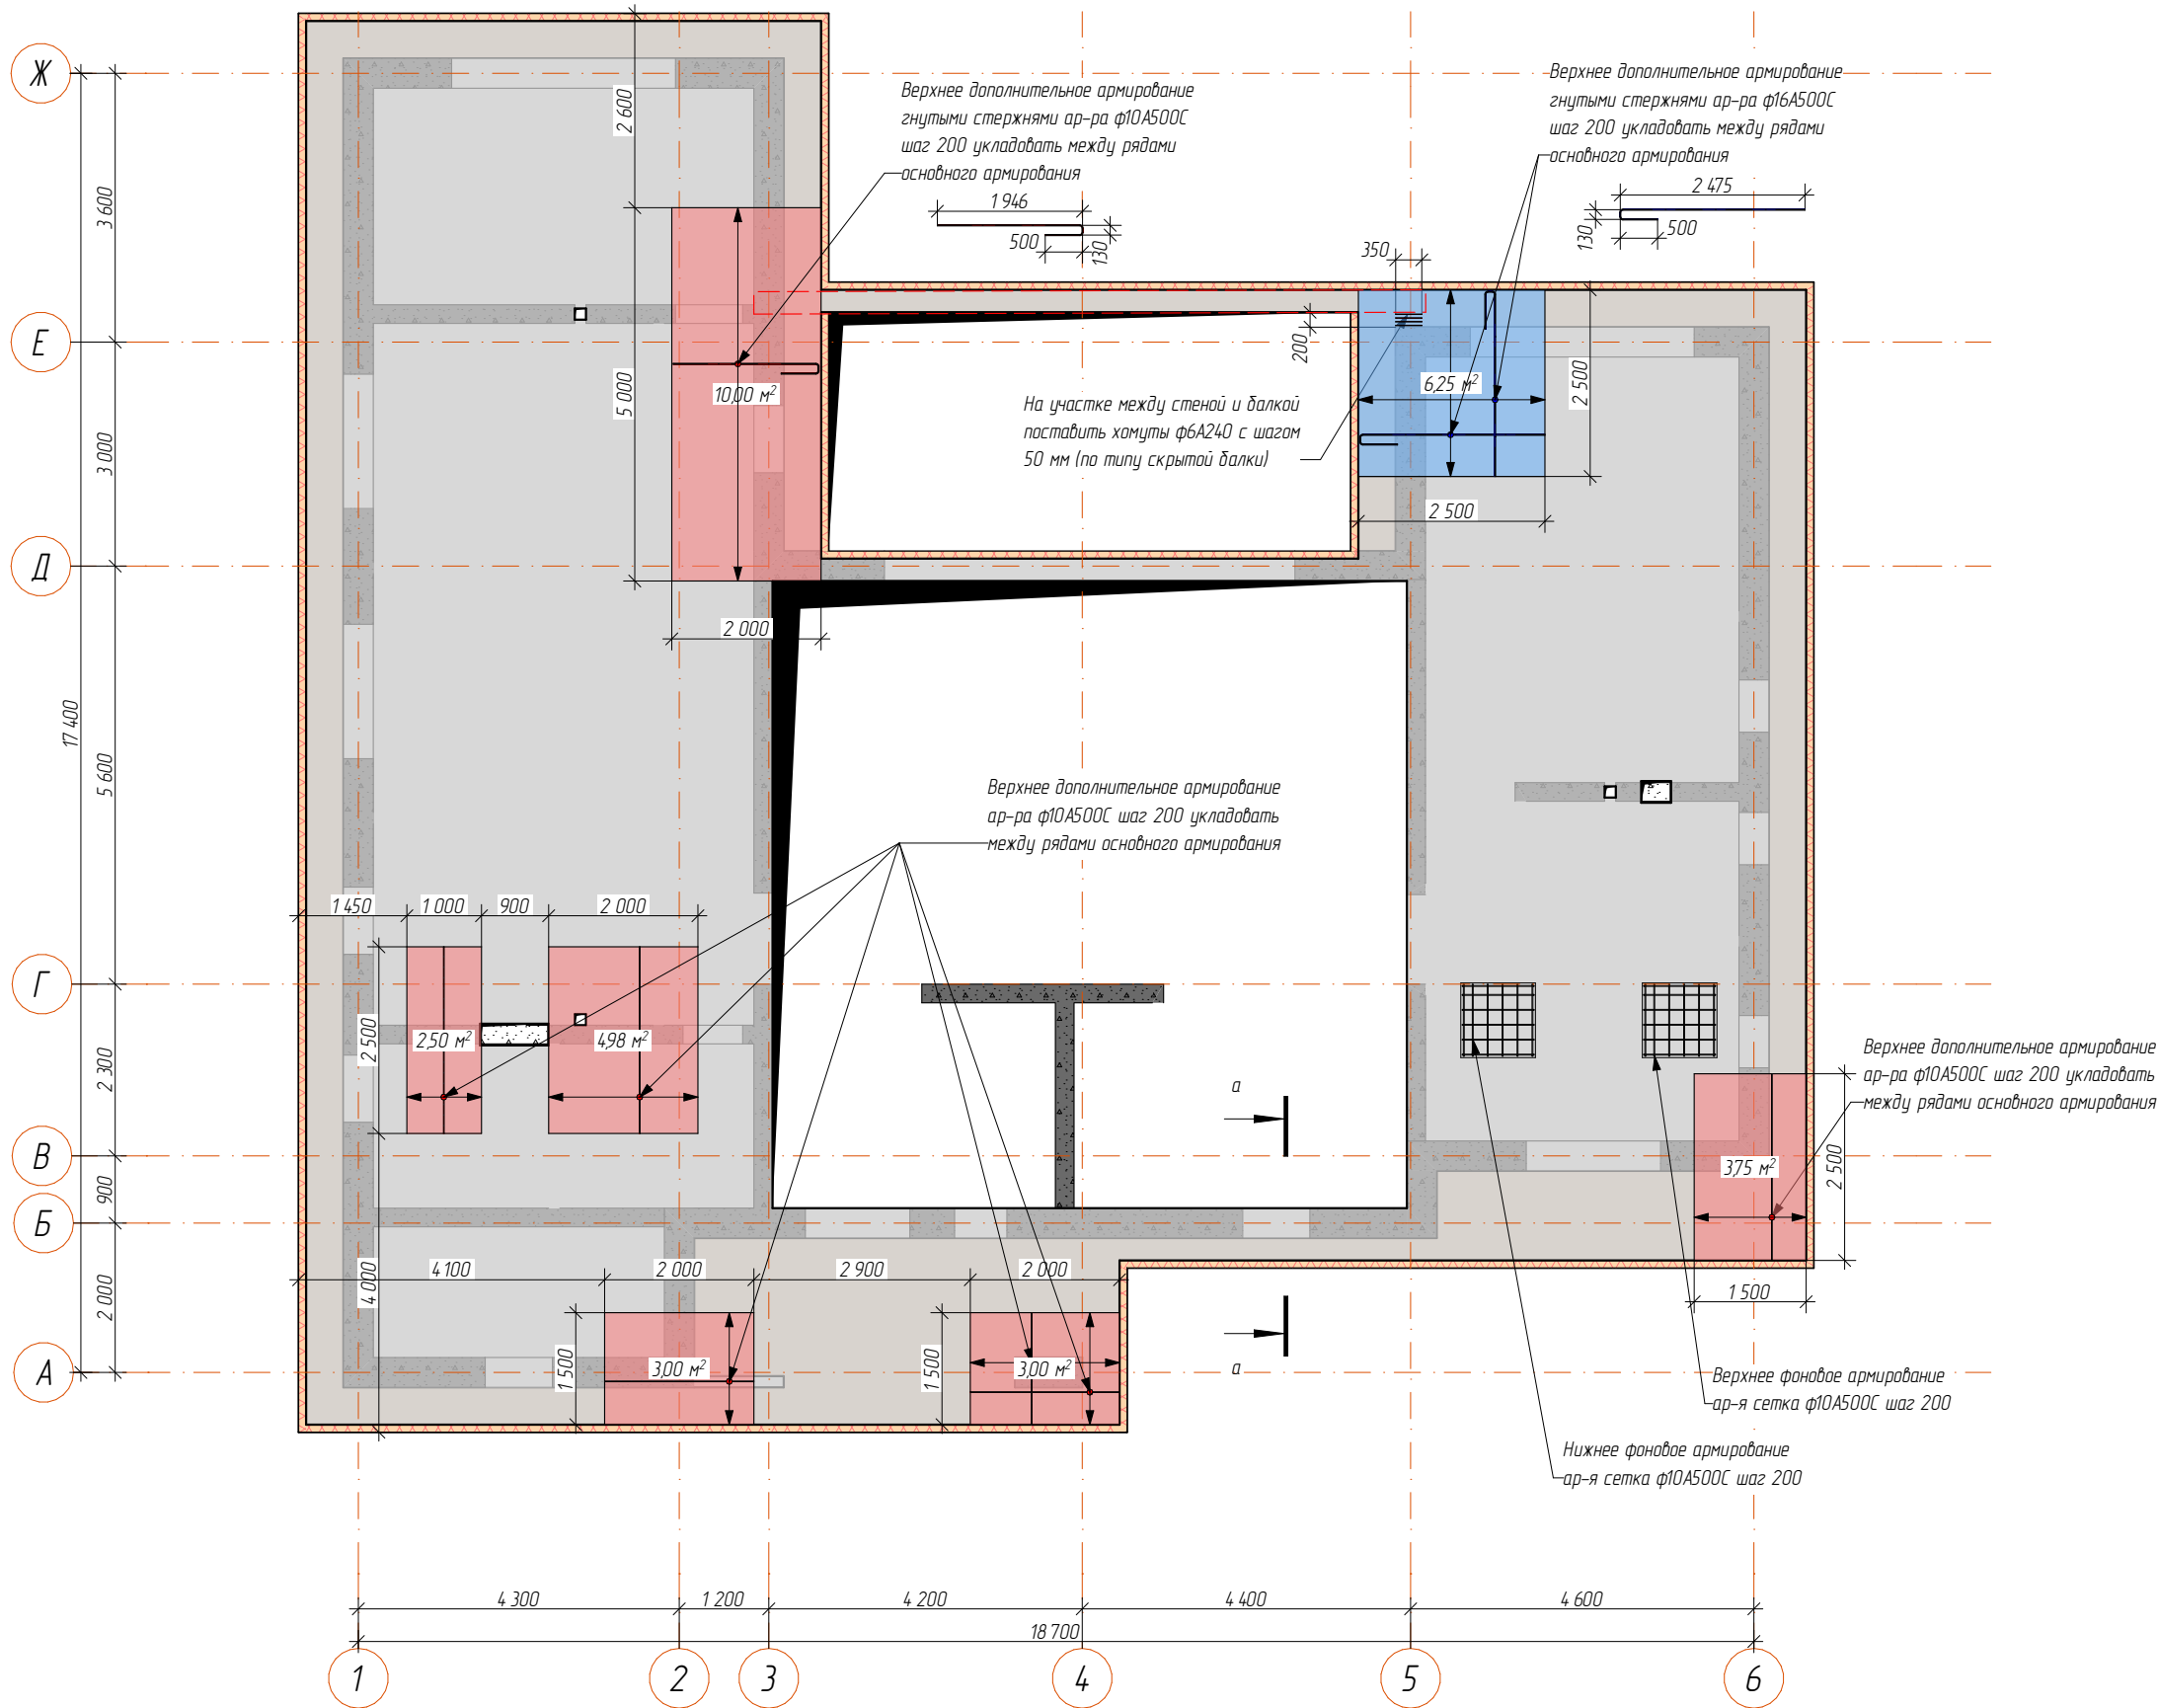


Поз.	Обозначение	Наименование	Кол-во	Масса ед. шт.	Примечание
	ГОСТ 34028-2016	ф10 A500C	90	0,617	м/п
	ГОСТ 34028-2016	ф16 A500C	60	1,6	м/п

						Проект жилого дома			
Изм.	Кол.уч.	Лист	№ док.	Подпись	Дата	Индивидуальный жилой дом по адресу: «Российская федерация, Московская область, г. о. Домодедово, п. Государственного племенного завода "Константиново", тер. КП "Юсупово Вилладж" участок с кад. номером 50:28:0050421:2962»	Стадия	Лист	Листов
ГАП		Филатов А.Г.			11.06.2026		Р	24	
Разработал									
						Нижнее дополнительное армирование плиты на отм. + 3.300	 Brick House строительство домов под ключ		

План плиты перекрытия на отм. + 4.680

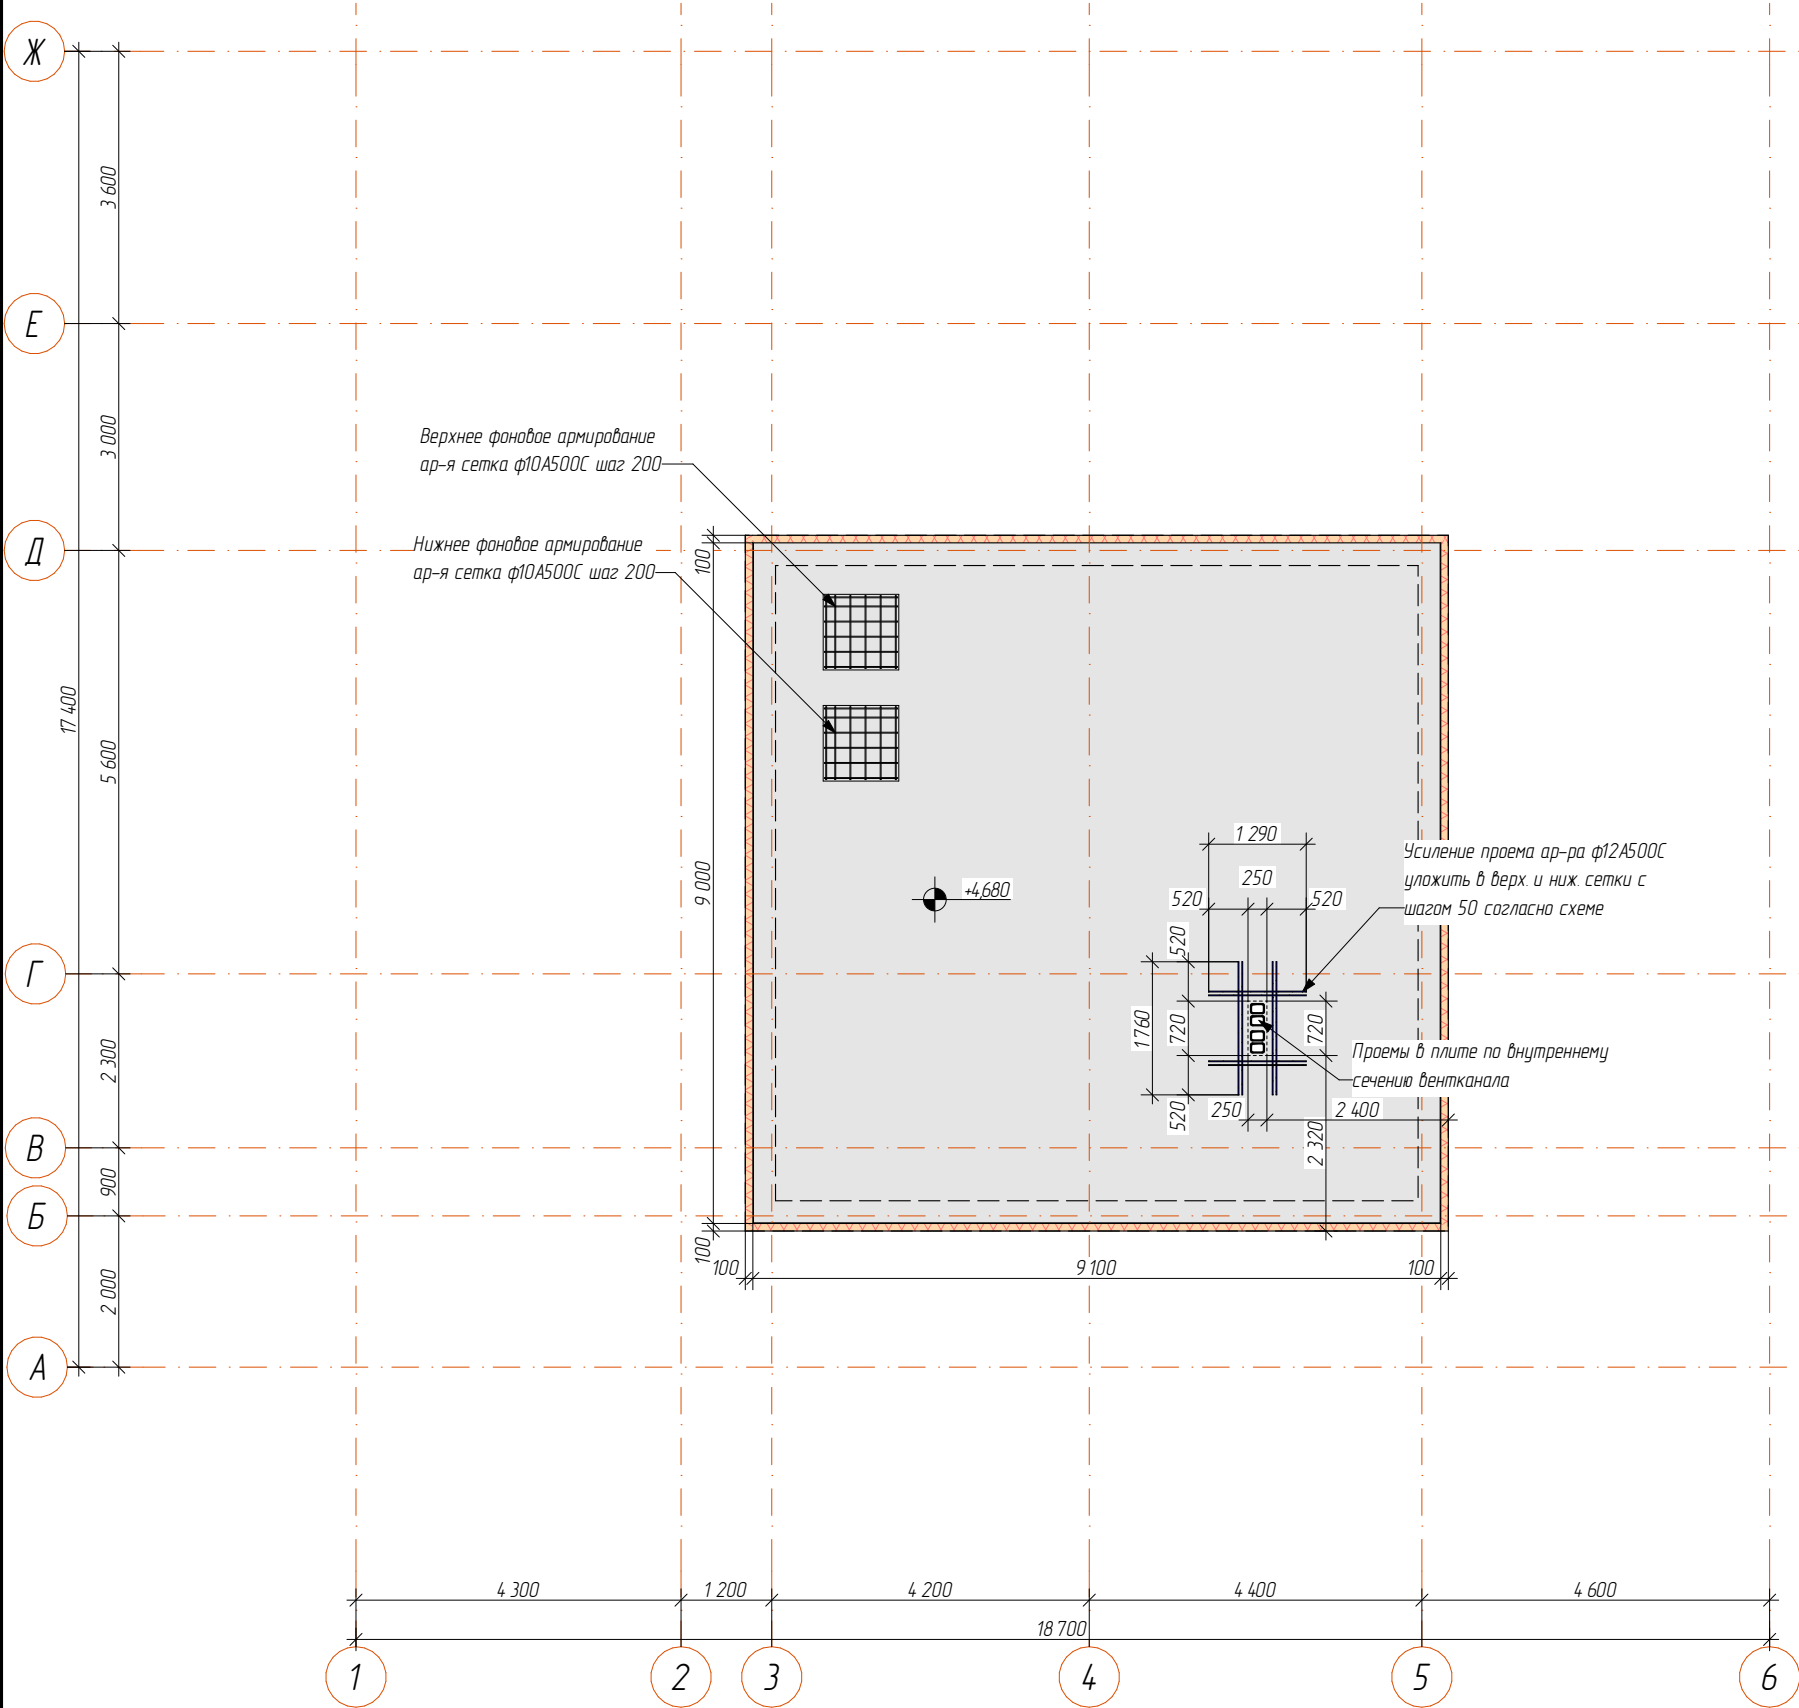

Сечение по плите перекрытия

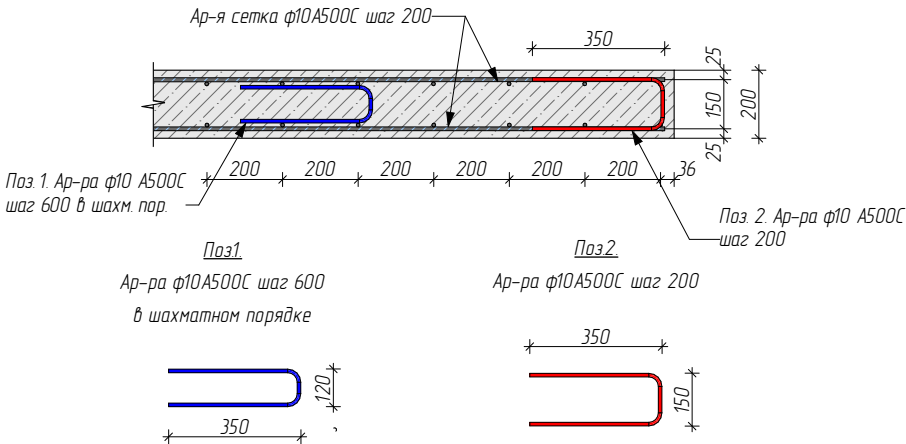


Спецификация к плите перкрытия на отм. +4.680

Поз	Обозначение	Наименование	Кол-во	Масса ед. шт.	Примечание
	ГОСТ 26633-2015	Бетон В 22,5 W6 F150 П4	16,5		м³
	ГОСТ 32310-2012	ЭППС 100 мм (торец плиты)	7,4		м²
	ГОСТ 34028-2016	φ10 A500C (ар-я сетка, П-ки, фиксаторы)	24,31	0,617	кг
	ГОСТ 34028-2016	φ12 A500C (усиление проемов)	24,77	0,888	кг
		Площадь опалубки	212,35		м²
		Плотность армирования	22		м/п на 1 м2

Согласовано					
Взам. инв. №					
Подпись и дата					
Инв. № подл.					

						Проект жилого дома			
Изм.	Кол. уч.	Лист	№ док.	Подпись	Дата	Индивидуальный жилой дом по адресу: «Российская федерация, Московская область, г. о. Домодедово, п. Государственного племенного завода "Константиново", тер. КП "Осупово Вилладж" участок с кад. номером 50:28:0050421:2962»	Стадия	Лист	Листов
ГАП		Филатов А.Г.			10.06.2026		Р	25	
Разработал									
						План плиты перекрытия на отм. + 4. 680	 Brick House строительство домов под ключ		


Нижнее дополнительное армирование плиты на отм. +4,680

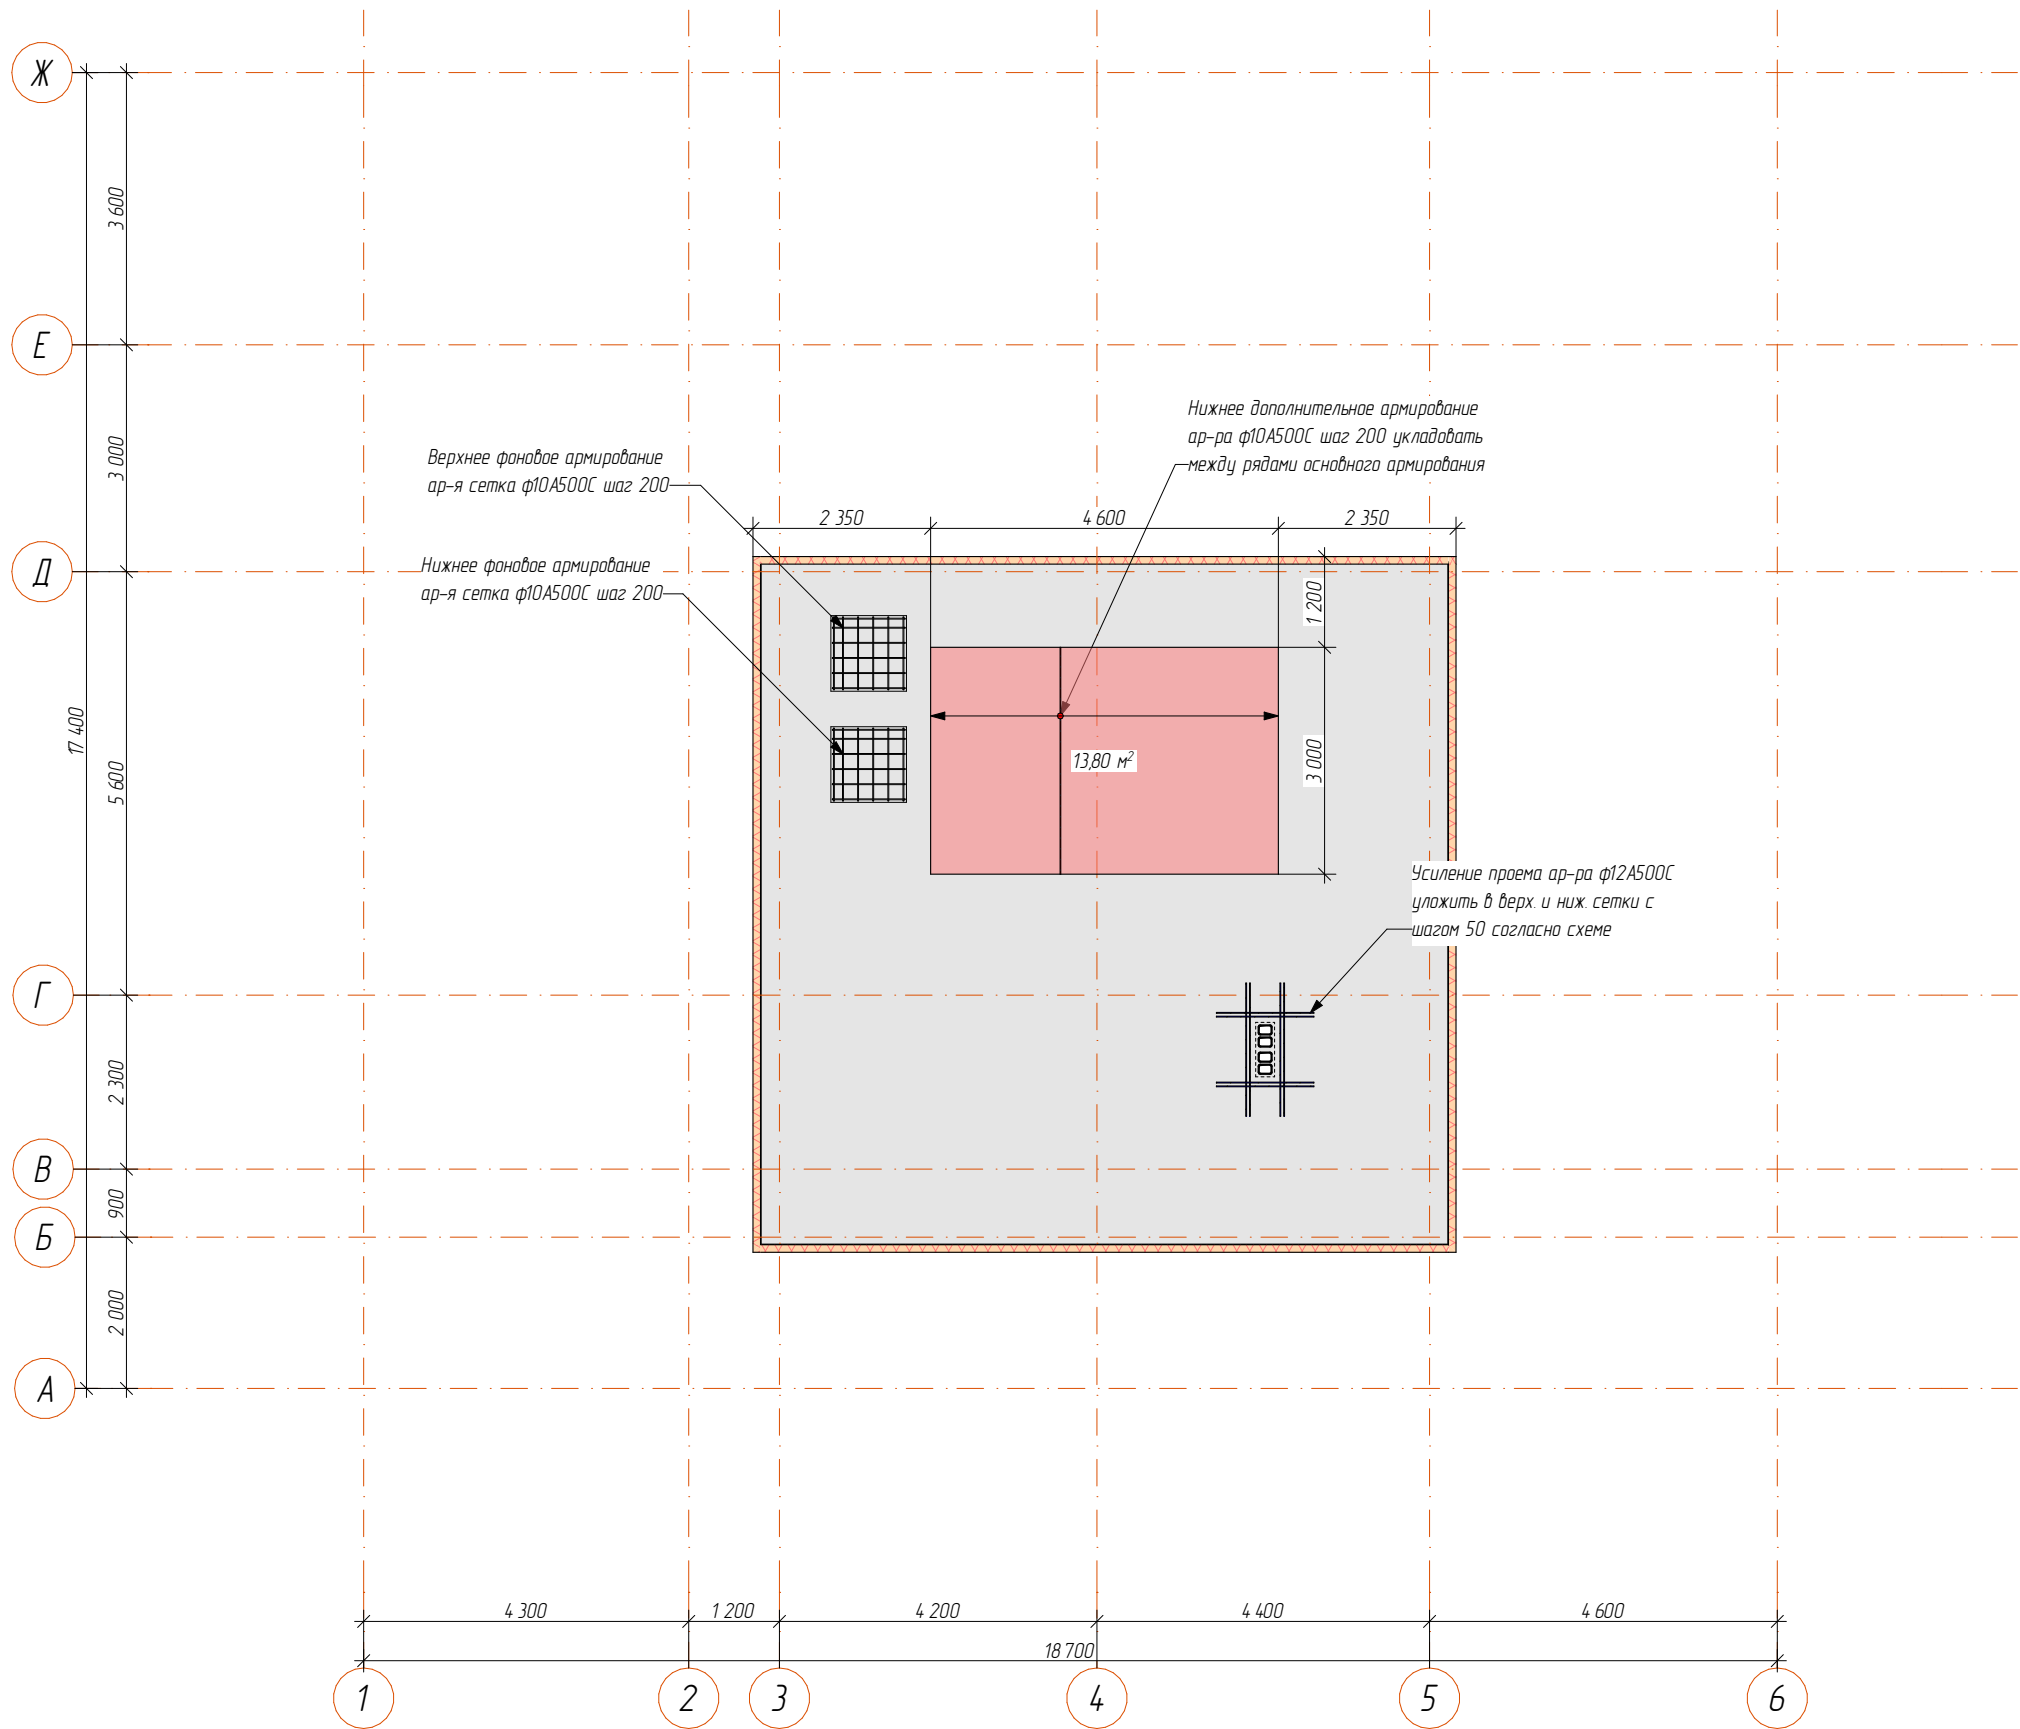

Согласовано				
Взам. инв. №				
Подпись и дата				
Инв. № подл.				

						Проект жилого дома			
Изм.	Кол.уч.	Лист	№ док.	Подпись	Дата	Индивидуальный жилой дом по адресу: «Российская федерация, Московская область, г. о. Домодедово, п. Государственного племенного завода "Константиново", тер. КП "Юсупово Вилладж" участок с кад. номером 50:28:0050421:2962»	Стадия	Лист	Листов
ГАП	Филатов А.Г.				10.06.2026		Р	26	
Разработал									
						Нижнее дополнительное армирование плиты на отм. +4,680	 Brick House строительство домов под ключ		

Верхнее дополнительное армирование плиты на отм. +4,680

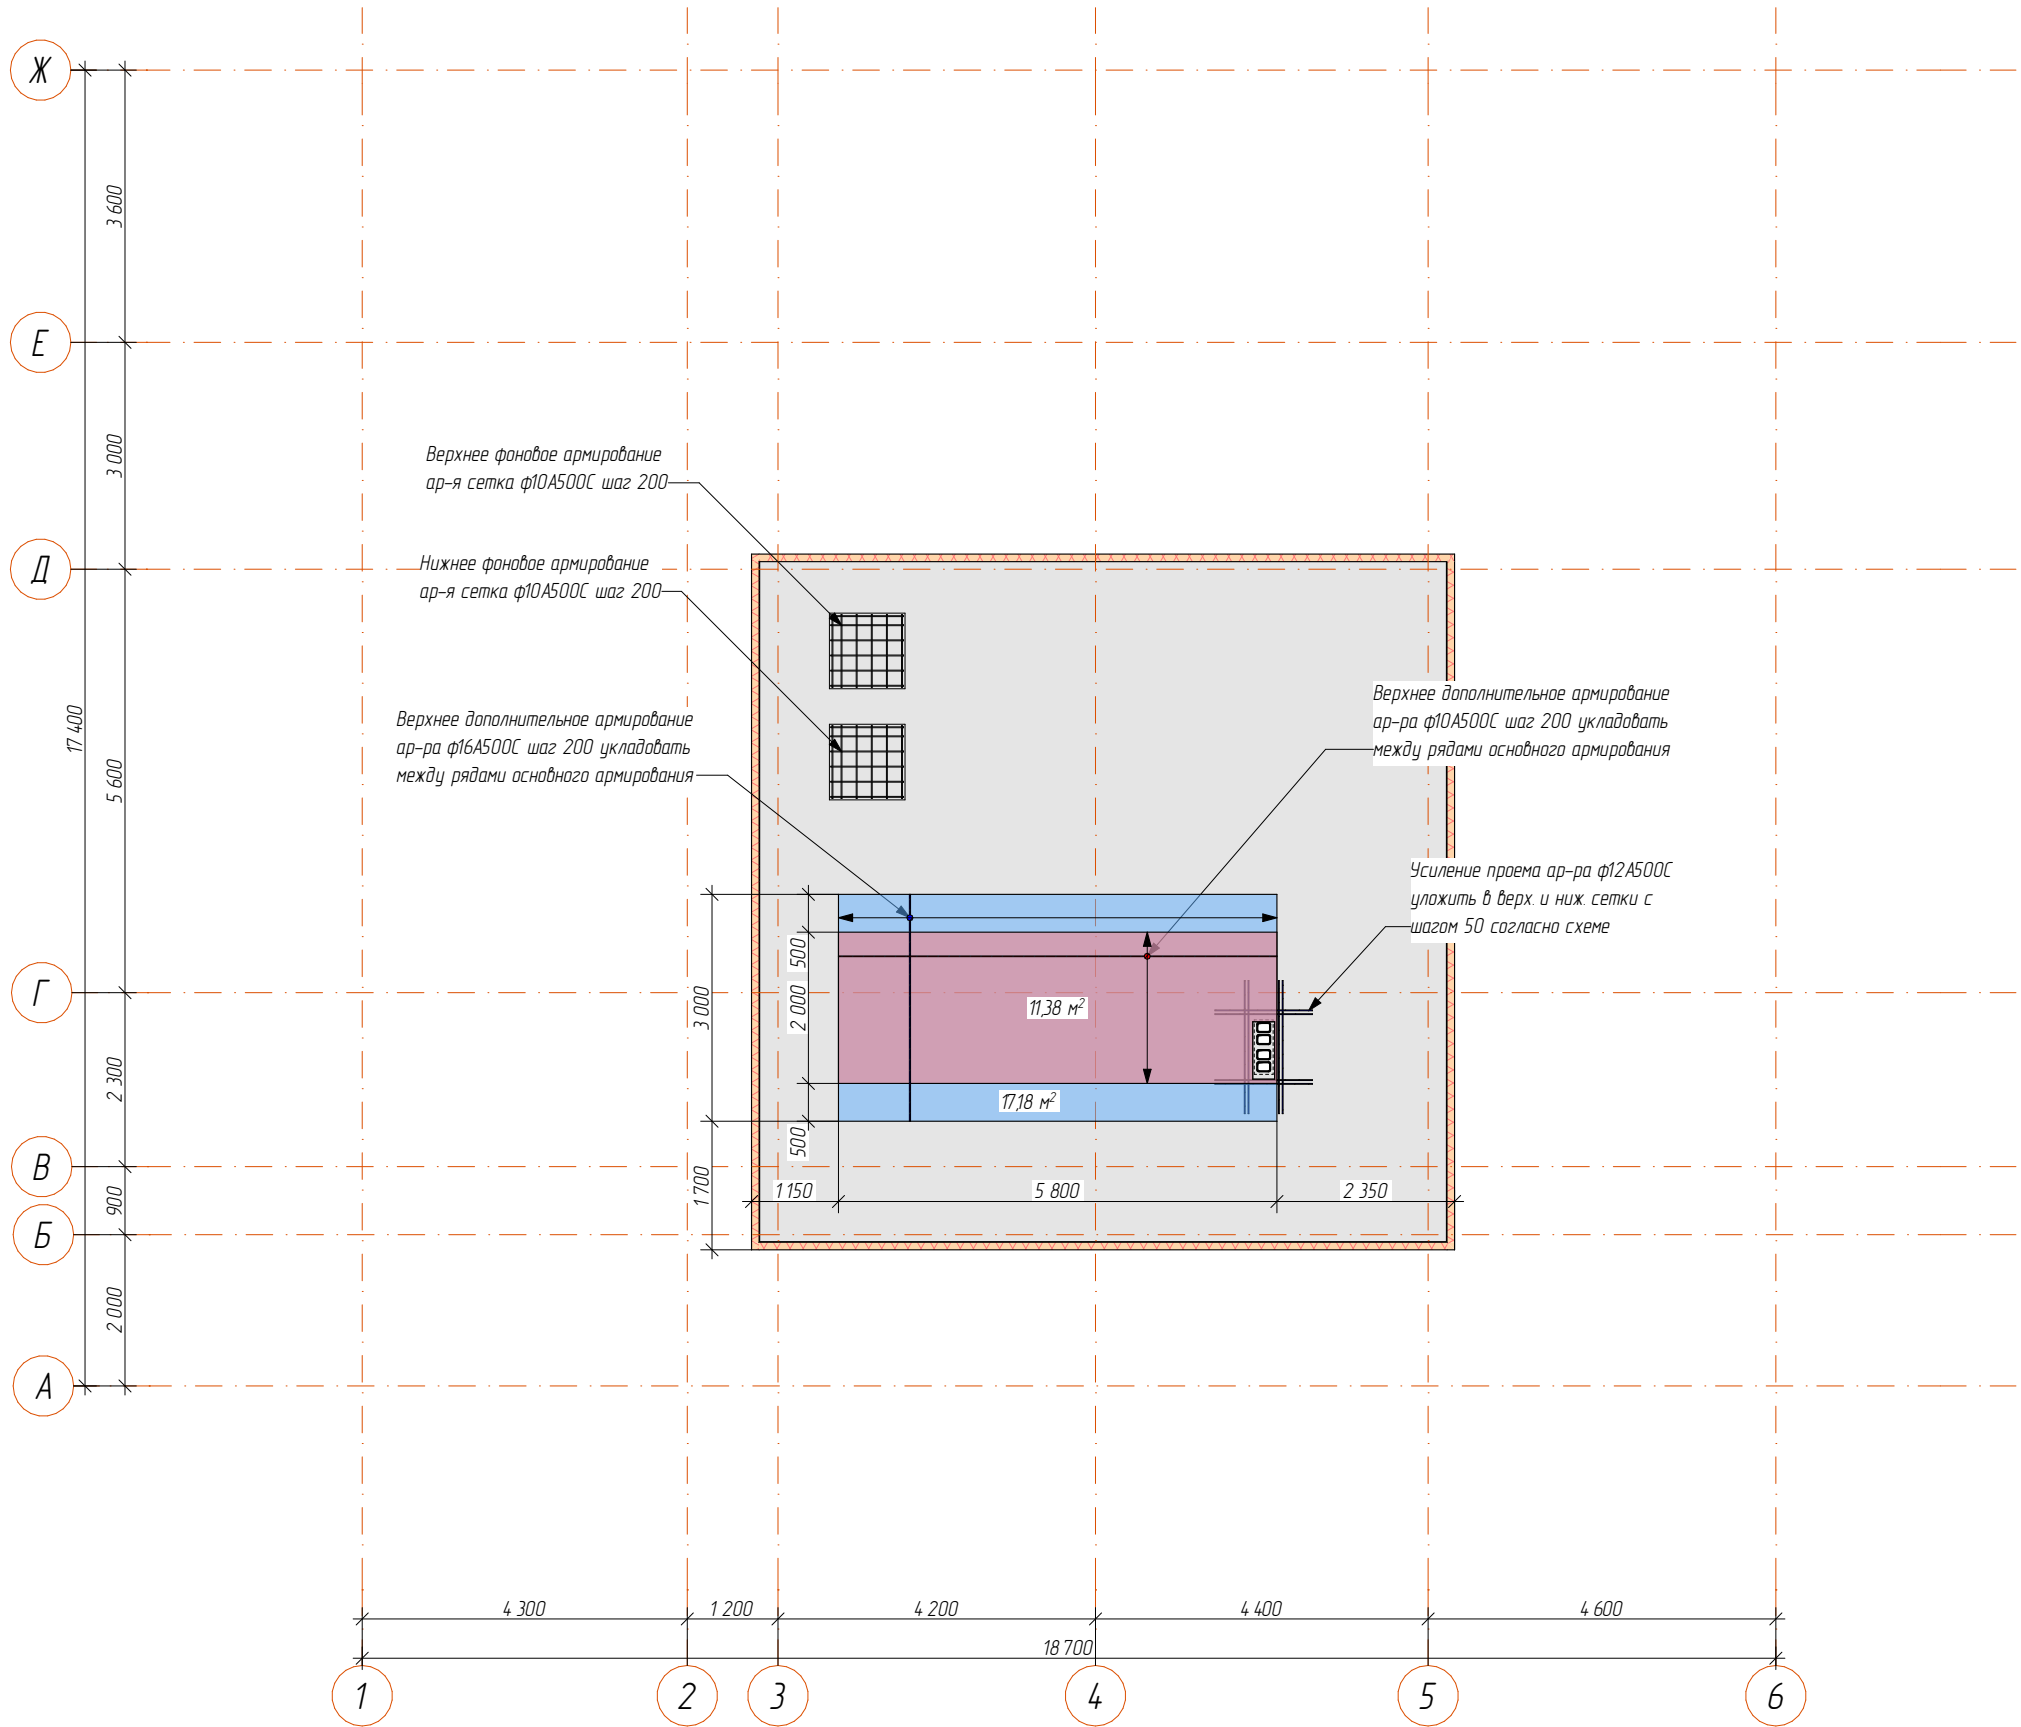


Спецификация к дополнительному армированию

Поз.	Обозначение	Наименование	Кол-во	Масса ед. шт.	Примечание
	ГОСТ 34028-2016	ф16 A500C	89	1,6	м/п
	ГОСТ 34028-2016	ф10 A500C	57	0,617	м/п

						Проект жилого дома					
Изм.	Кол.уч.	Лист	№ док.	Подпись	Дата	Индивидуальный жилой дом по адресу: «Российская федерация, Московская область, г. о. Домодедово, п. Государственного племенного завода "Константиново", тер. КП "Юсупово Вилладж" участок с кад. номером 50:28:0050421:2962»			Стадия	Лист	Листов
ГАП		Филатов А.Г.			10.06.2026				Р	27	
Разработал									 Brick House строительство домов под ключ		
						Верхнее дополнительное армирование плиты на отм. +4,680					

План кровли

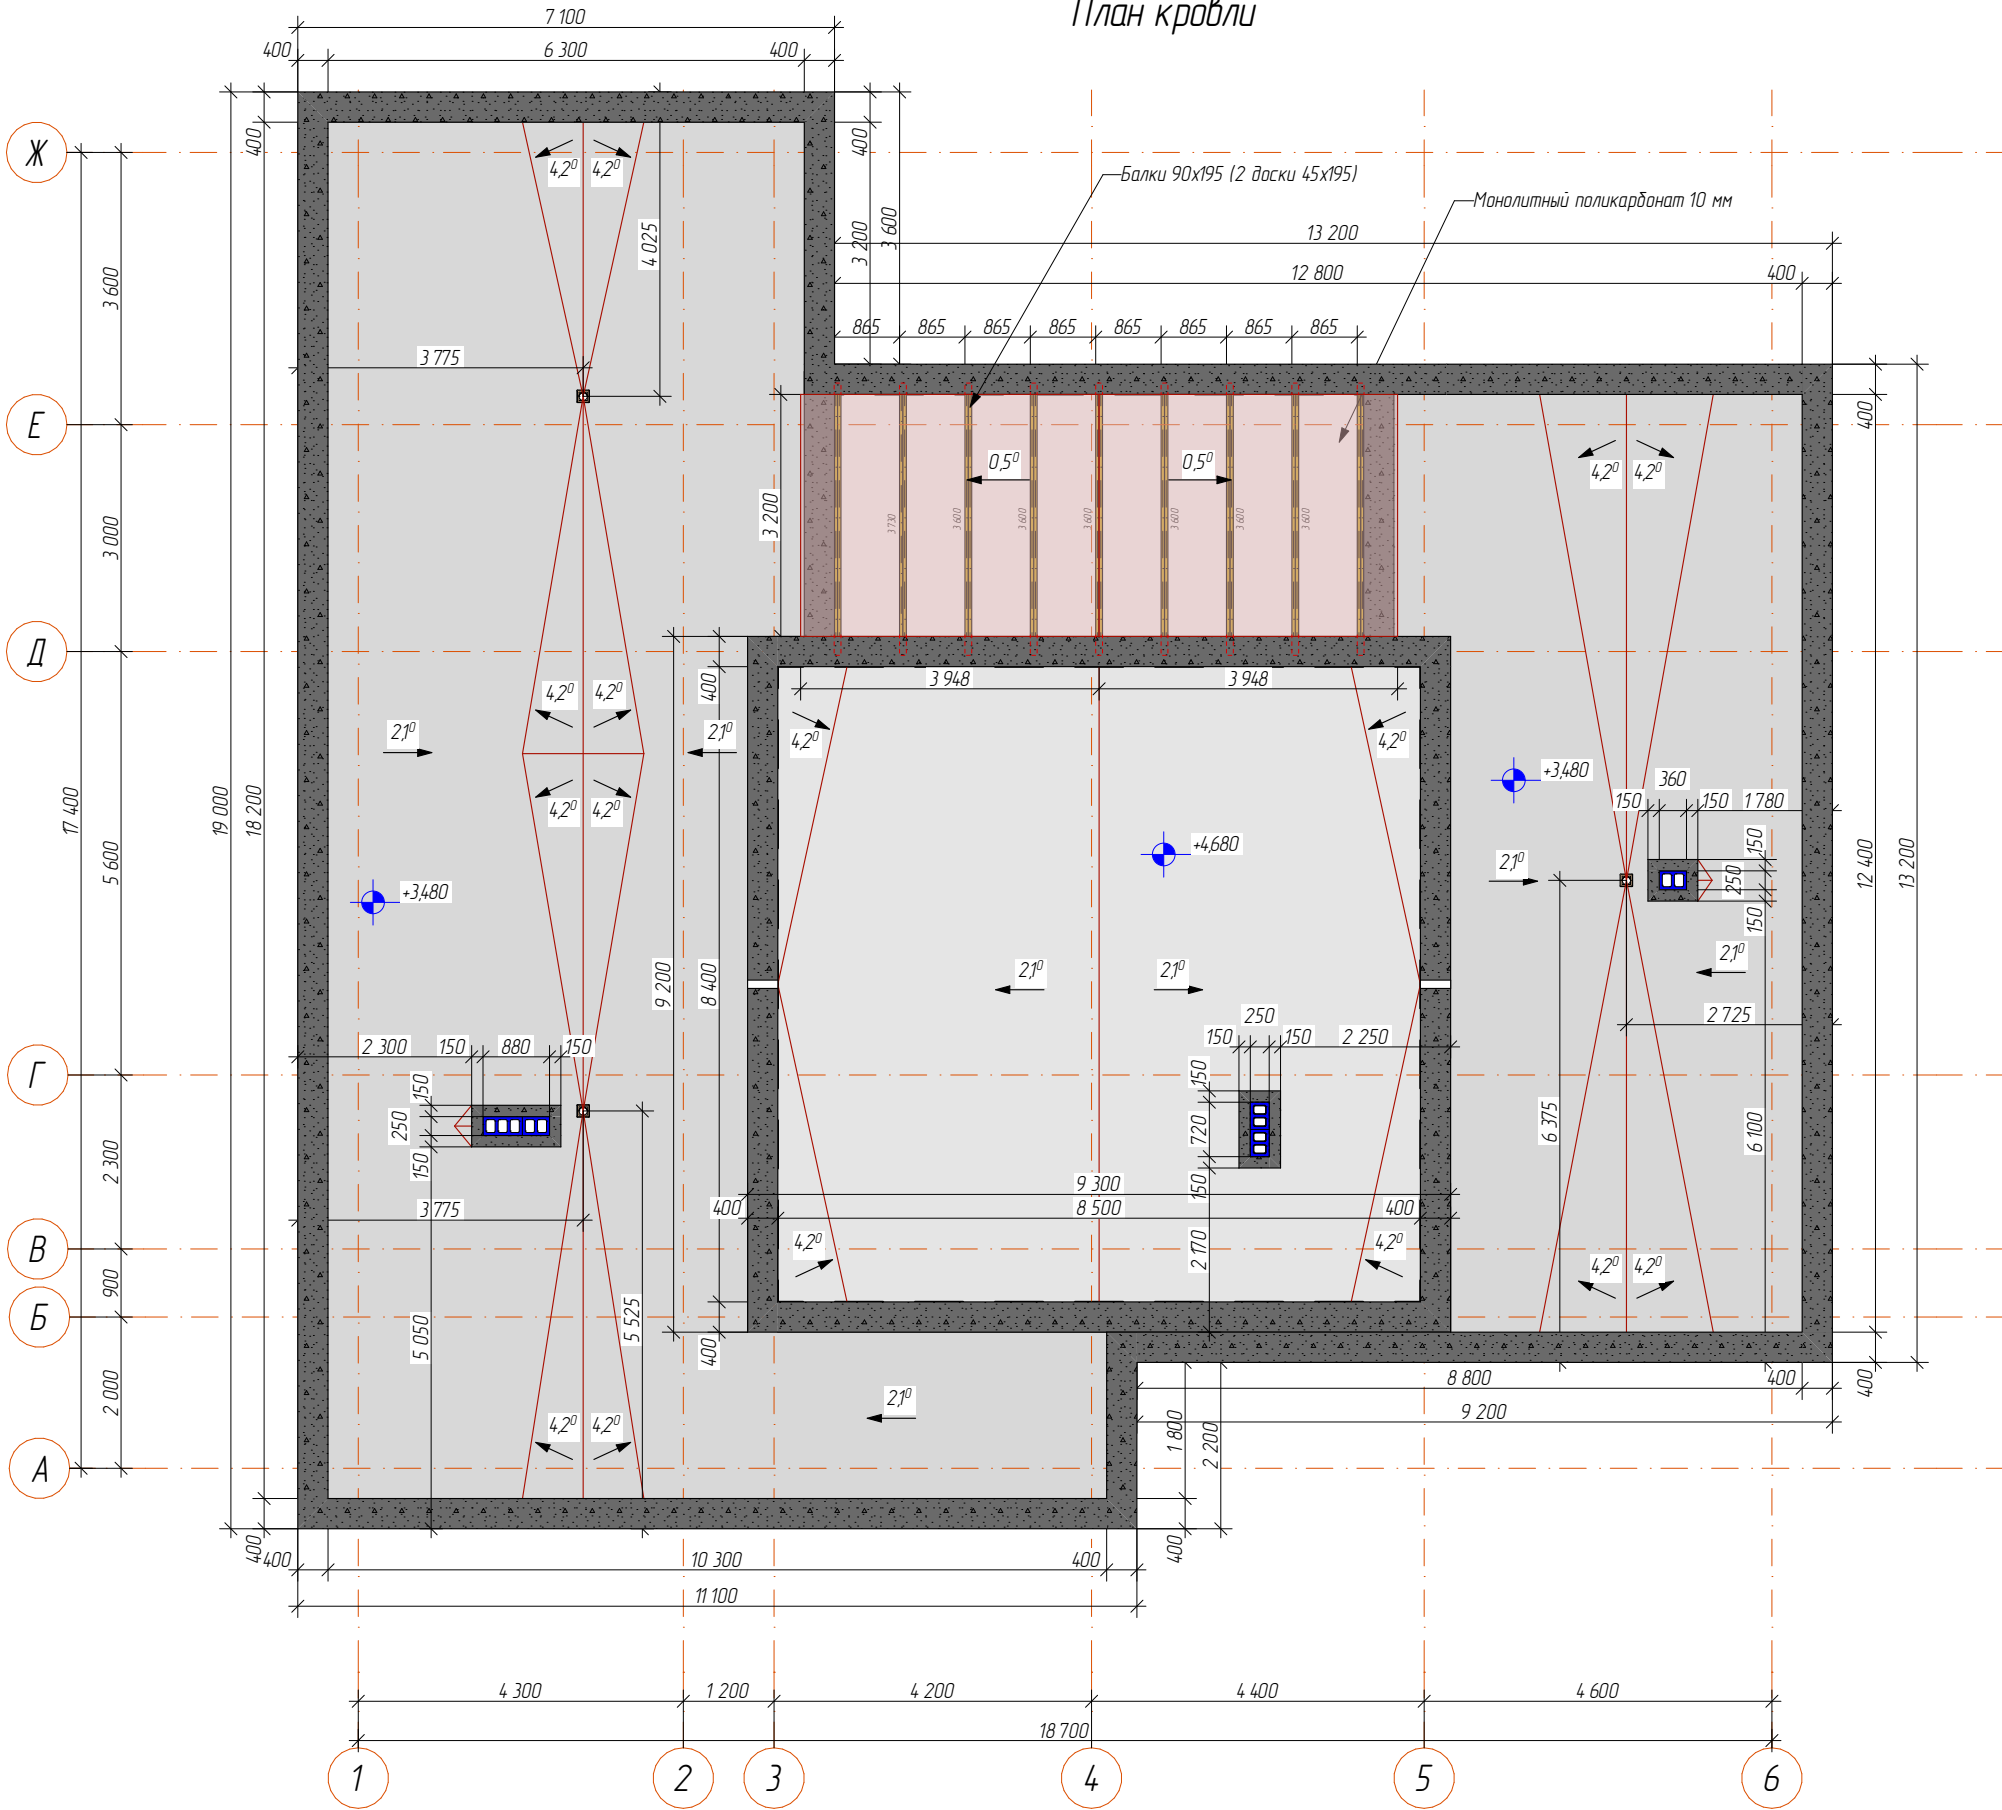

Примечание:

Организовать систему антиоблиedenия водоприемных воронок. Материалы по кровле допускается заменять аналогами со схожими характеристиками

						Проект жилого дома		
Изм.	Кол. уч.	Лист	№ док.	Подпись	Дата			
ГЛП		Филатов А.Г.		11.06.2026		Индивидуальный жилой дом по адресу «Российская федерация, Московская область, г. а. Домодедово, п. Государственного племенного завода "Константиново", тер. КП "Юсупово Виллаж" участок с кат. номером 50:28:0050421:2962»		
Разработал						Стандия	Лист	Листов
						Р	28	
						 Brick House строительство домов под ключ		
						План кровли		

Спецификация к плану кровли

Спецификация кровли 2-го этажа

Поз.	Обозначение	Наименование	Кол-во	Масса ед. шт.	Примечание
	ТУ 5774-008-17925162-2022	Пароизоляционный слой Биполь ЭПП	294		м²
	ГОСТ 32310-2012	ЭППС ТехноНИКОЛЬ CARBON PROF	58,8		м³
	ТУ 5952-001-13344965-2004	Стеклохолст ТЕХНОНИКОЛЬ 100 г/м²	294		кг
	ГОСТ 32310-2012	Разуклонка из клиновидных плит XPS ТехноНИКОЛЬ CARBON PROF SLOPE	Уточнить у монтажной организации		
		Полимерная мембрана LOGICROOF V-RP	398,4		
		Комплект листоуловитель с воранкой внутреннего водостока	3		шт
		Парапетная воранка	2		шт
		Доска 45х195(6м)	18		шт
		Монолитный поликарбонат 10 мм	25,28		м²
		Длина примыкания к парапетам	103,35		
		Длина примыкания к стенам	24,65		м/п
		Площадь кровли на отм. +3,480	212,35		м²
		Площадь кровли на отм. +4, 680	82		м²

Согласовано

Взам. инв. №

Подпись и дата

Инв. № подл.

Изм.

Кол. уч.

Лист

№ док.

Подпись

Дата

Г.А.П.

Филатов А.Г.

11.06.2026

Разработал

Проект жилого дома

Индивидуальный жилой дом по адресу:
«Российская федерация, Московская область,
г. о. Домодедово, п. Государственного племенного завода
"Константиново", тер. КП "Юсупово Вилладж"
участок с када. номером 50:28:0050421:2962»

Стадия

Лист

Листов

Р

29

Спецификация к плану кровли


Brick House

строительство домов под ключ

Формат А3

Узлы кровли

Примыкание к парапету

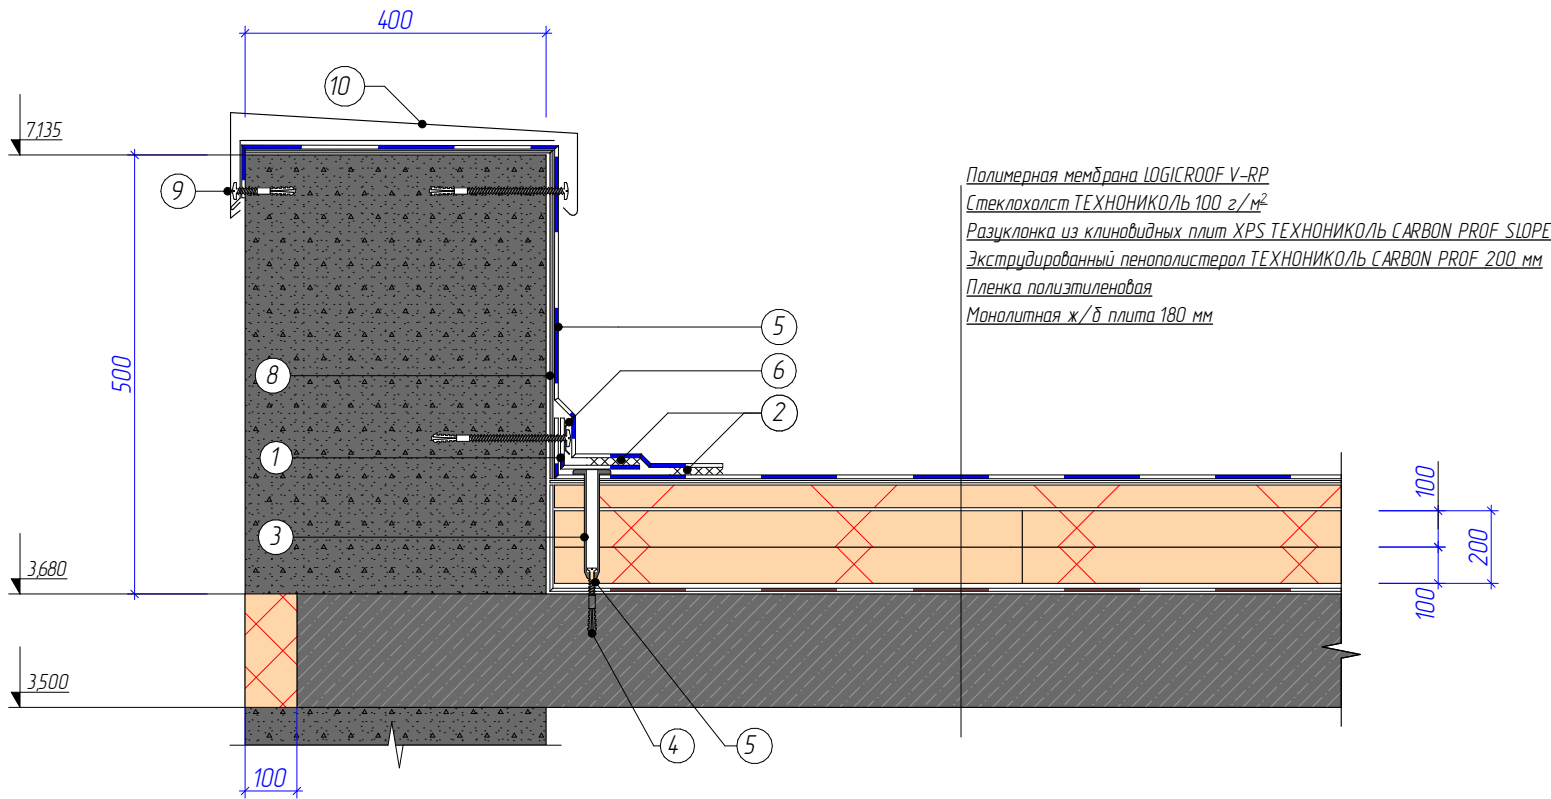

Полимерная мембрана LOGICROOF V-RP
Стеклохолст ТЕХНОНИКОЛЬ 100 г/м²
Разуклонка из клиновидных плит XPS ТЕХНОНИКОЛЬ CARBON PROF SLOPE
Экструдированный пенополистерол ТЕХНОНИКОЛЬ CARBON PROF 200 мм
Пленка полиэтиленовая
Монолитная ж/б плита 180 мм

- 1

Армированная полимерная мембрана шириной 130 мм
- 2

Сварной шов 30 мм
- 3

Телескопический крепежный элемент
ТЕХНОНИКОЛЬ*
- 4

Прижимная рейка ТЕХНОНИКОЛЬ
- 5

Армированная полимерная мембрана
ТЕХНОНИКОЛЬ по проекту
- 6

Геотекстиль излопробивной термо-
обработанный ТЕХНОНИКОЛЬ 300 г/квм
- 7

Ж/б основание, оштукатуренное
цп. раствором М200 по металлической
сетке, зафиксированной саморезами
- 8

Отлив из оцинкованной стали
- 9

Крепежный элемент
- 10

Металлический отлив с ПВХ-покрытием
- 11

Жидкий ПВХ
- 12

Крепежный элемент
- 13


Полиамидная анкерная гильза
длиной 45 или 60 мм
- 14

Остроконечный саморез по бетону
ТЕХНОНИКОЛЬ Ø 4,8 мм

ПРИМЕЧАНИЯ

* вместо телескопического крепежного элемента возможна установка стальной прижимной рейки и телескопического крепежа для индукции, см. лист 31

Водоприемная воронка

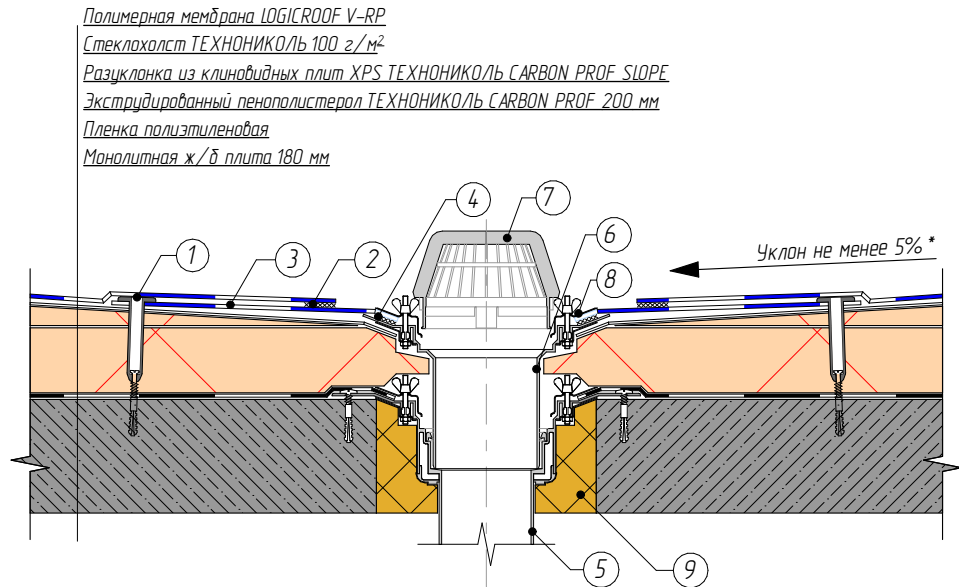

Полимерная мембрана LOGICROOF V-RP
Стеклохолст ТЕХНОНИКОЛЬ 100 г/м²
Разуклонка из клиновидных плит XPS ТЕХНОНИКОЛЬ CARBON PROF SLOPE
Экструдированный пенополистерол ТЕХНОНИКОЛЬ CARBON PROF 200 мм
Пленка полиэтиленовая
Монолитная ж/б плита 180 мм

- 1

Телескопический крепежный элемент ТЕХНОНИКОЛЬ
- 2

Сварной шов 30 мм
- 3

Фартук 1000x1000 мм из полимерной мембраны ТЕХНОНИКОЛЬ по проекту
- 4

Герметик ТЕХНОНИКОЛЬ ПУ
- 5

Водоприемная воронка ТЕХНОНИКОЛЬ
- 6

Надставной элемент
- 7

Листовоуловитель
- 8

Обжимной фланец
- 9

Пена монтажная ТЕХНОНИКОЛЬ

ПРИМЕЧАНИЯ

* Предусмотреть увеличение уклона к воронке до 5% в радиусе не менее 500 мм вокруг нее. Рекомендуется предусматривать заглубление воронки на 20–30 мм относительно уровня кровли.

Согласовано

Взам. инв. №


Подпись и дата

Инв. № подл.

Примечание:
Организовать систему антиобледенения водоприемных воронок. Материалы по кровле допускается заменять аналогами со схожими характеристиками

						Проект жилого дома			
Изм.	Кол.уч.	Лист	№док.	Подпись	Дата	Индивидуальный жилой дом по адресу: «Российская федерация, Московская область, г. о. Домодедово, п. Государственного племенного завода "Константиново", тер. КП "Юсупово Вилладж" участок с кад. номером 50:28:0050421:2962»	Стадия	Лист	Листов
ГАП		Филатов А.Г.			10.06.2026		Р	30	
Разработал									
						Узлы кровли	Brick House строительство домов под ключ		

Узлы кровли (продолжение)



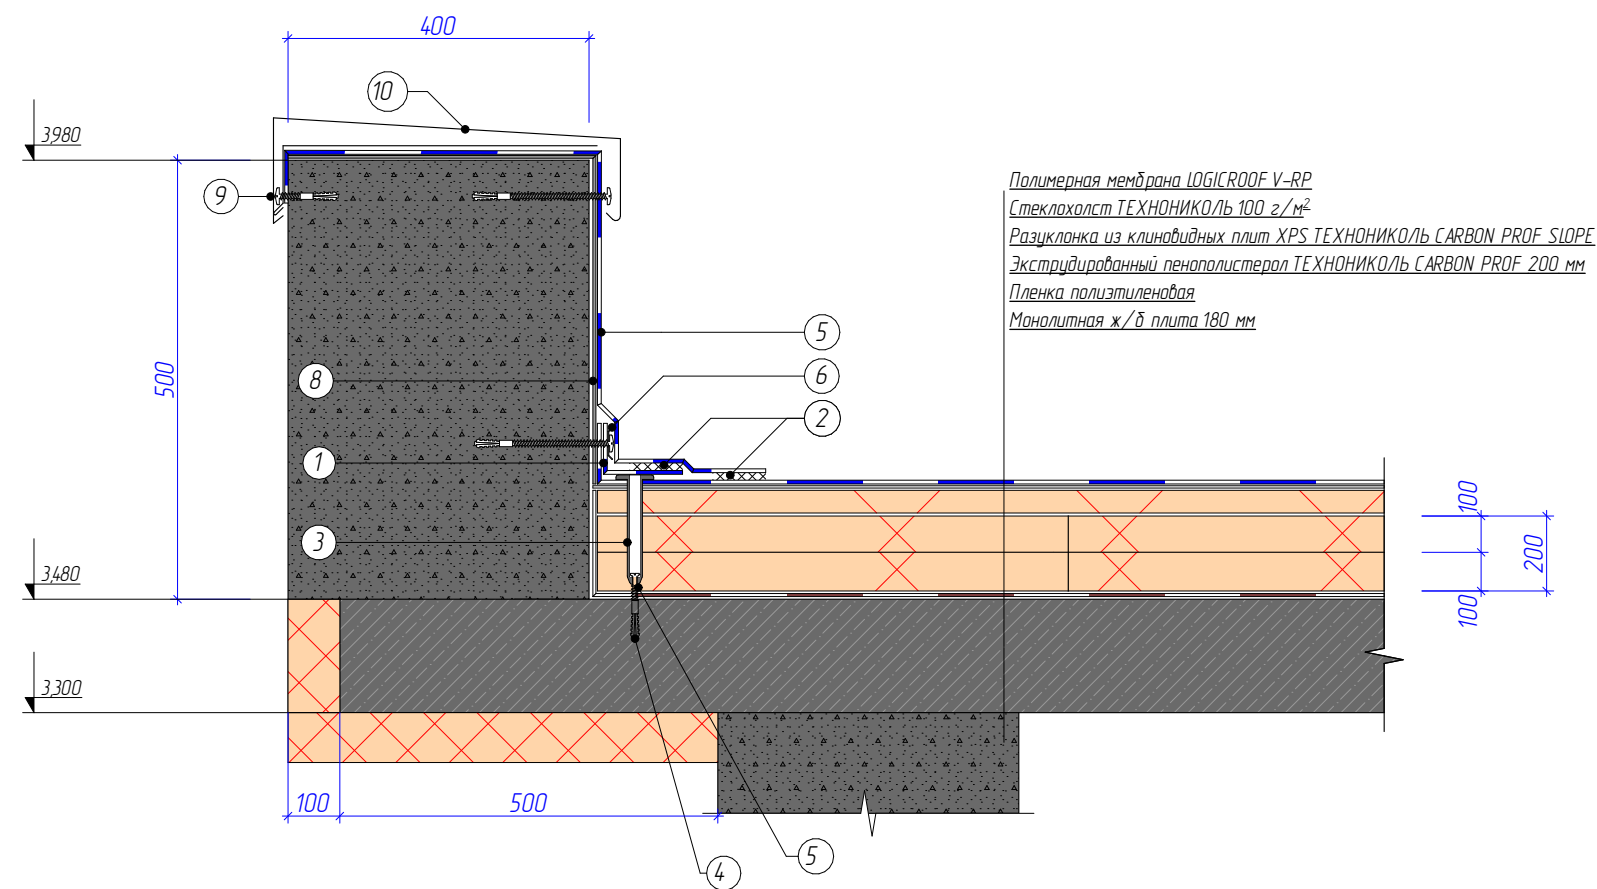


- | | | | |
|---|--|----|---|
| 1 | Армированная полимерная мембрана шириной 130 мм | 8 | Отлив из оцинкованной стали |
| 2 | Сварной шов 30 мм | 9 | Крепежный элемент |
| 3 | Телескопический крепежный элемент
ТЕХНОНИКОЛЬ* | 10 | Металлический отлив с ПВХ-покрытием |
| 4 | Прижимная рейка ТЕХНОНИКОЛЬ | 11 | Жидкий ПВХ |
| 5 | Армированная полимерная мембрана
ТЕХНОНИКОЛЬ по проекту | 12 | Крепежный элемент |
| 6 | Геотекстиль излопробивной термо-
обработанный ТЕХНОНИКОЛЬ 300 г/квм | 13 | Полиамидная анкерная гильза
длиной 45 или 60 мм |
| | | 14 | Остроконечный саморез по бетону
ТЕХНОНИКОЛЬ Ø 4,8 мм |

Согласовано				
Взам. инв. №				
Подпись и дата				
Инв. № подл.				

						Проект жилого дома					
Изм.	Кол. уч.	Лист	№ док.	Подпись	Дата	Индивидуальный жилой дом по адресу: «Российская федерация, Московская область, г. о. Домодедово, п. Государственного племенного завода "Константиново", тер. КП "Юсупово Вилладж" участок с кад. номером 50:28:0050421:2962»			Стадия	Лист	Листов
ГАП	Филатов А.Г.				10.06.2026				Р	31	
Разработал											
						Узлы кровли (продолжение)			 Brick House строительство домов под ключ		

Разрез по вентканалам

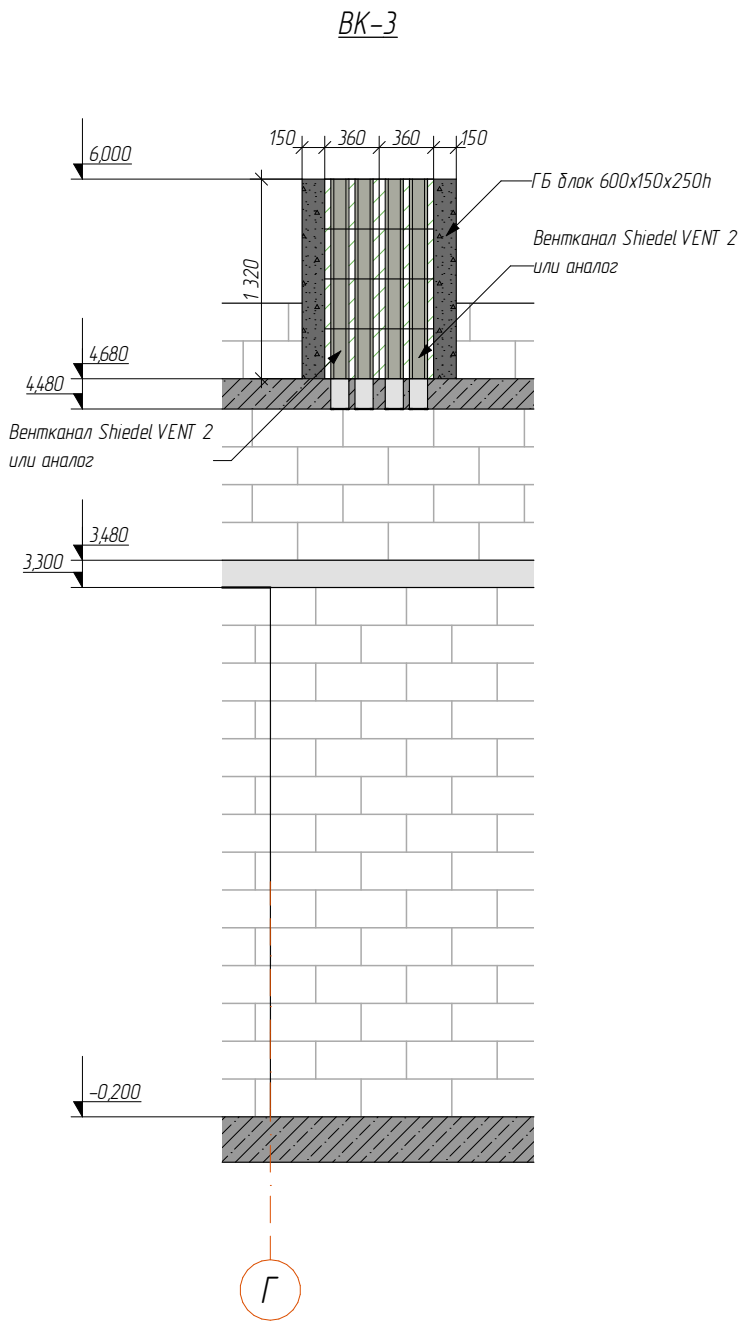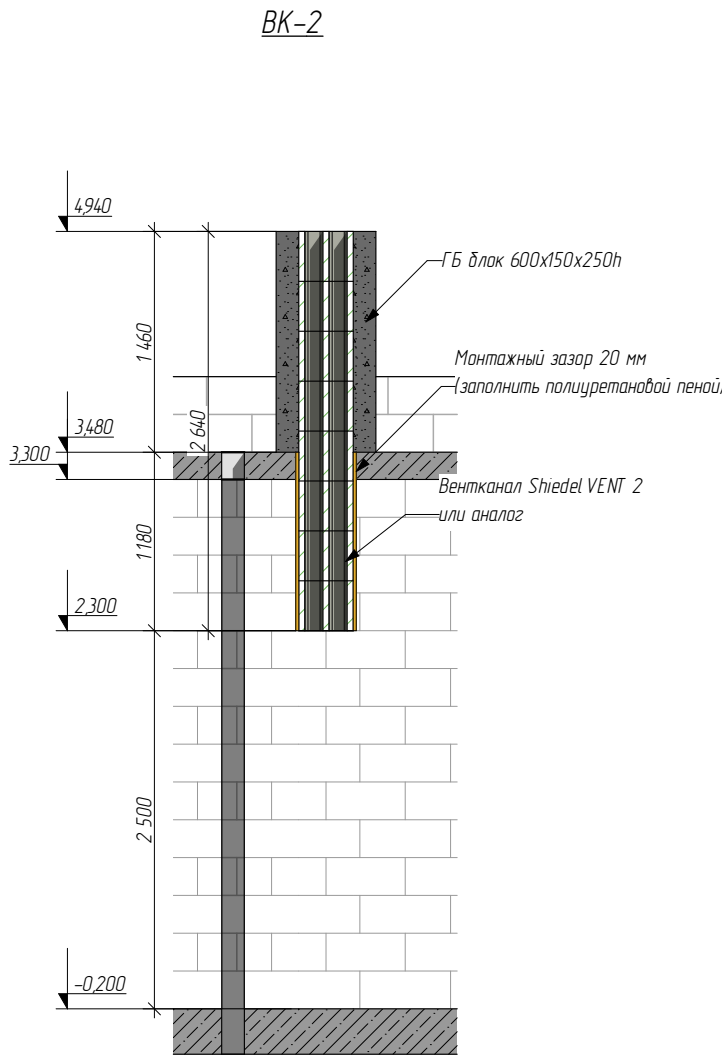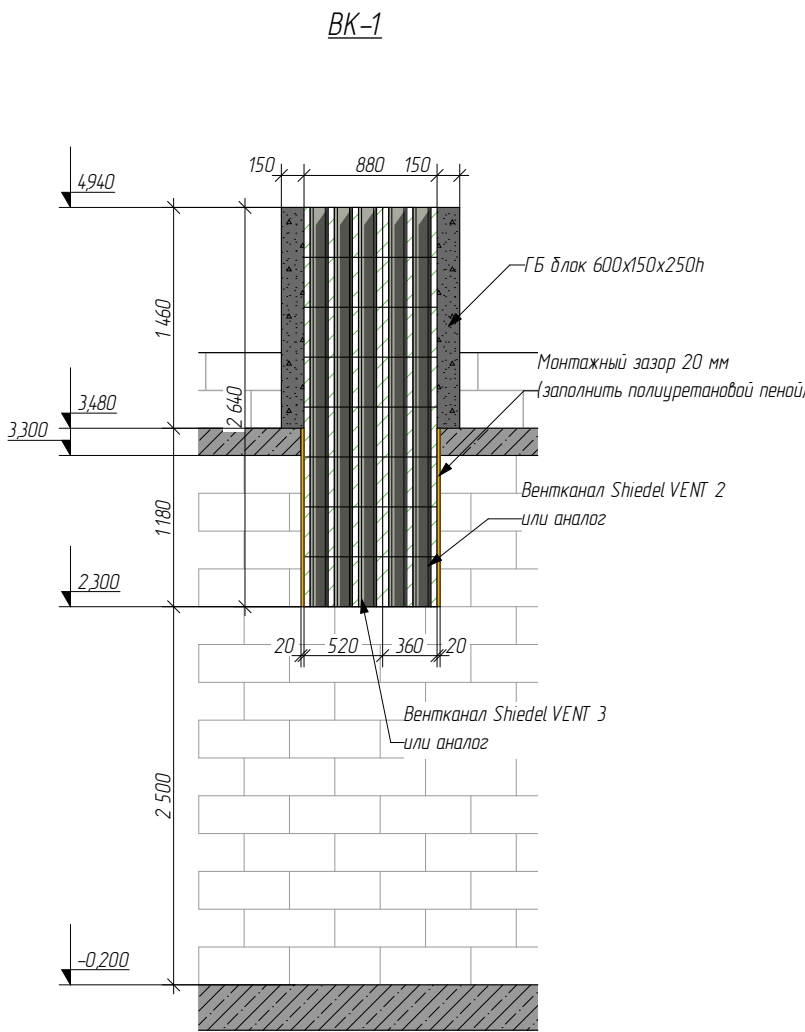

Спецификация вентиляционных каналов

Поз	Обозначение	Наименование	Кол-во	Масса ед. шт.	Примечание
		Вентиляционный канал Shiedel VENT 2 (360x250 мм)	24		шт
		Вентиляционный канал Shiedel VENT 3 (520x250 мм)	8		шт
		Газобетонный блок 600x150x250 (обкладка вентканалов)	172		м³
		Общая длина кладки	652		м/п

Изм.	Кол. уч.	Лист	№ док.	Подпись	Дата	Проект жилого дома		
ГАП	Филатов А.Г.				10.06.2026	Индивидуальный жилой дом по адресу: «Российская федерация, Московская область, г.о. Домодедово, п. Государственного племенного завода "Константиново", тер. КП "Осупово Вилладж" участок с кадастровым номером 50:28:0050421:2962»		
Разработал						Стадия		
						Р		
						Лист		
						32		
						Листов		
						Формат А3		