



*Индивидуальный жилой дом по адресу:
«Российская федерация, Московская область,
г. о. Домодедово, п. Государственного племенного завода
"Константиново", тер. КП "Юсупово Вилладж"
участок с кад. номером 50:28:0050421:2962»*

КР-1. Конструкции ниже отметки 0,000

ГАП _____ Филатов А. Г.

город Москва, 2026 г.

Ведомость чертежей

Лист	Наименование	Примечание
1	Обложка	
2	Ведомость чертежей	
3	Пояснительная записка	
4	Схема планировочной организации земельного участка	
5	План разбивки осей	
6	Основное сечение по фундаменту	
7	Схема коммуникаций	
8	План котлована	
9	План фундаментной плиты	
10	Спецификация к плану фундаментной плиты	
11	План термовставок	
12	Узлы фундаментной плиты	
13	Общий вид фундамента	

Согласовано			
Взам. инв. №			
Подпись и дата			
Инв. № подл.			

						Проект жилого дома				
Изм.	Кол.уч.	Лист	№ док.	Подпись	Дата					
ГАП		Филатов А.Г.			11.06.2026	Индивидуальный жилой дом по адресу: «Российская федерация, Московская область, г. о. Домодедово, п. Государственного племенного завода "Константиново", тер. КП "Юсупово Вилладж" участок с када. номером 50:28:0050421:2962»		Стадия	Лист	Листов
Разработал					Р			2		
						Ведомость чертежей		 Brick House строительство домов под ключ		

ОБЩИЕ ДАННЕ:

1. Проект выполнен согласно Эскизному проекту, техническому заданию Заказчика и действующих строительных норм и правил.
2. Проектом предусмотрено строительство фундамента для Индивидуального жилого дома по адресу
Индивидуальный жилой дом по адресу: «Российская федерация, Московская область, г. о. Ступино, д. Колычево.
участок с кад. номером 50:33:010325:1511»
3. За отм. + 0. 000 принята отметка чистого пола. Привязку здания по высотным отметкам на рельефе участка согласовать дополнительно.
4. Фундамент жилого дома плитный (монолитная плита локально усиленная 300 мм) из бетона В 22,5. W6 F150 П4.
– Армирование плиты фундамента выполнено из арм-ной сетки А500С (ГОСТ 34028–2016) ф12, в 2 уровня с шагом 200 мм,
– Вертикальное утепление фундамента выполнено из ЭППС 100 мм, с механическим креплением тарельчатыми дюбелями (ГОСТ Р 58359–2019)
– Вертикальная гидроизоляция фундамента выплнена из битумной мастики в 2 слоя – выполнить по всем бетонным поверхностям соприкасающимися с грунтом, согласно проекта.
– Под ж/б плитой жилого дома запроектировано песчанное основание , В местах соприкосновения песчанного основания с грунтом выполнить устройство геотекстиля. Коэффициент уплотнения песчанного основания принять согласно СП 4513330.2017 Ксот. =0,95.
– Наружная контурная терраса – на вспомогательном фундаменте на винтовых сваях с балочным перекрытием.
5. Расход материалов дано проектное без учета производственных остатков, потерь, норм отпуска материалов.
6. Спецификации, представленные в проекте, не являются заявками на поставку материалов. Необходимо дополнительное составление заявок заказчиком или подрядной организацией.
7. Строительно-монтажные работы должны вестись строго в соответствии с требованиями:
– СП 2213330.2016 “Основания зданий и сооружений”
– СП 7013330.2012 “Несущие и ограждающие конструкции”
– СП 4513330.2017 “Земляные сооружения, основания и фундаменты”
– СП 6313330.2018 “Бетонные и железобетонные конструкции”
– СП 50-101-2004 “Проектирование и устройство оснований и фундаментов зданий и сооружений”
– СП 52-101-2003 “Бетонные и железобетонные конструкции без предварительного напряжения арматуры”
8. Перед началом работ выполнить проекты ИС (инженерные сети Водопровода и канализации, Отопления и вентиляции и пр.)
После разработки проектов ИС при необходимости согласовать с автором проекта места устройства сетей, отверстий, штроб и прочего.

Условные обозначения

№ п/п	наименование	сечение	поверхность	примечание
1	ЭППС			
2	Железобетон			
3	Газобетон			


АРМИРОВАНИЕ КОНСТРУКЦИЙ:

1. Армирование монолитных фундаментов из отдельных стержней исходя из максимальной длины стержня.
Марка арматурной стали:
– А240 – ст3кп по ГОСТ 5781–82*
– А500С– 3ПС – ГОСТ 380–2005.
При необходимости стыковку стержней производить нахлесткой. Длина нахлестки стержней не менее 50d.
2. Арматура не должна иметь механических повреждений или пластических деформаций ухудшающих сцепление с бетоном, загрязнения и коррозионные поражения.
3. Все изготавливаемые арматурные изделия должны отвечать требованиям ГОСТ 10922–2012 и ГОСТ 14098–91.
4. Все сопряжения арматуры выполнять вязальной проволокой 1,2 – 0 – 4 по ГОСТ 3282–74 с шагом через 2 стержня в шахматном порядке.
5. Минимальный защитный слой бетона принять 25 мм.

Согласовано			
Взам. инв. №			
Подпись и дата			
Инв. № подл.			

						Проект жилого дома					
Изм.	Кол.уч.	Лист	№ док.	Подпись	Дата						
ГАП		Филатов А.Г.			10.06.2026	Индивидуальный жилой дом по адресу: «Российская федерация, Московская область, г. о. Домодедово, п. Государственного племенного завода "Константиново", тер. КП "Юсупово Вилейж" участок с кад. номером 50:28:0050421:2962»		Стадия	Лист	Листов	
Разработал								Р	3		
								 Brick House строительство домов под ключ			
						Пояснительная записка					


Схема планировочной организации земельного участка

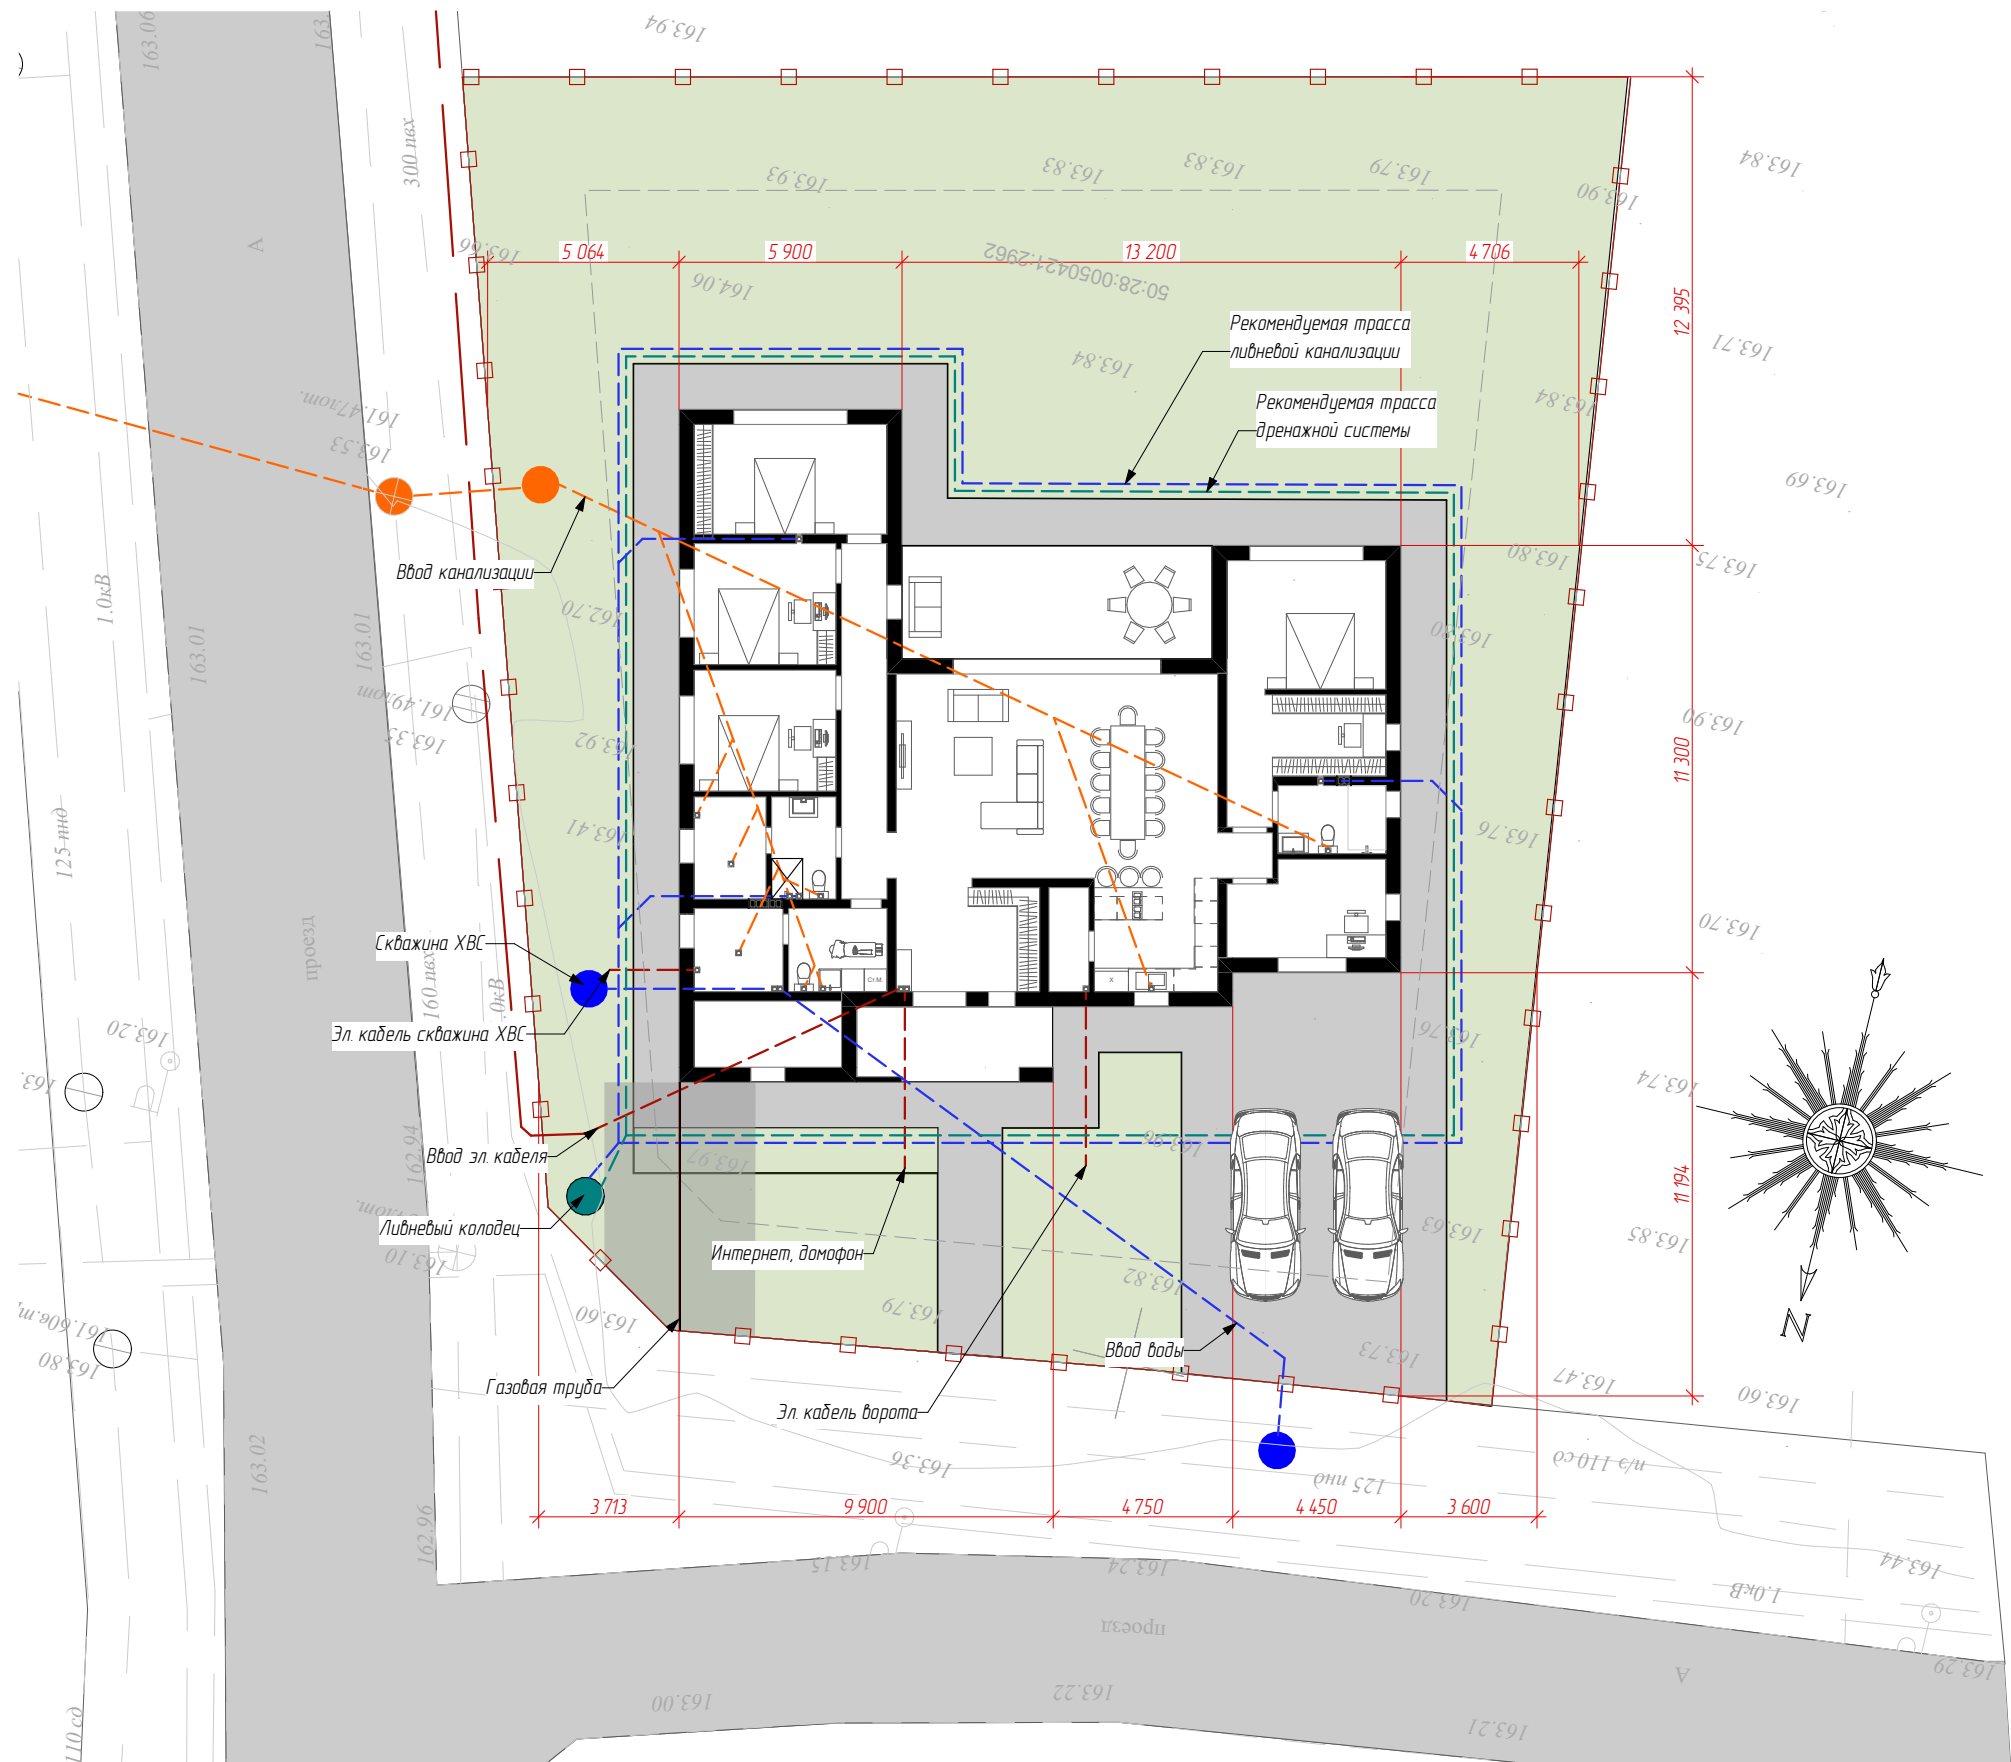

Согласовано					
Инв. № подл.	Взам. инв. №		Подпись и дата		

						Проект жилого дома			
Изм.	Кол.уч.	Лист	№ док.	Подпись	Дата	Индивидуальный жилой дом по адресу: «Российская федерация, Московская область, г. о. Домодедово, п. Государственного племенного завода "Константиново", тер. КП "Юсупово Вилладж" участок с кад. номером 50:28:0050421:2962»	Стадия	Лист	Листов
ГАП	Филатов А.Г.				10.06.2026		Р	4	
Разработал									
						Схема планировочной организации земельного участка	 Brick House строительство домов под ключ		


План разбивки осей

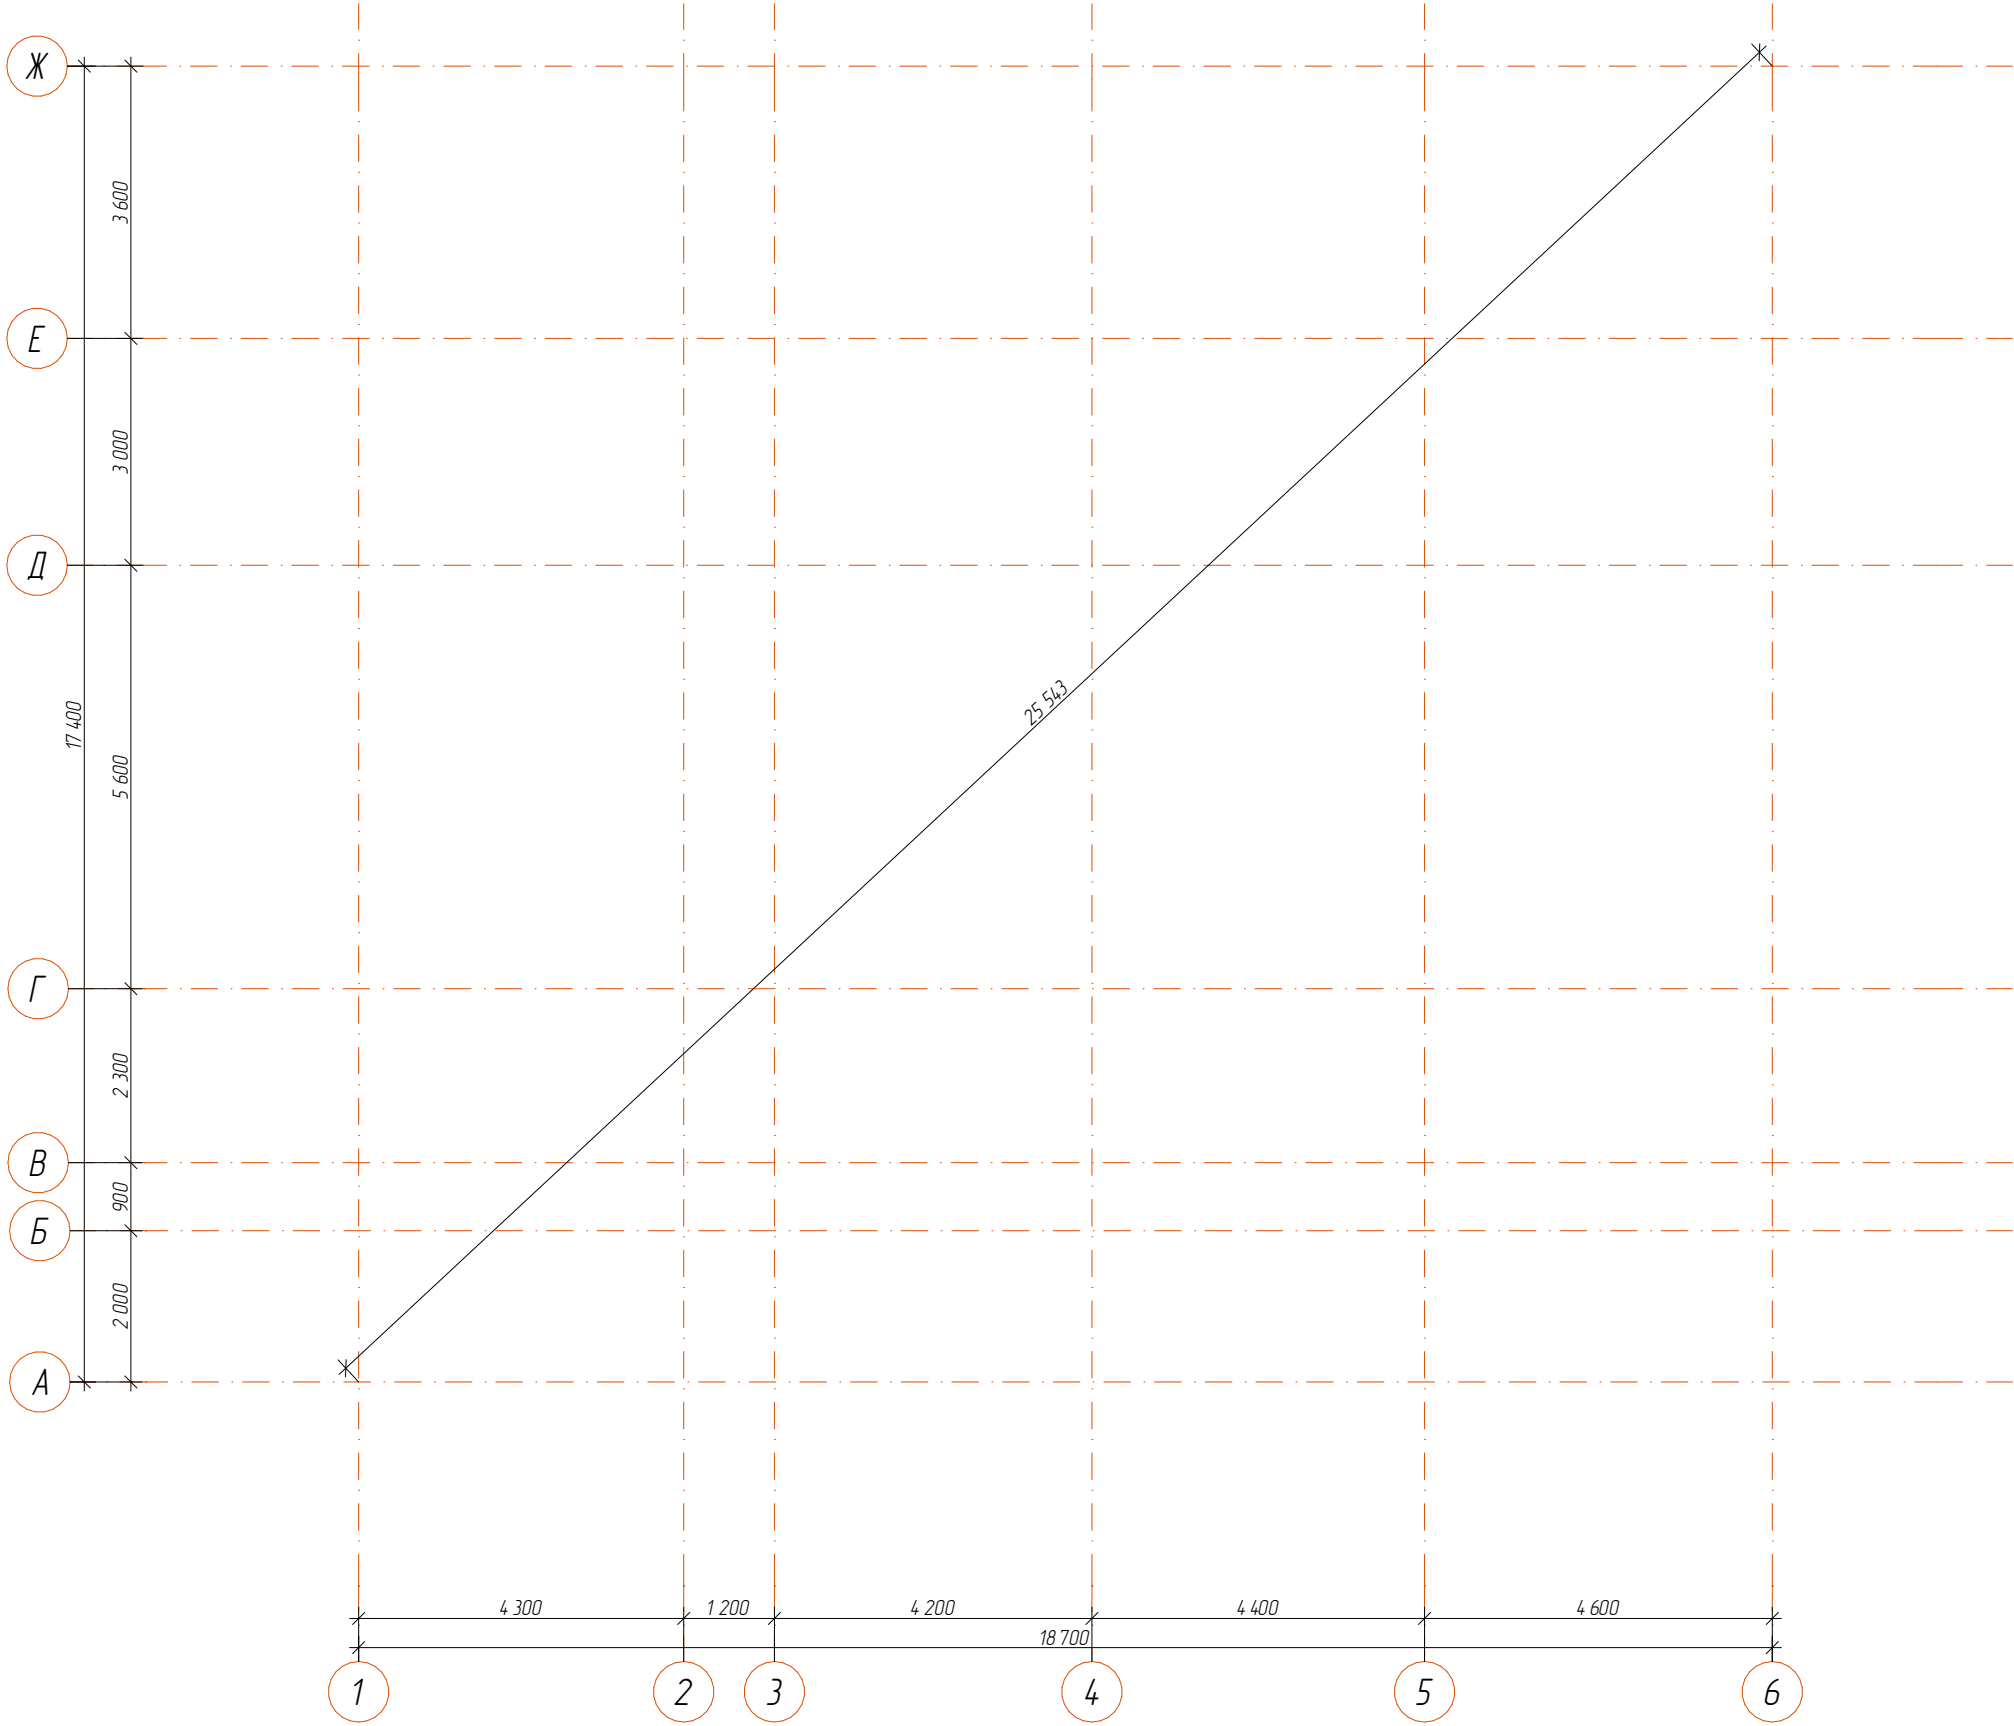

Согласовано			
Взам. инв. №			
Подпись и дата			
Инв. № подл.			

						Проект жилого дома			
Изм.	Кол.уч.	Лист	№ док.	Подпись	Дата	Индивидуальный жилой дом по адресу: «Российская федерация, Московская область, г. о. Домодедово, п. Государственного племенного завода "Константиново", тер. КП "Юсупово Вилладж" участок с кад. номером 50:28:0050421:2962»	Стадия	Лист	Листов
ГАП		Филатов А.Г.			10.06.2026		Р	5	
Разработал									
						План разбивки осей	 Brick House строительство домов под ключ		

Основное сечение по фундаменту

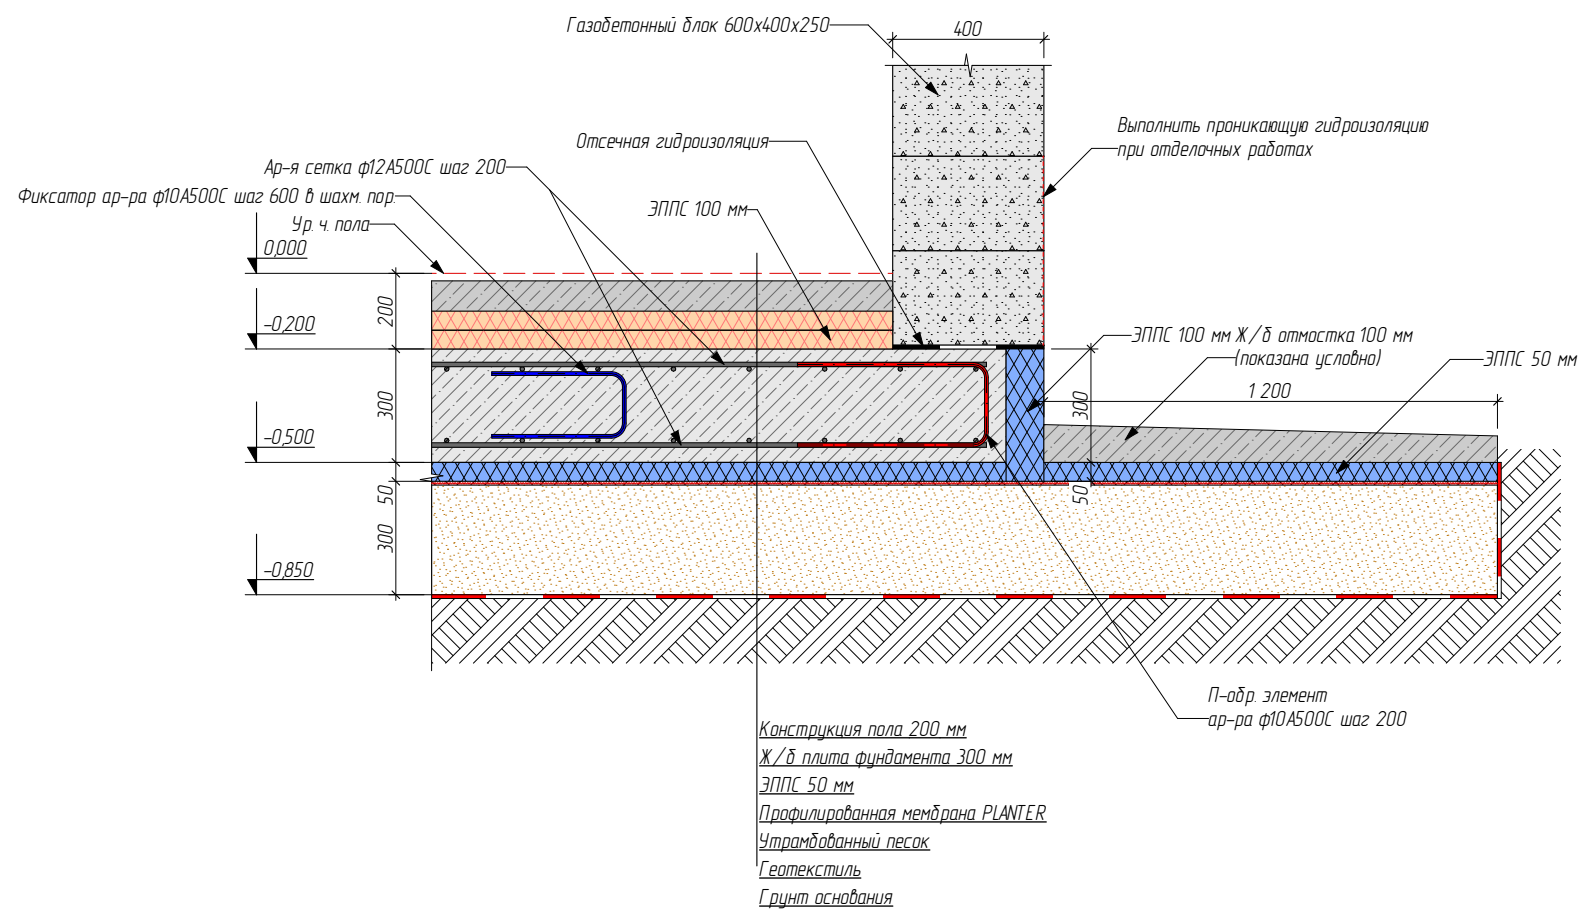

Согласовано

Взам. инв. №


Подпись и дата

Инв. № подл.

Проект жилого дома

Изм.	Кол. уч.	Лист	№ док.	Подпись	Дата	Индивидуальный жилой дом по адресу: «Российская федерация, Московская область, г. о. Домодедово, п. Государственного племенного завода "Константиново", тер. КП "Осупово Вилладж" участок с кадастровым номером 50:28:0050421:2962»		
Г.А.П.		Филатов А.Г.			11.06.2026			
Разработал						Основное сечение по фундаменту		
						Формат А3		


Схема коммунікацій

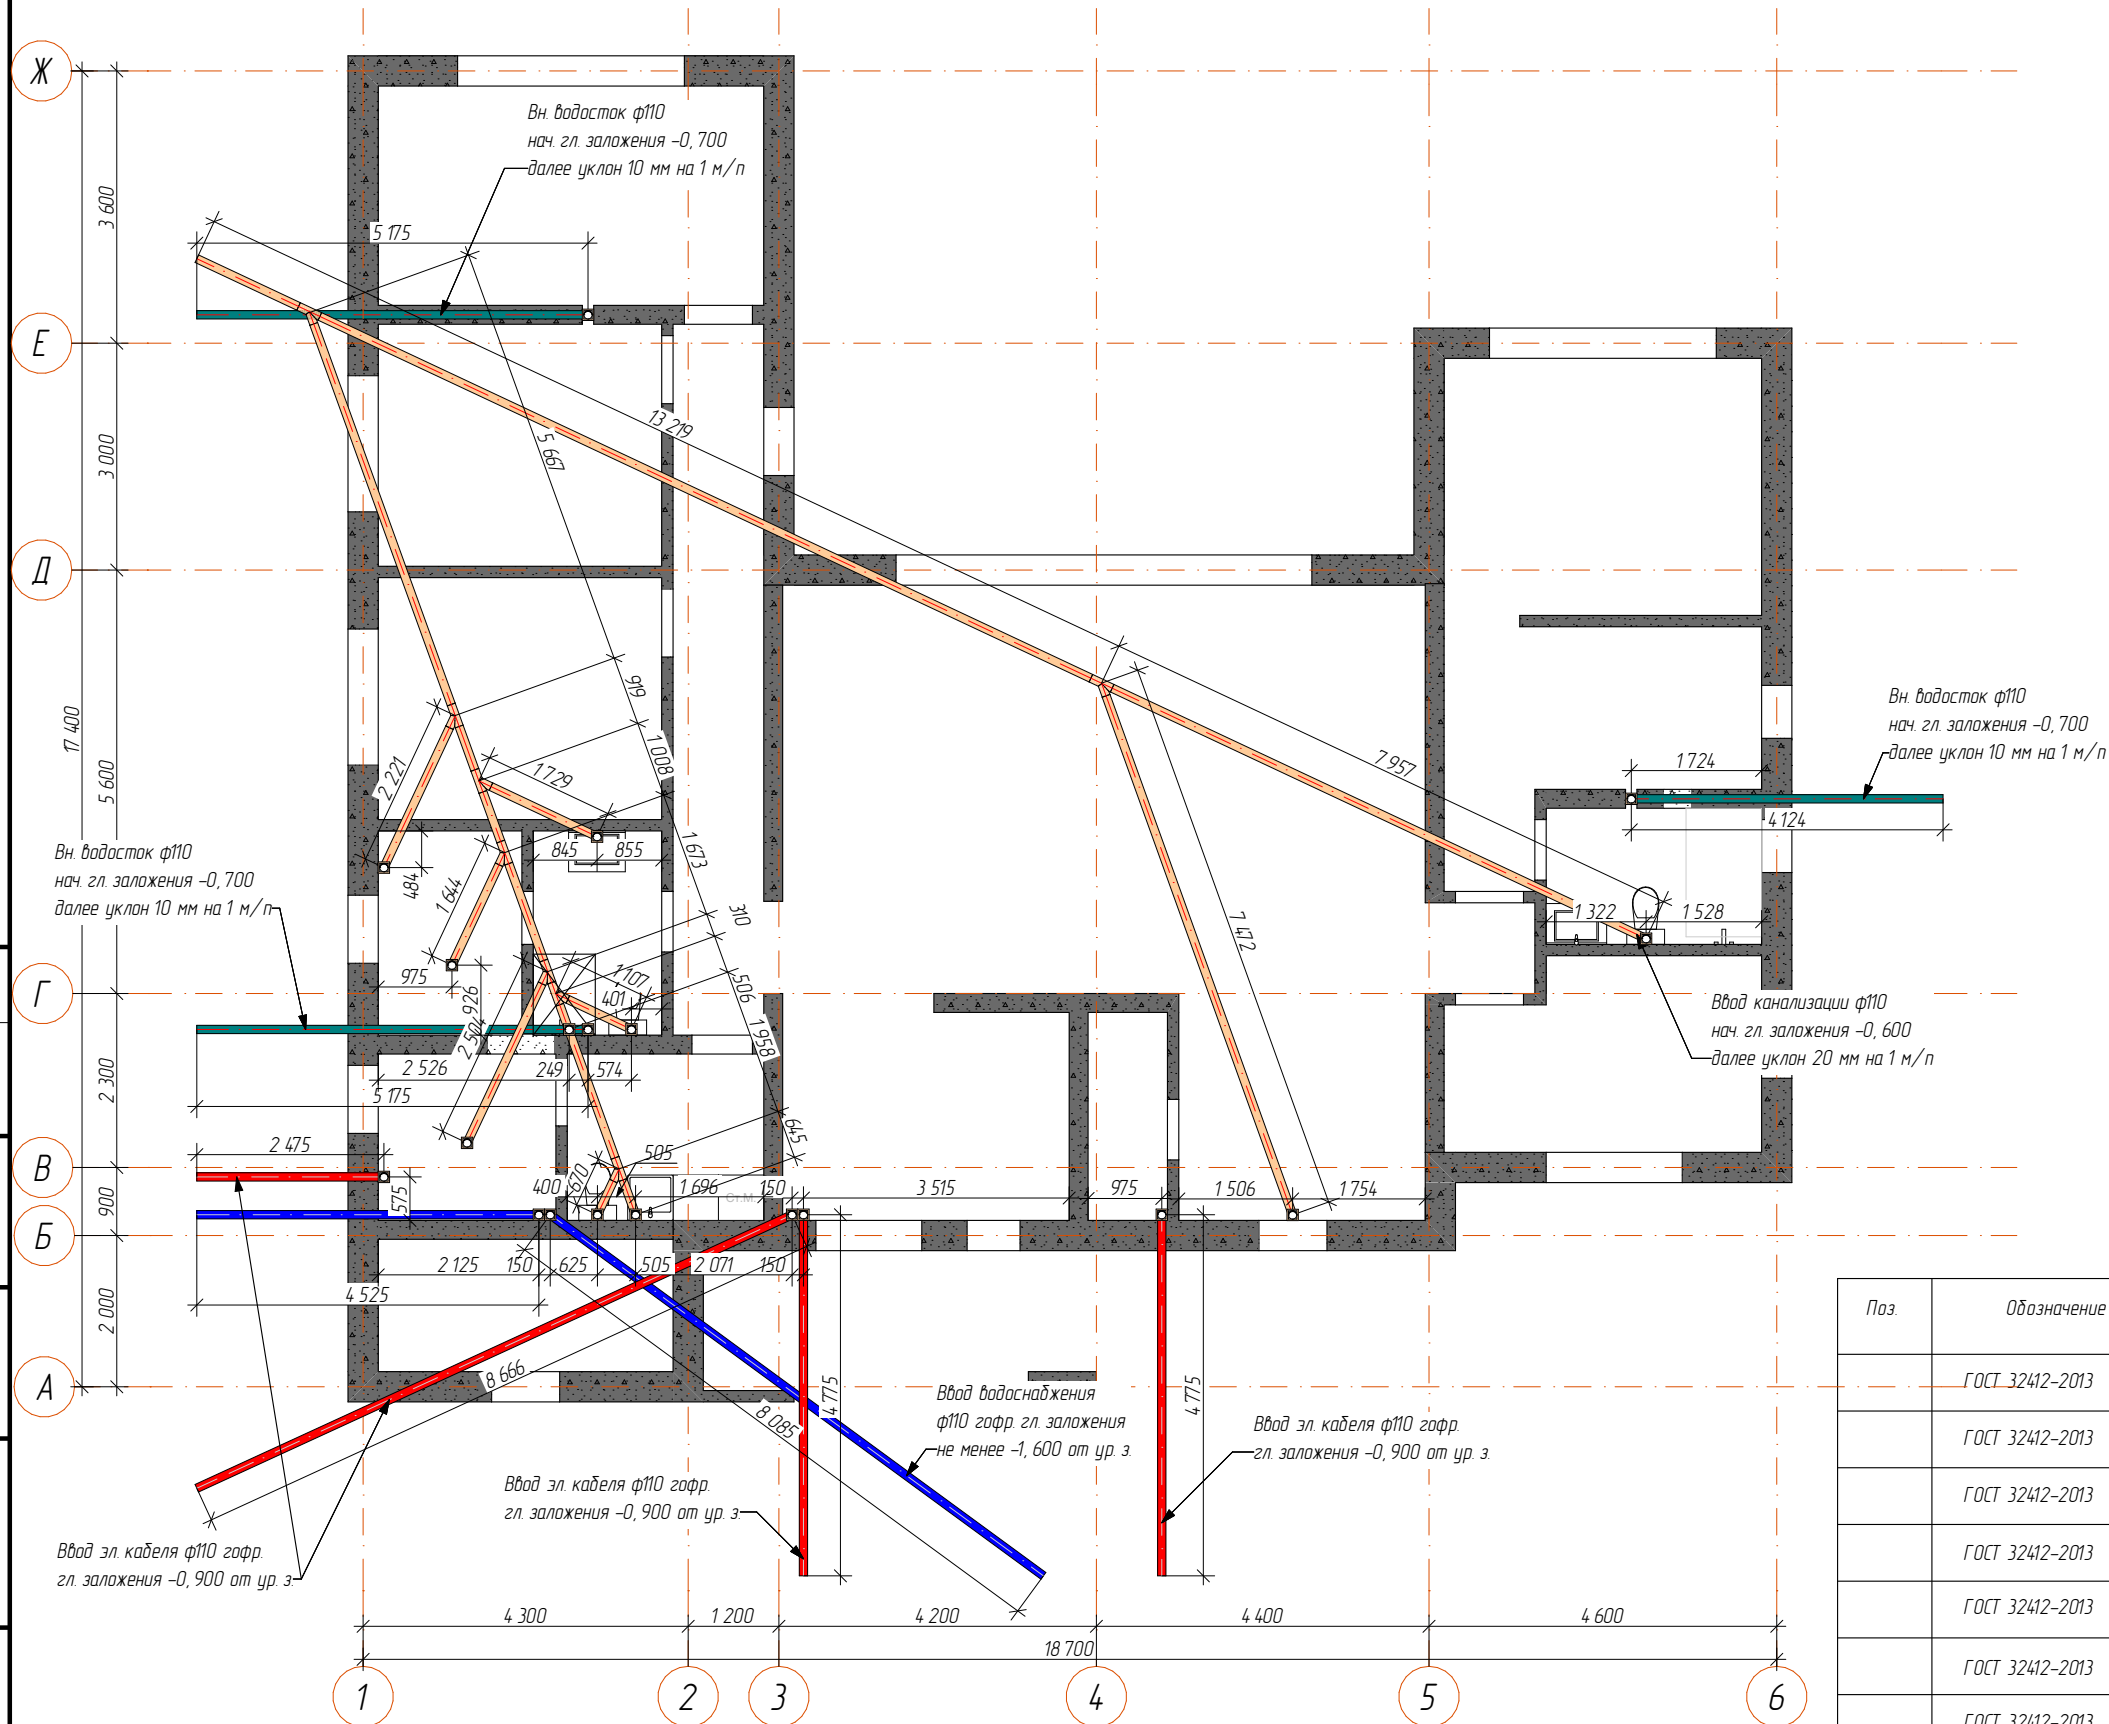

Поз	Обозначение	Наименование	Кол-во	Масса ед. шт.	Примечание
	ГОСТ 32412-2013	Труба 1 м. ф110 (рыжая)	12		шт
	ГОСТ 32412-2013	Труба 2 м. ф110 (рыжая)	7		шт
	ГОСТ 32412-2013	Труба 3 м. ф110 (рыжая)	18		шт
	ГОСТ 32412-2013	Тройник 45° ф110 (рыжий)	8		шт
	ГОСТ 32412-2013	Угол 45° ф110 (рыжий)	23		шт
	ГОСТ 32412-2013	Заглушка. ф110 (рыжий)	18		шт
	ГОСТ 32412-2013	Труба ф110 гофрированная	35		м/п

						Проект жилого дома			
Изм.	Кол. ун.	Лист	№ док.	Подпись	Дата				
ГАП		Филатов А. Г.			11.06.2026	Индивидуальный жилой дом по адресу: «Российская федерация, Московская область, г. о. Домодедово, п. Государственного племенного завода "Константиново", тер. КП "Юсупово Вилладж" участок с кад. номером 50:28.0050421:2962»			
Разработал									
Схема коммуникаций						Стадия	Лист	Листов	
						Р	7		
						 Brick House строительство домов под ключ			

План котлована

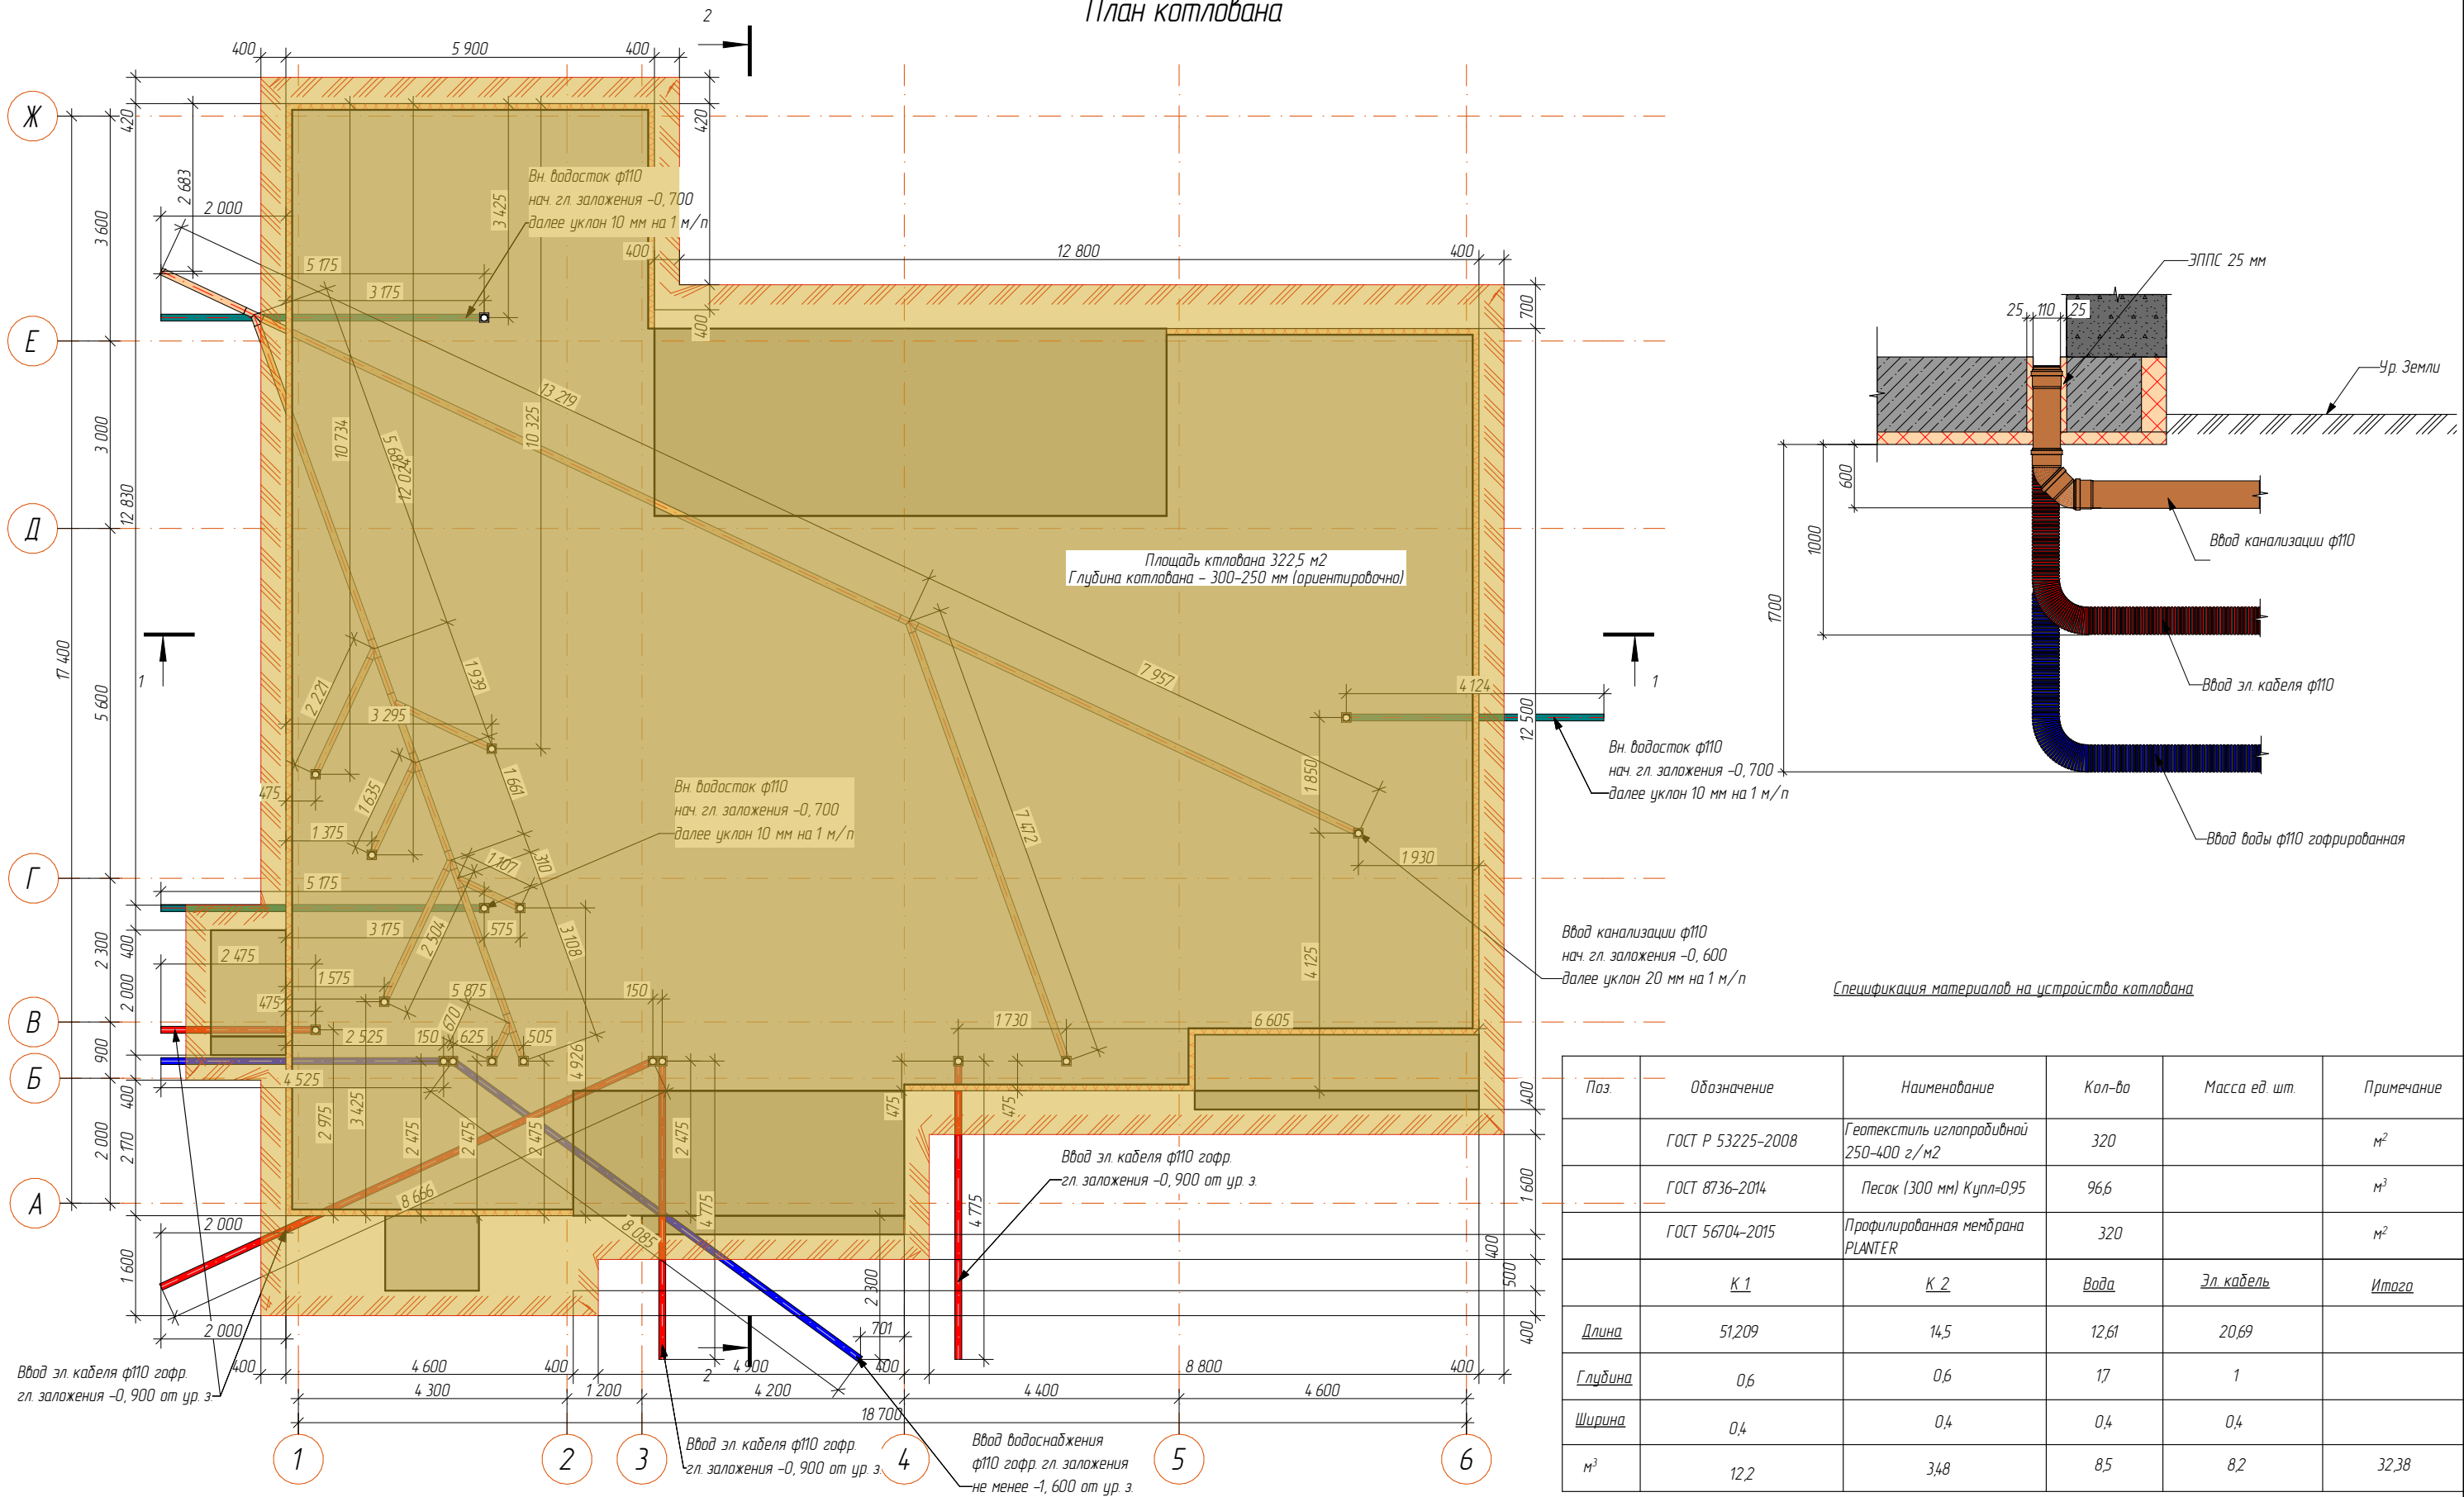

Спецификация материалов на устройство котлована


Поз.	Обозначение	Наименование	Кол-во	Масса ед. шт.	Примечание
	ГОСТ Р 53225-2008	Геотекстиль излопроливной 250-400 г/м2	320		м ²
	ГОСТ 8736-2014	Песок (300 мм) Купл=0,95	96,6		м ³
	ГОСТ 56704-2015	Профилированная мембрана PLANTER	320		м ²
	<u>К 1</u>	<u>К 2</u>	<u>Вода</u>	<u>Эл. кабель</u>	<u>Итого</u>
<u>Длина</u>	51209	14,5	12,61	20,69	
<u>Глубина</u>	0,6	0,6	17	1	
<u>Ширина</u>	0,4	0,4	0,4	0,4	
м ³	12,2	348	8,5	8,2	32,38

						Проект жилого дома		
Изм.	Кол. уч.	Лист	№ док.	Подпись	Дата			
ГАП		Филатов А.Г.		10.06.2026		Индивидуальный жилой дом по адресу «Российская федерация, Московская область, г. о. Домодедово, п. Государственного племенного завода "Константиново", тер. КП "Юсупово Вилладж" участок с кадастровым номером 50:28:0050421:2962»		
Разработал								
						Страница	Лист	Листов
						Р	8	
План котлована						 Brick House строительство домов под ключ		



Примечание:
1. Ширина откоса показана условно
2. При необходимости устройства песчанной подсыпки доработать вручную до проектной отметки.

Формат А3



Согласовано			
Взам. инв. №			
Подпись и дата			
Инв. № подл.			

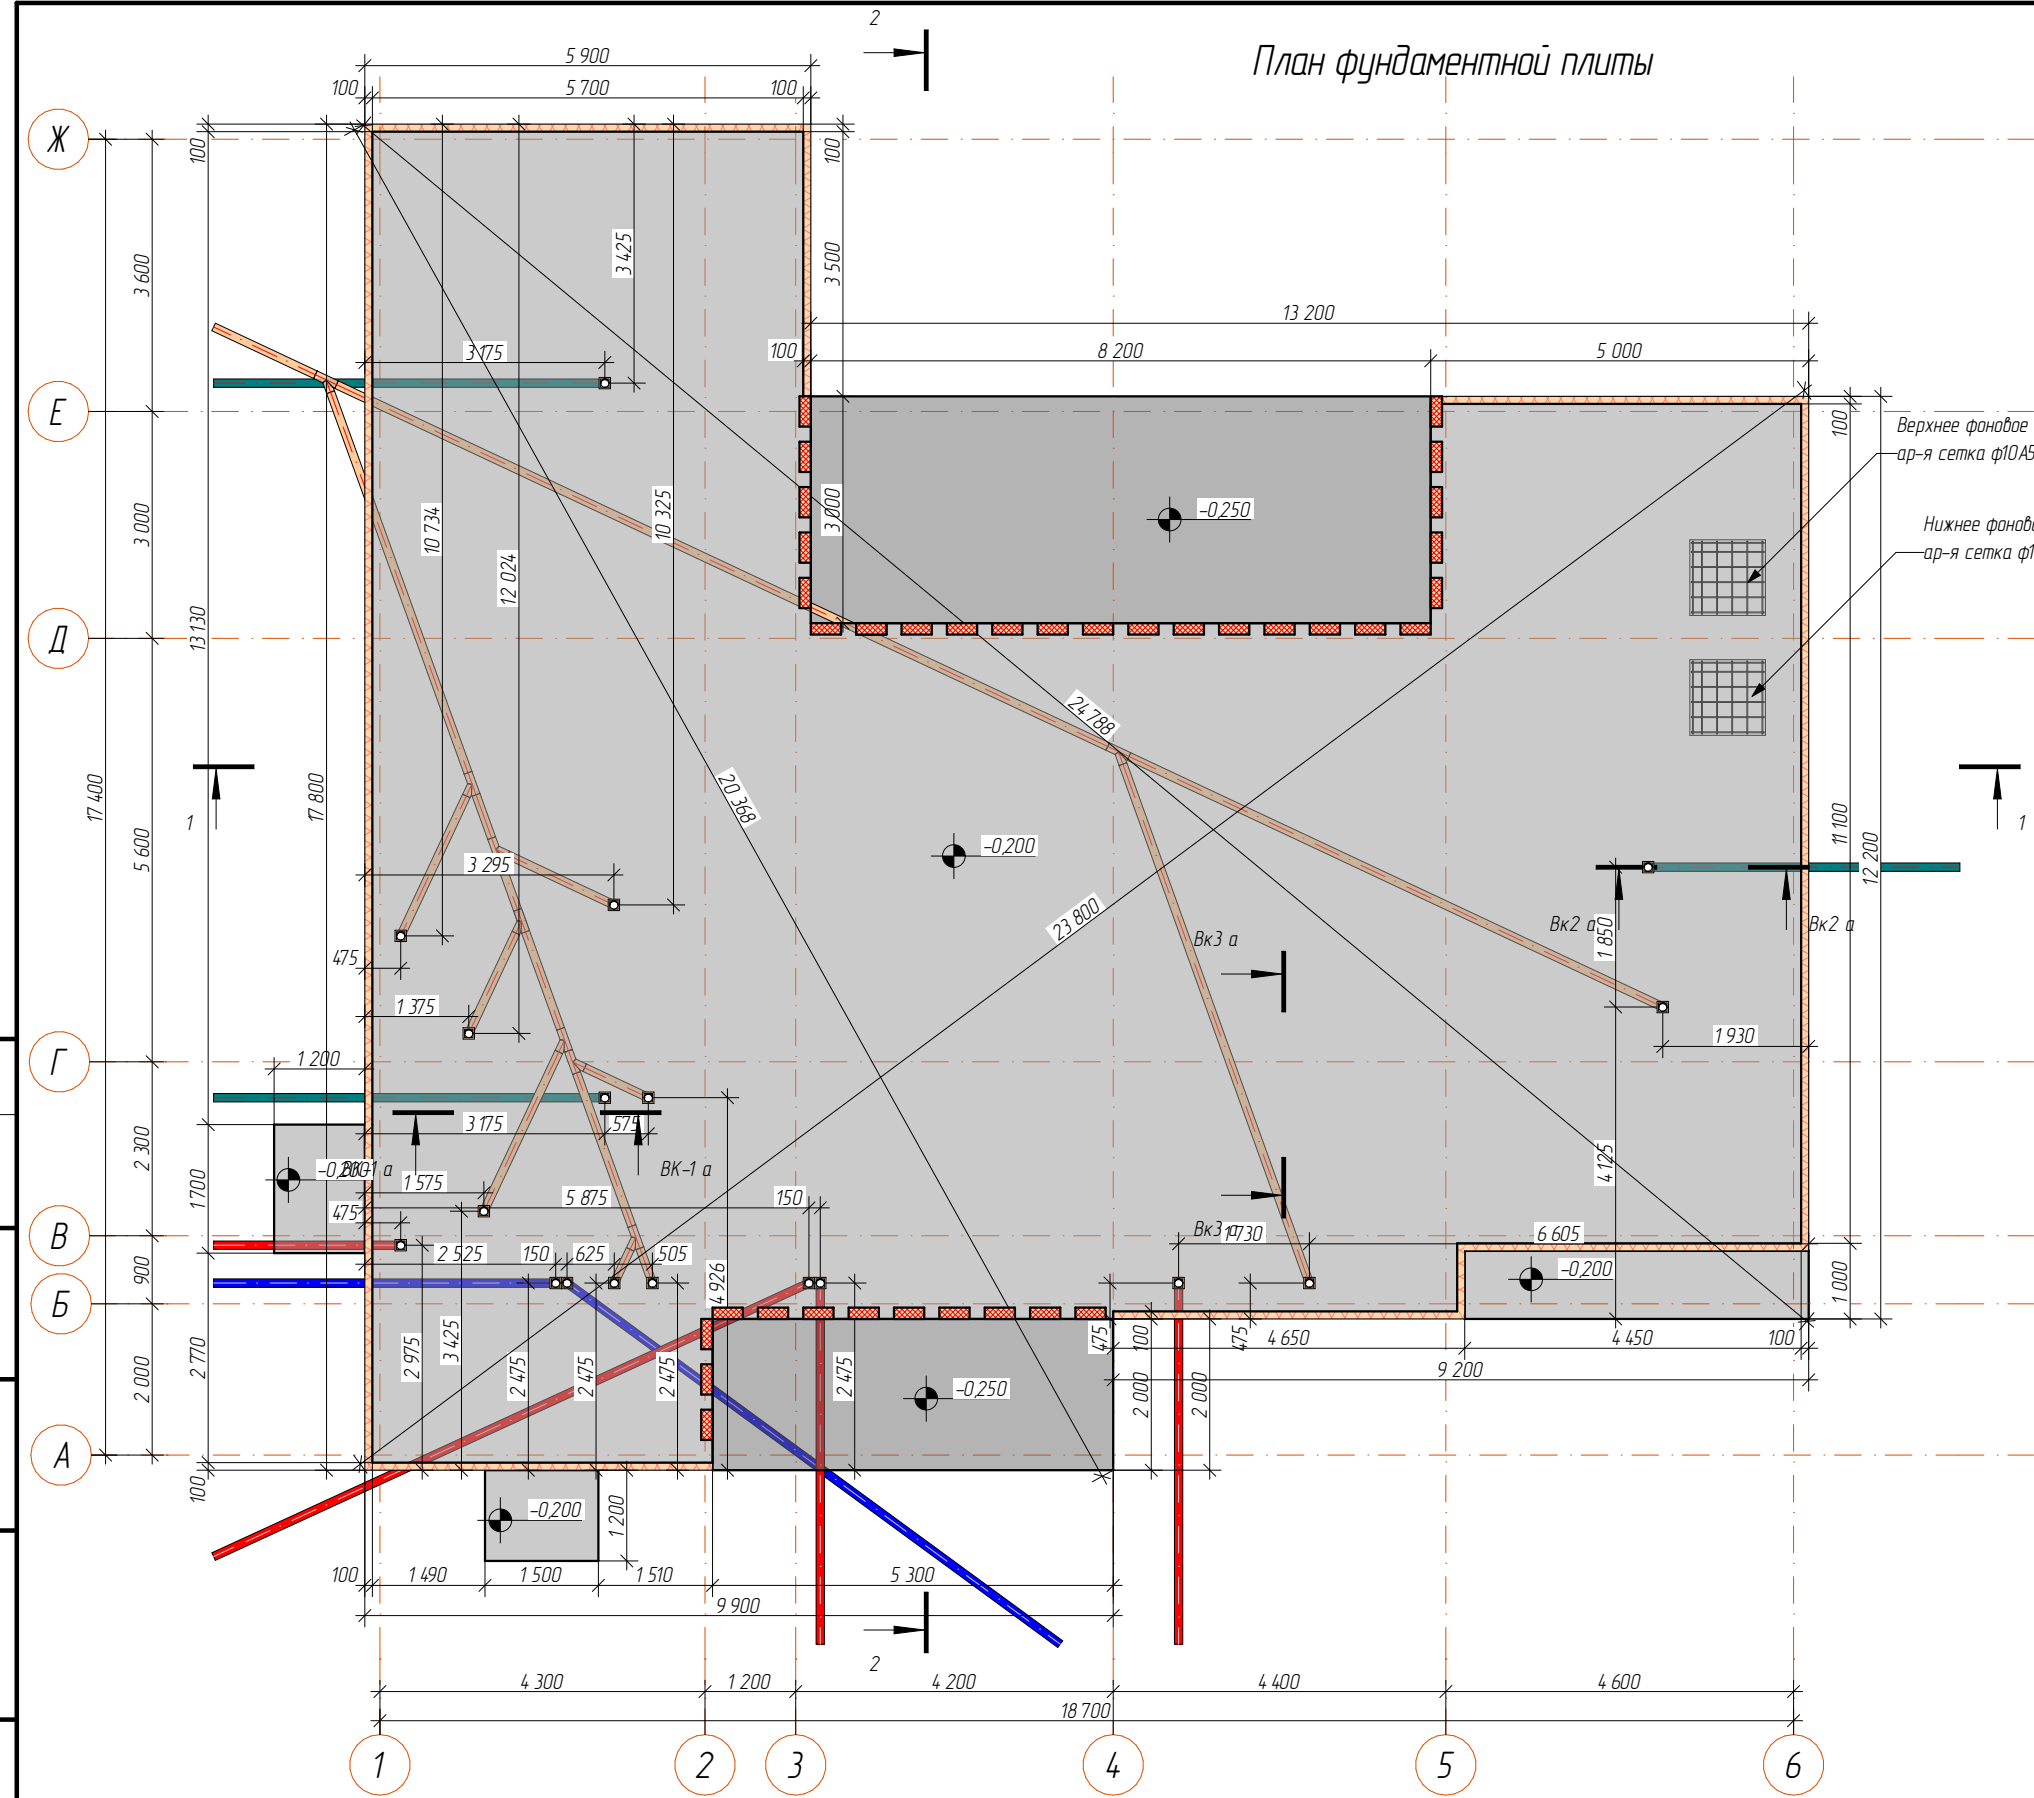

Сечение по фундаментной плите

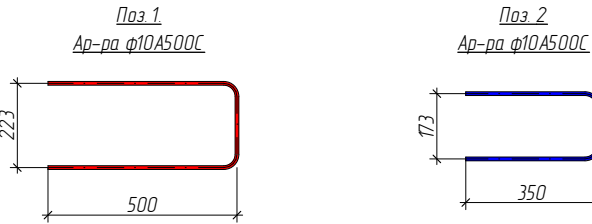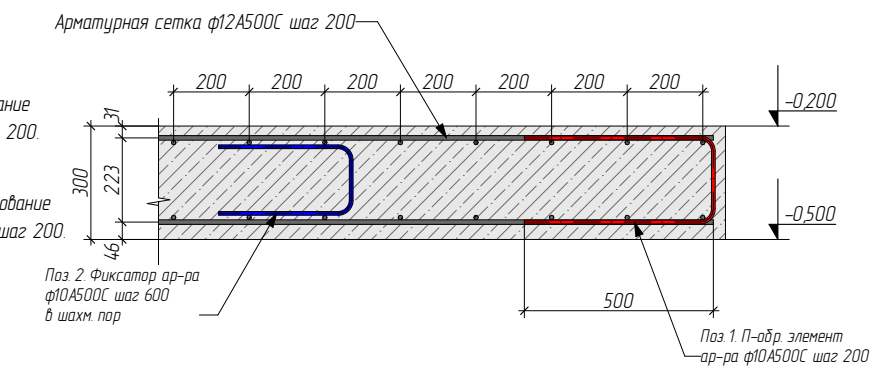

Сечение по плите террасы и крыльца

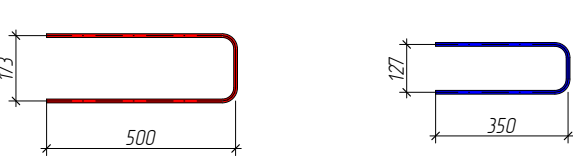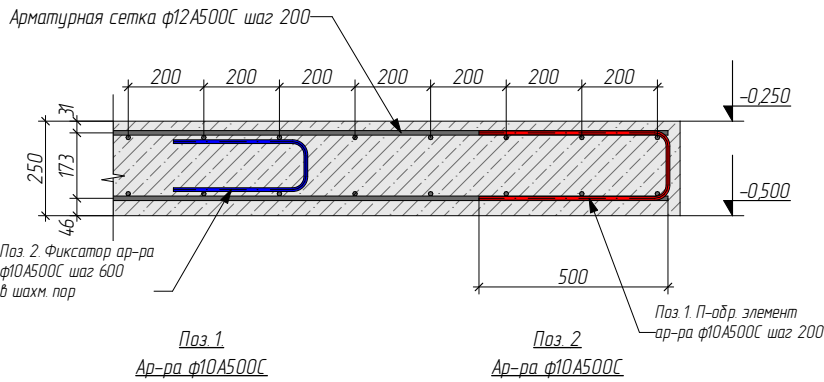

						Проект жилого дома					
Изм.	Кол.уч.	Лист	№ док.	Подпись	Дата						
ГАП		Филатов А.Г.			10.06.2026	Индивидуальный жилой дом по адресу: «Российская федерация, Московская область, г. о. Домодедово, п. Государственного племенного завода "Константиново", тер. КП "Осупово Вилладж" участок с када. номером 50:28:0050421:2962»		Стадия	Лист	Листов	
Разработал								Р	9		
								 Brick House строительство домов под ключ			
План фундаментной плиты											

Спецификация к плану фундаментной плиты

Поз.	Обозначение	Наименование	Кол-во	Масса ед. шт.	Примечание
	ГОСТ 26633-2015	Бетон В 22,5 W6 F150 П4	81		м³
	ГОСТ 32310-2012	ЭППС 100 мм (торец)	175		м³
	ГОСТ 32310-2012	ЭППС 50 мм (низ)	13,5		м³
	ГОСТ 34028-2016	φ12 А500С (сетка)	5950	0,888	м/п
	ГОСТ 34028-2016	φ10 А500С (П-шки, фиксаторы)	1747	0,617	м/п
		Площадь опалубки	23,58		м²
		Площадь утепления торцов	17,5		м²
		Плотность армирования	195		кг на 1 м³

Согласовано

Взам. инв. №

Подпись и дата

Инв. № подл.

Изм.

Кол. уч.

Лист

№ док.

Подпись

Дата

Г.А.П.

Разработал

Филатов А.Г.

10.06.2026

Проект жилого дома

Индивидуальный жилой дом по адресу:
«Российская федерация, Московская область,
г.о. Домодедово, п. Государственного племенного завода
"Константиново", тер. КП "Юсупово Вилладж"
участок с кадастровым номером 50:28:0050421:2962»

Спецификация к плану фундаментной
плиты

Стадия

Лист

Листов


Р

10

Brick House

строительство домов под ключ

План термовставок

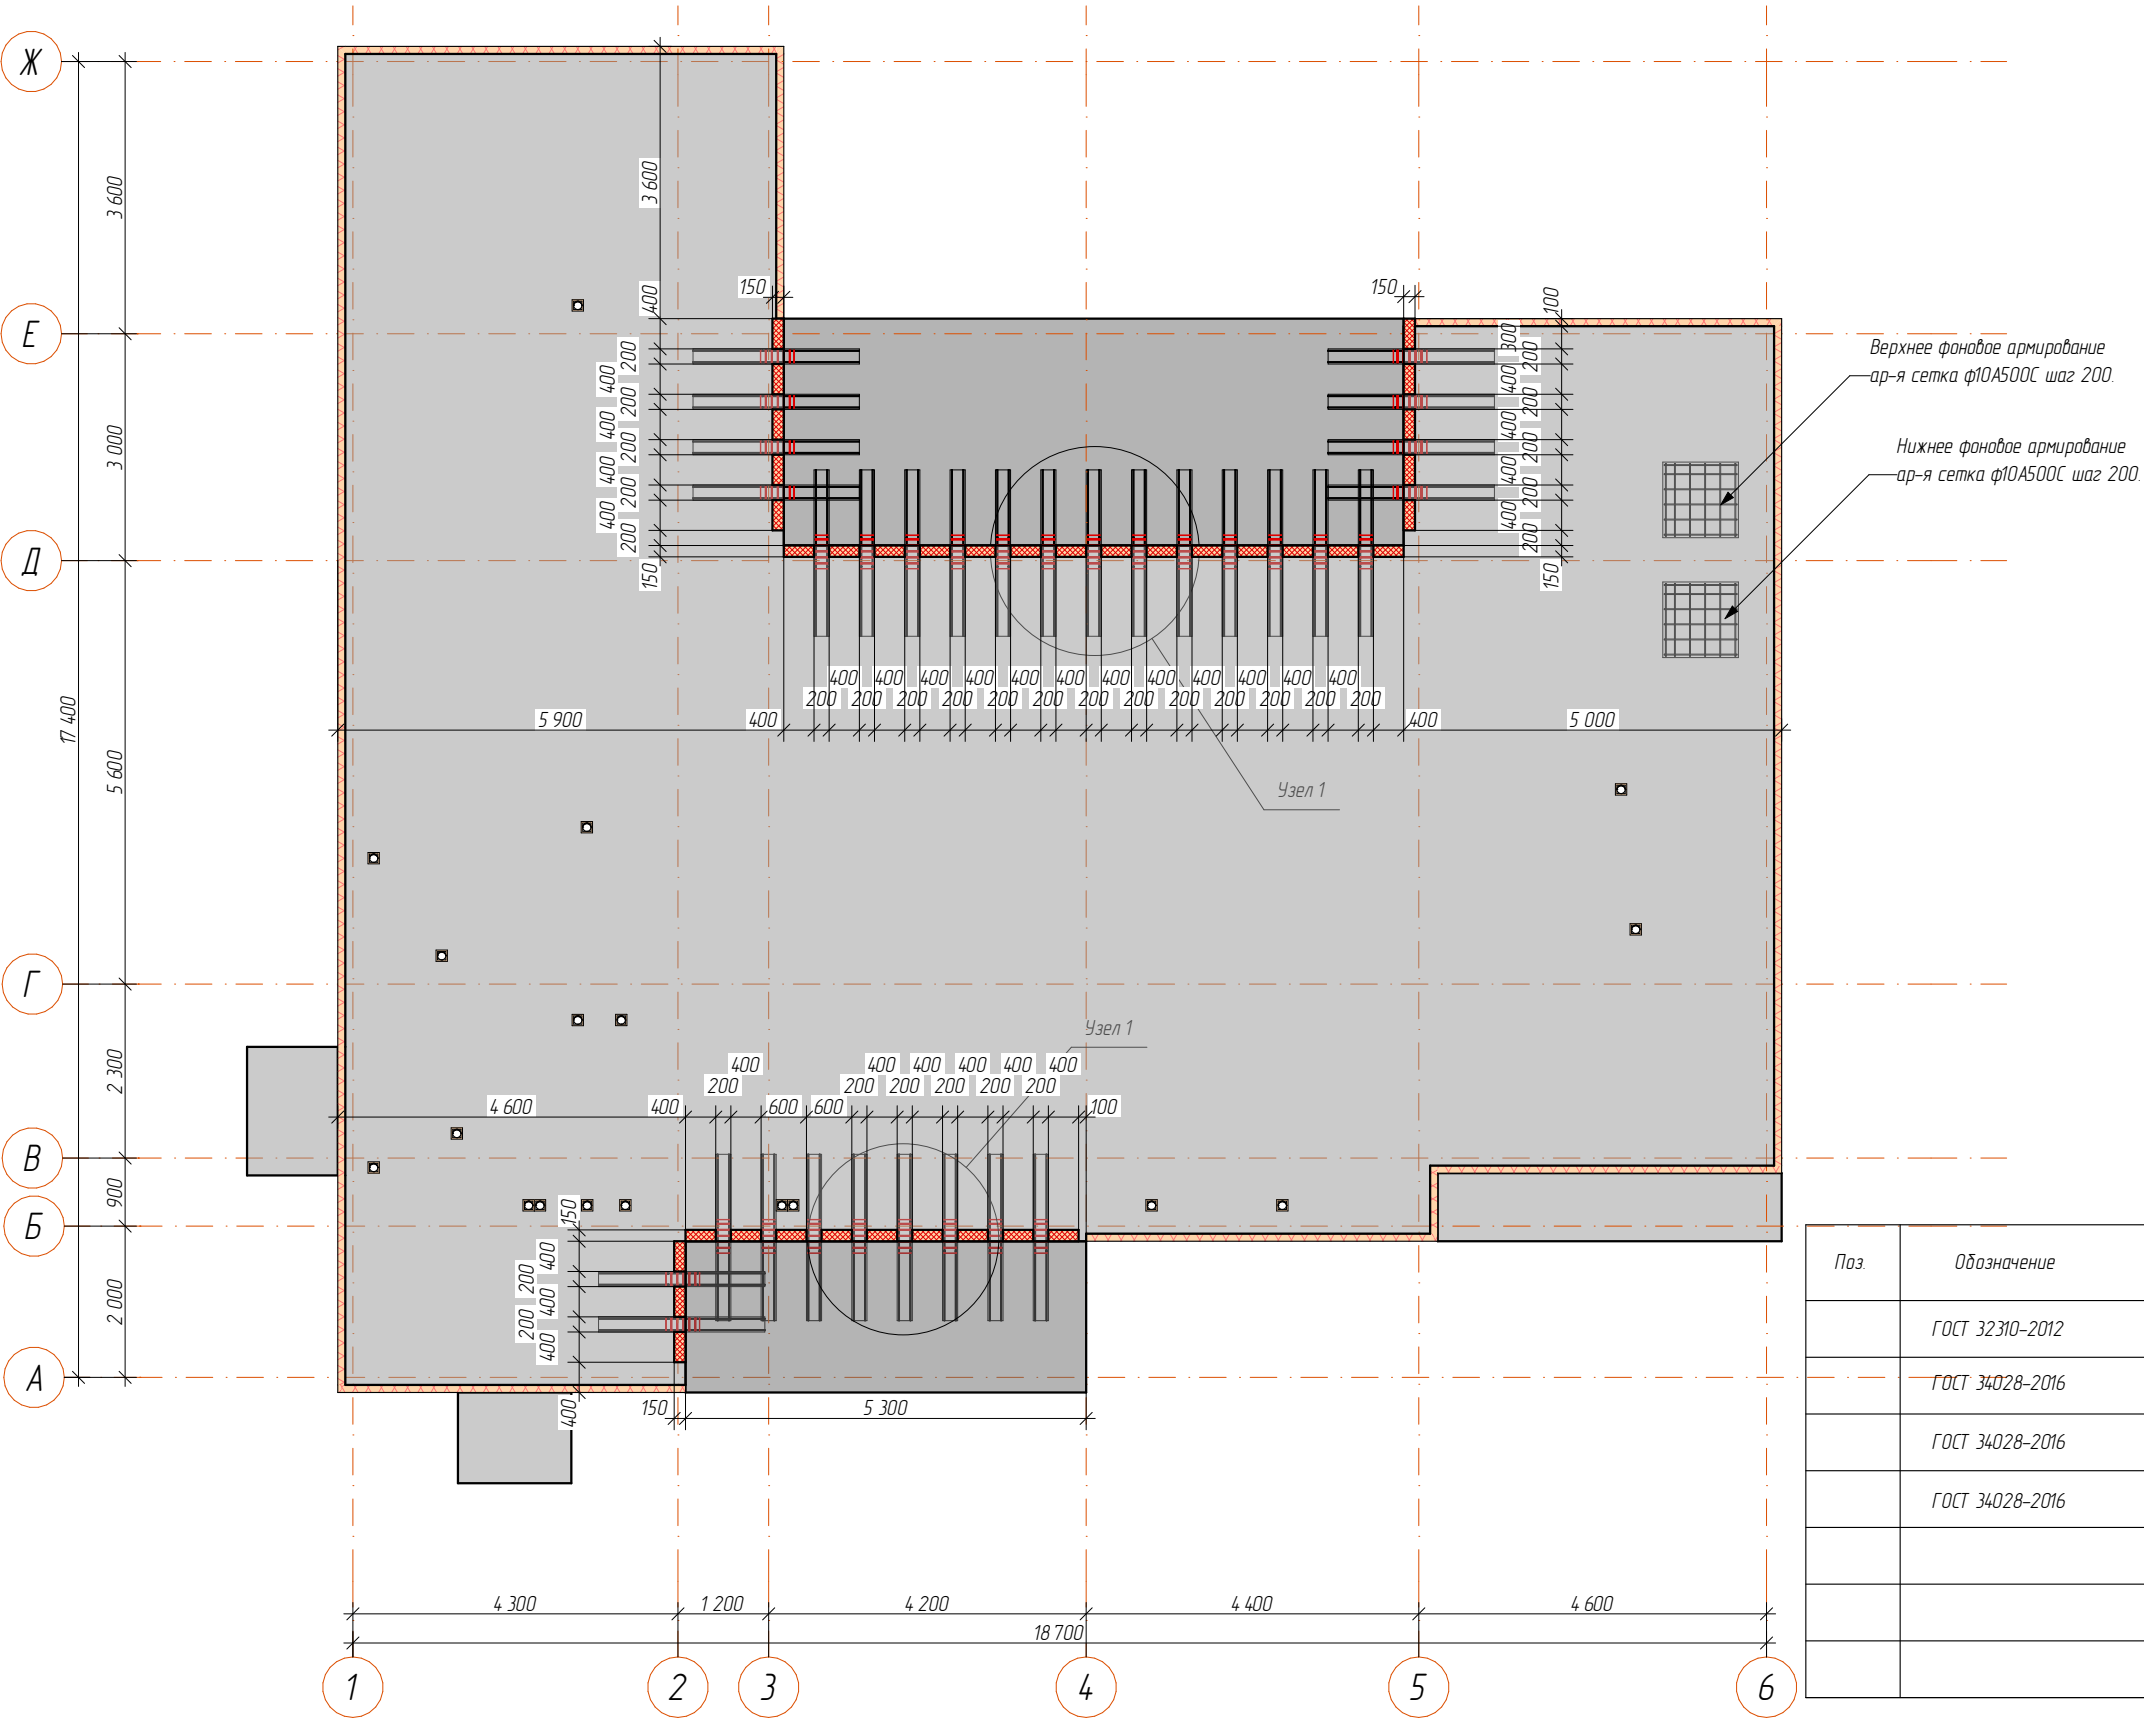

Верхнее фановое армирование
ар-я сетка ф10А500С шаг 200.


Нижнее фановое армирование
ар-я сетка ф10А500С шаг 200.

Поз.	Обозначение	Наименование	Кол-во	Масса ед. шт.	Примечание
	ГОСТ 32310-2012	ЭППС 100 мм (термовставки)	0,4		м³
	ГОСТ 34028-2016	ф16 А500С (ар-я сетка)	328		кг
	ГОСТ 34028-2016	ф12 А500С (ар-я сетка)	122		кг
	ГОСТ 34028-2016	ф6 А240 (хомуты)	35		кг
		Длина термовставок	22		м/п
		Количество термовставок	34		шт
		ЭППС 50 мм (термовставки)	0,2		м³

Согласовано				
Взам. инв. №				
Подпись и дата				
Инв. № подл.				

						Проект жилого дома				
Изм.	Кол.уч.	Лист	№ док.	Подпись	Дата					
ГАП		Филатов А.Г.			10.06.2026	Индивидуальный жилой дом по адресу «Российская федерация, Московская область, г.о. Домодедово, п. Государственного племенного завода "Константиново", тер. КП "Юсупово Вилладж" участок с кад. номером 50:28:0050421:2962»		Стадия	Лист	Листов
Разработал					Р			11		
						План термовставок		 Brick House строительство домов под ключ		


Узлы фундаментной плиты

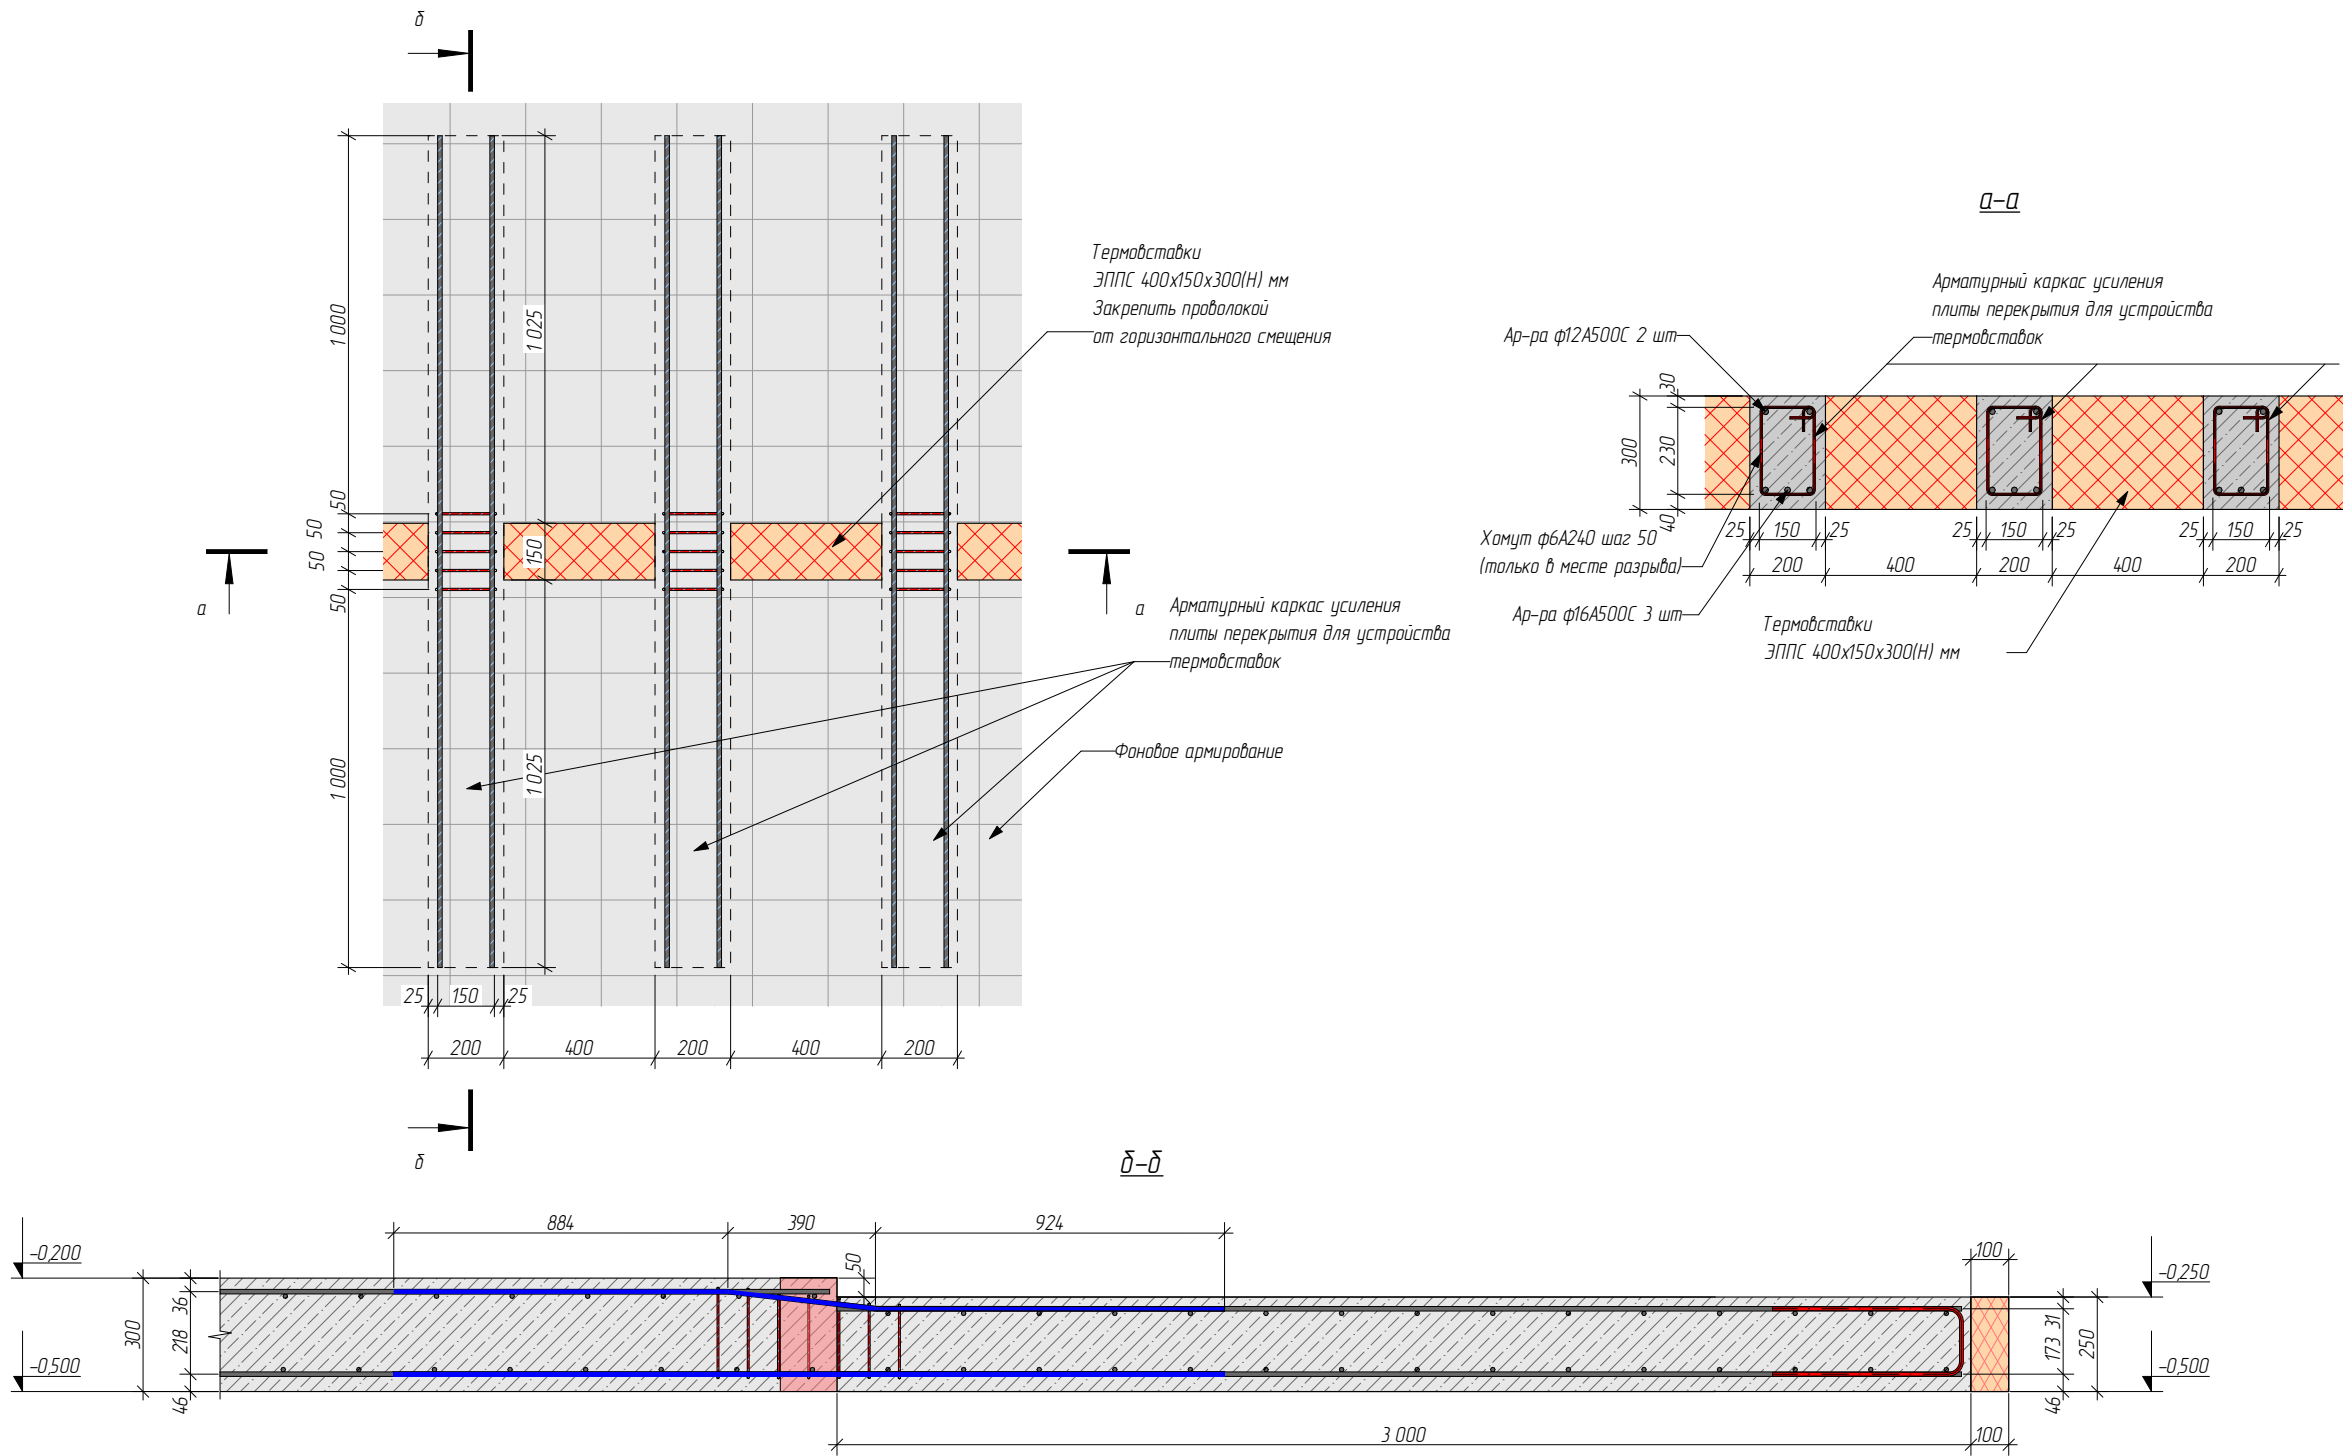

Согласовано			
	Инв. № подл.	Подпись и дата	Взам. инв. №

						Проект жилого дома		
Изм.	Кол. уч.	Лист	№ док.	Подпись	Дата			
ГАП		Филатов А.Г.			11.06.2026	Индивидуальный жилой дом по адресу «Российская федерация, Московская область, г. о. Домодедово, п. Государственного племенного завода "Константиново", тер. КП "Юсупово Вилладж" участок с када. номером 50:28:0050421:2962»		
Разработал						Студия	Лист	Листов
						Р	12	
						 Brick House строительство домов под ключ		
						Узлы фундаментной плиты		

Общий вид фундамента

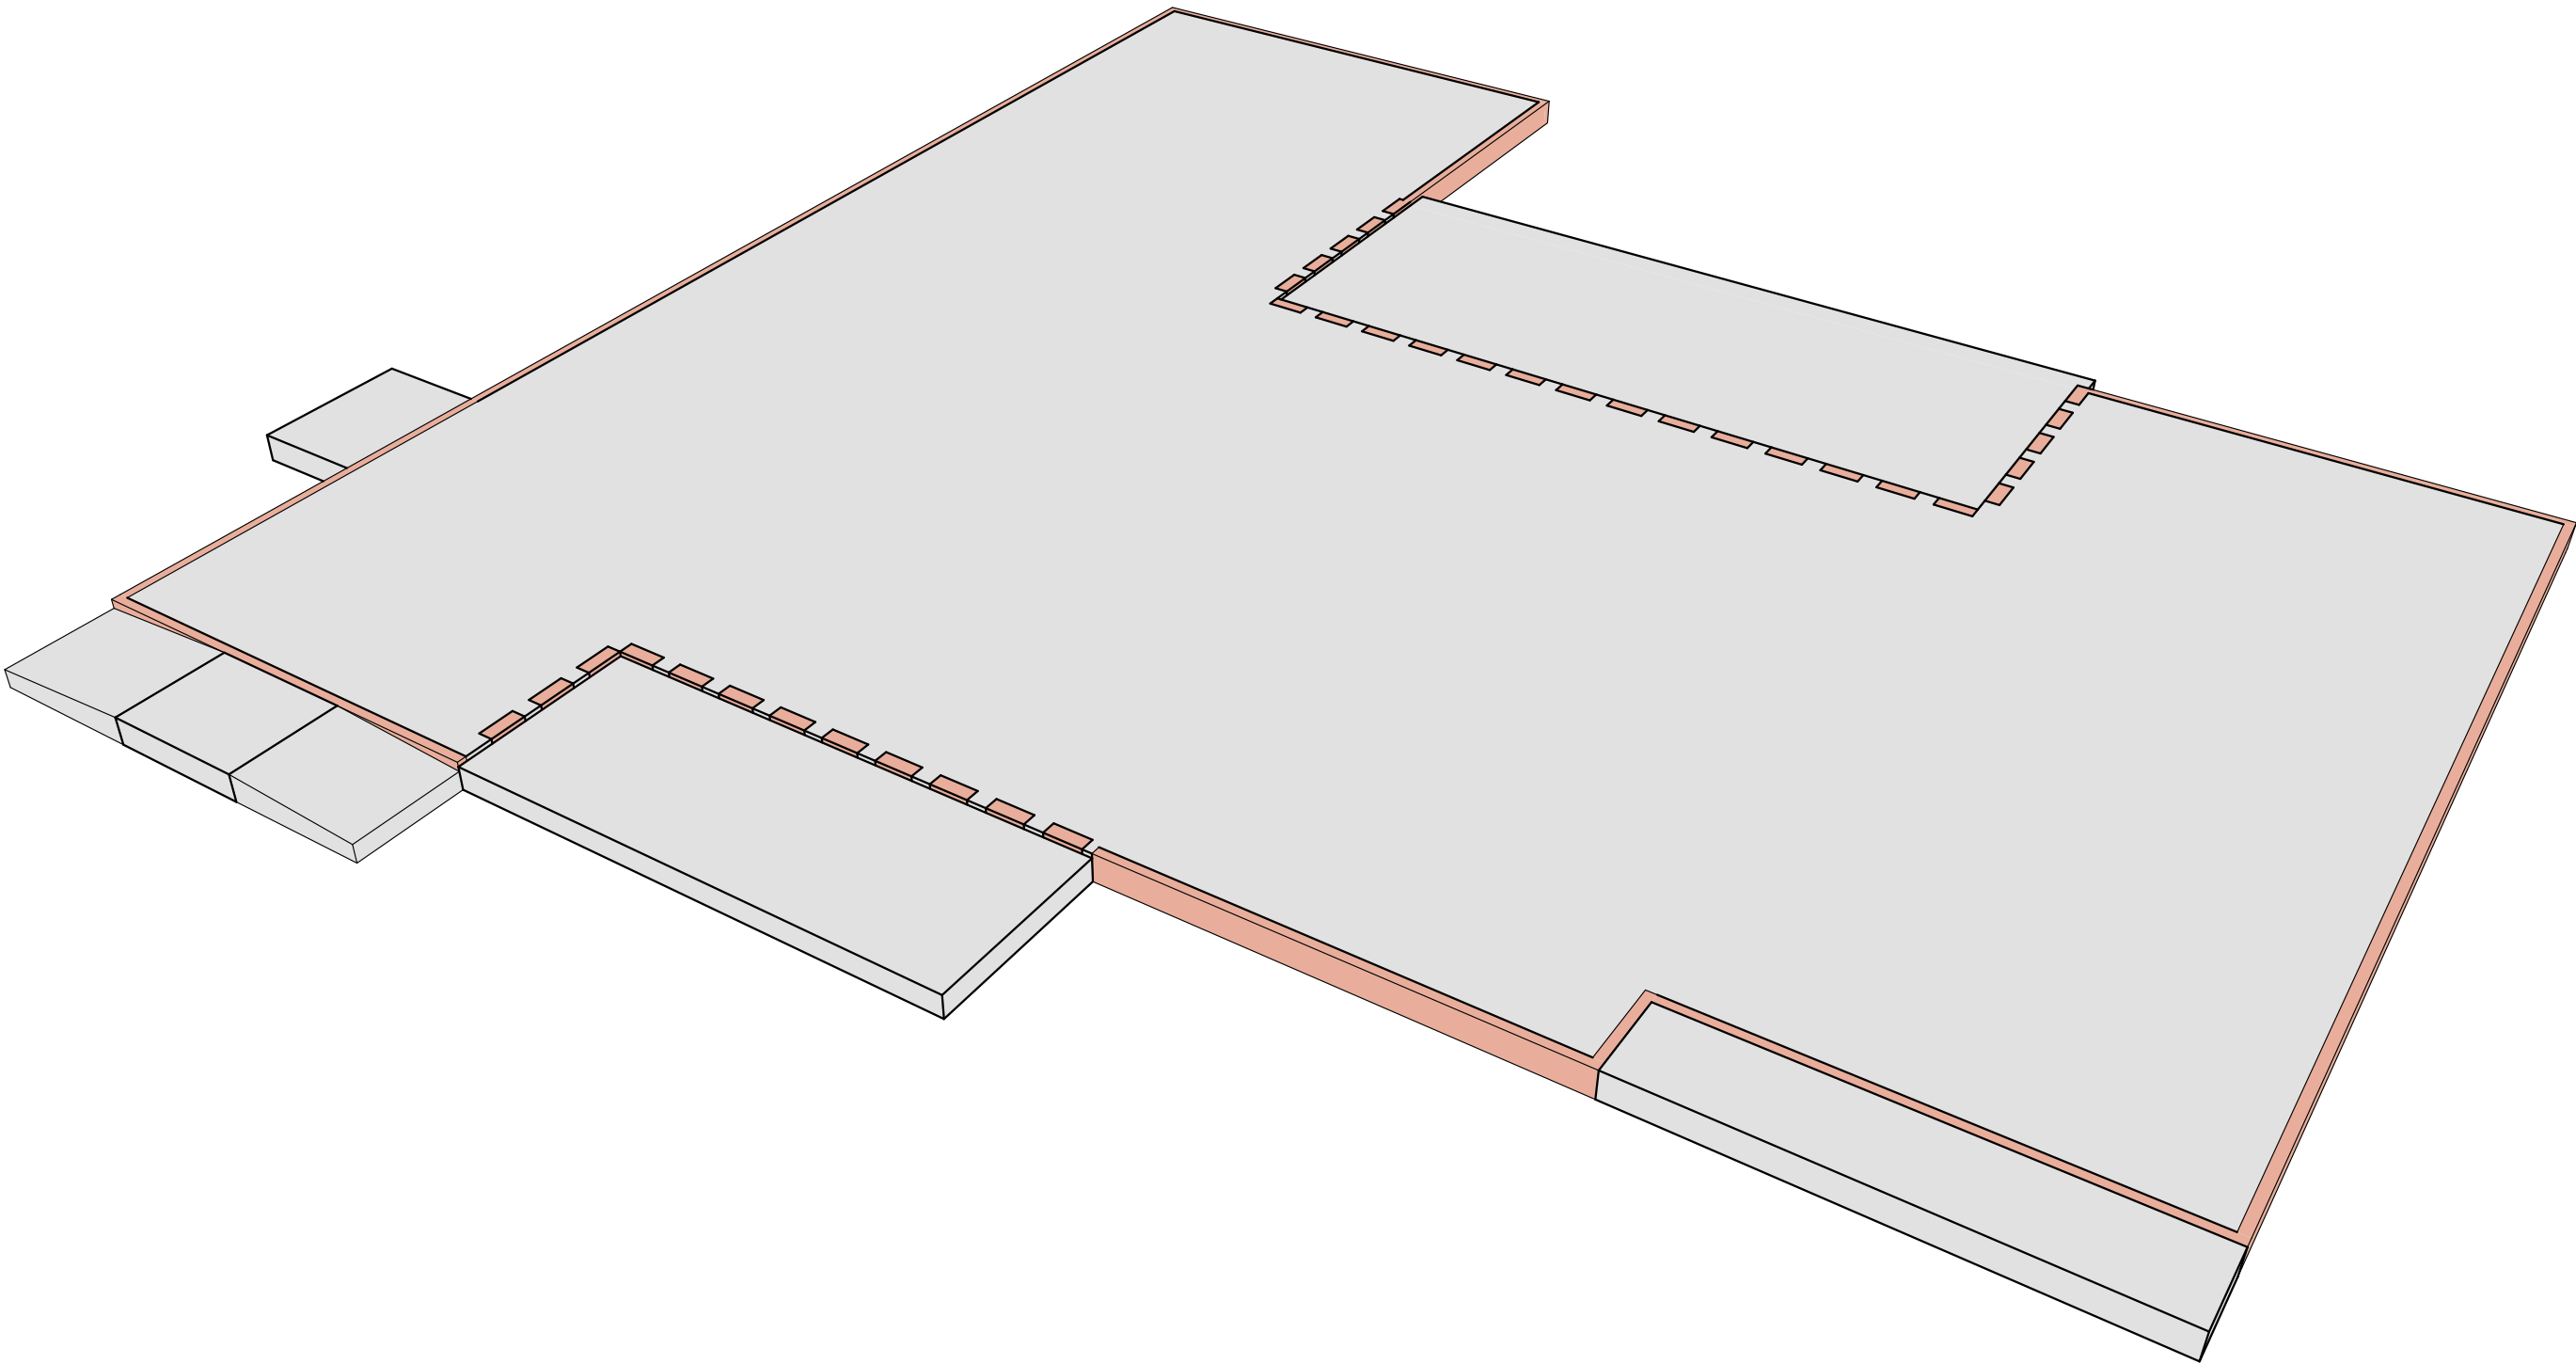

Согласовано				
Взам. инв. №				
Подпись и дата				
Инв. № подл.				

						Проект жилого дома					
Изм.	Кол. уч.	Лист	№ док.	Подпись	Дата	Индивидуальный жилой дом по адресу: «Российская федерация, Московская область, г. о. Домодедово, п. Государственного племенного завода "Константиново", тер. КП "Юсупово Вилладж" участок с кадастровым номером 50:28:0050421:2962»			Стадия	Лист	Листов
ГАП		Филатов А.Г.			10.06.2026				Р	13	
Разработал									Общий вид фундамента		
									Brick House строительство домов под ключ		